
Le Ministère - Grand Remix

PLAN LX ET SCÉNOGRAPHIE - VUE DE DESSUS / TOP

30 OCTOBRE 2026

POUR VALIDATION DT

DJ À GAUCHE / ARTISTE ET ÉCRAN AU CENTRE - TOP 1:65

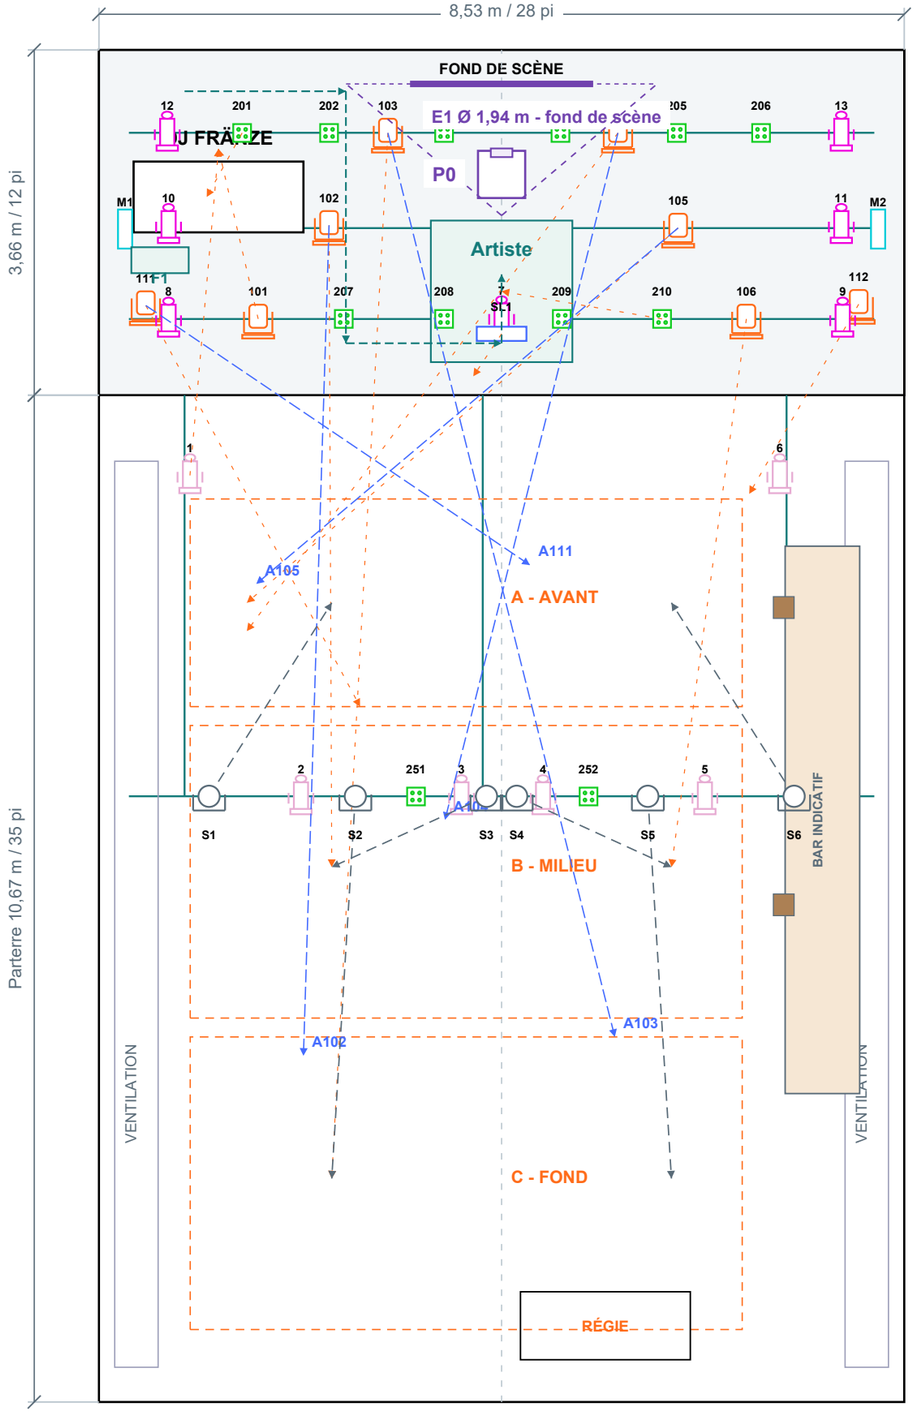

KIT CONSERVÉ

106 et Zoom 5 restent en place. 9, 11, 13, 205, 206, M2 et Zoom 6 réactivés ; orientations revues.

DJ À GAUCHE VUE PUBLIC

Table 1,80 x 0,75 m. Centre x -3,00 ; y +2,10. Bord à 37 cm du mur. Passage artiste par le fond.

ÉCRAN E1 AU FOND DE SCÈNE

Au centre, à la place de l'écran existant. Circonférence 20 pi : diamètre calculé 1,94 m. Centre x 0 ; y +3,30 m.

PROJECTEUR P0 EXISTANT

Point du plan LX original conservé. Centre graphique x 0 ; y +2,34 m. Hauteur et cadrage à relever en salle.

ARTISTE ET LUMIÈRE

Artiste dans l'axe x 0, devant l'écran. Focus latéraux et face ; toile protégée. PAR proposés pour la piste.

COORDONNÉES / MÈTRES

Origine : centre du nez de scène. x : droite public ; y : fond de scène ; z : hauteur depuis le sol salle.

LÉGENDE - APPAREILS DU MINISTÈRE

Symbole	Appareil	Qté	DMX
	ETC Source Four 36°	8*	1
	ETC Source Four 25/50 Zoom	6	1
	Colorado 1 Tour-Tri	12	ARC1 / 3
	Intimidator Spot 375Z	8	15
	DMG SL1 Mix 200 W	1	4**
	DMG Mini Mix 100 W	2	4**
	PAR 56 WFL 500 W	6*	1

KIT CONSERVÉ - APPAREILS RÉACTIVÉS

* Source 36° : 8 inventoriés, 7 dessinés. PAR : implantation proposée.
** SL1 : profil strobe à confirmer (p. 7).

IMPLANTATION DEMANDÉE - REPÈRES

E1 : fond de scène ; bas +1,08 m, haut +3,02 m proposés. Suspension au plafond à valider.

P0 : support Chief VCMU existant conservé. Position graphique, pas un relevé de pose.

S1-S6 : six PAR proposés sur B4 ; disponibilité, gradateurs et charge à confirmer.

Lumière : tous les appareils disponibles. Réglages selon les huit ambiances ; contrôle de la toile au focus.

CARTOUCHE ET BASE DU PLAN

DT : Rémi LeGresley - Le Ministère
Base : fiche Audio-LX et plan LX fourni.
Statut : implantation proposée, à valider sur place.


Le Ministère - Grand Remix

PLAN LX ET SCÉNOGRAPHIE - FRONT / LEFT

30 OCTOBRE 2026

POUR VALIDATION DT

FRONT - VUE DEPUIS LE PUBLIC - 1:50

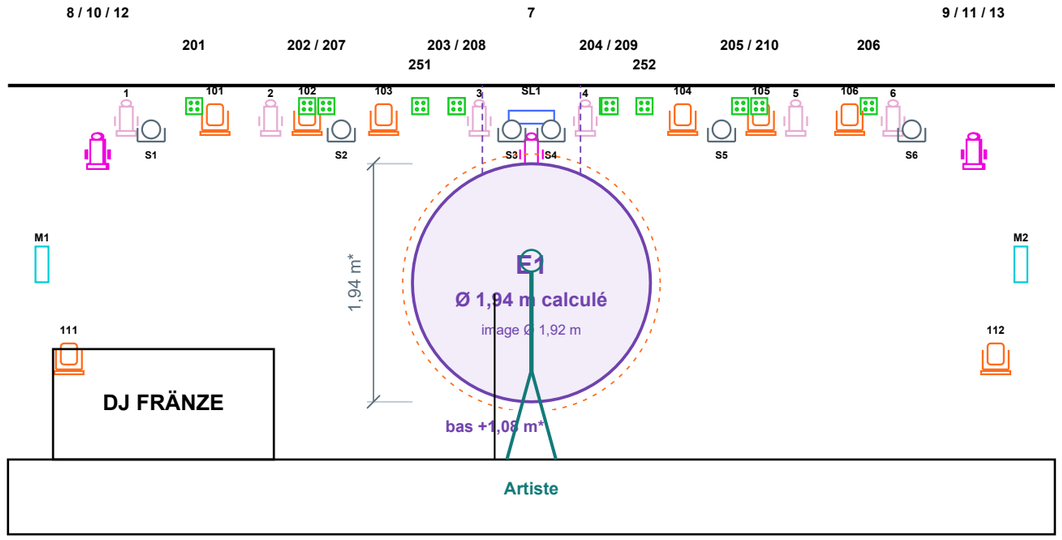


E1 centré au fond de scène. * Hauteur proposée ; cadrage, visibilité et accroches à régler sur place.

LEFT - COUPE DANS L'AXE CENTRAL - 1:65

P0 conservé : emplacement du plan LX original. La fiche salle annonce 5 pi (1,52 m) de son écran 150 pouces, sans préciser le repère de mesure.

Trajet vidéo indicatif. Le maintien du support ne valide pas le cadrage de l'écran rond : mire et focus en salle (p. 4).

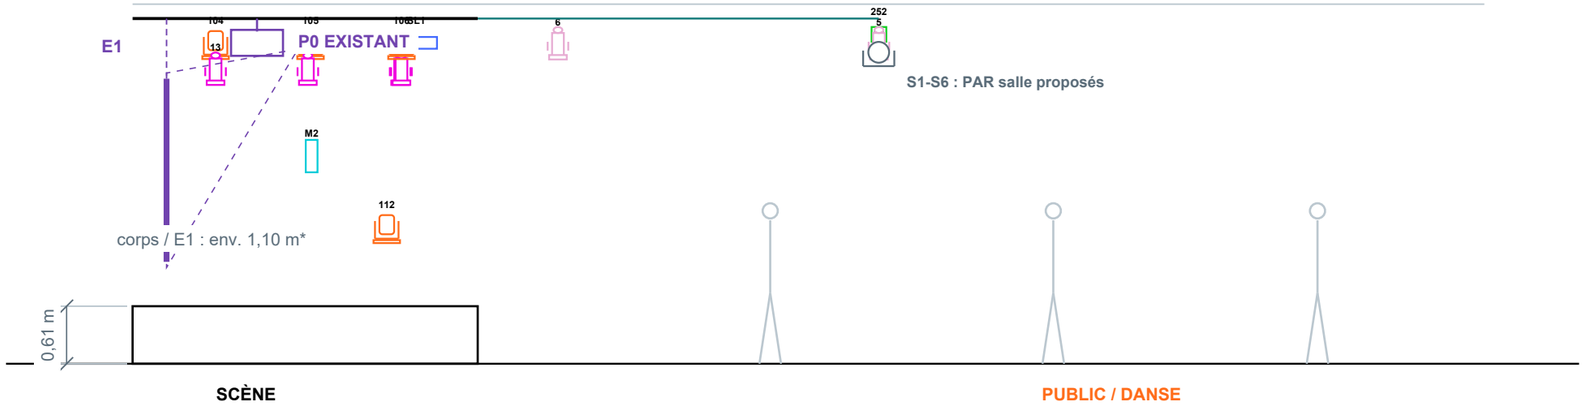

LÉGENDE - APPAREILS DU MINISTÈRE

Symbole	Appareil	Qté	DMX
	ETC Source Four 36°	8*	1
	ETC Source Four 25/50 Zoom	6	1
	Colorado 1 Tour-Tri	12	ARC1 / 3
	Intimidator Spot 375Z	8	15
	DMG SL1 Mix 200 W	1	4**
	DMG Mini Mix 100 W	2	4**
	PAR 56 WFL 500 W	6*	1

KIT CONSERVÉ - APPAREILS RÉACTIVÉS

* Source 36° : 8 inventoriés, 7 dessinés. PAR : implantation proposée.
** SL1 : profil strobe à confirmer (p. 7).

NOTES TECHNIQUES DE MONTAGE

Montage LX. Conserver tout le kit existant, dont 106 et Zoom 5. Profil strobe SL1 à confirmer (p. 7).

Scénographie. E1 centré au fond de scène, artiste au centre et DJ à gauche. Valider visibilité, dégagements et accès artiste.

Public. S1-S6 sur B4 : 6 x 500 W = 3 kW. Confirmer accroches et gradateurs ; régler la couverture sans éblouissement.

Accroches. Points approuvés par le DT, fixation et sécurité secondaire. Aucun appareil sur les rails à rideaux.

Projection. P0 au point original. Confirmer la référence de lentille, le cadrage et le focus (p. 4 et 6).


Le Ministère - Grand Remix

VUE D’ENSEMBLE LX / IMPLANTATION ET SPÉCIFICATIONS

30 OCTOBRE 2026

POUR VALIDATION DT

ISOMÉTRIE DE REPÉRAGE - SANS ÉCHELLE - IMPLANTATION PROPOSÉE

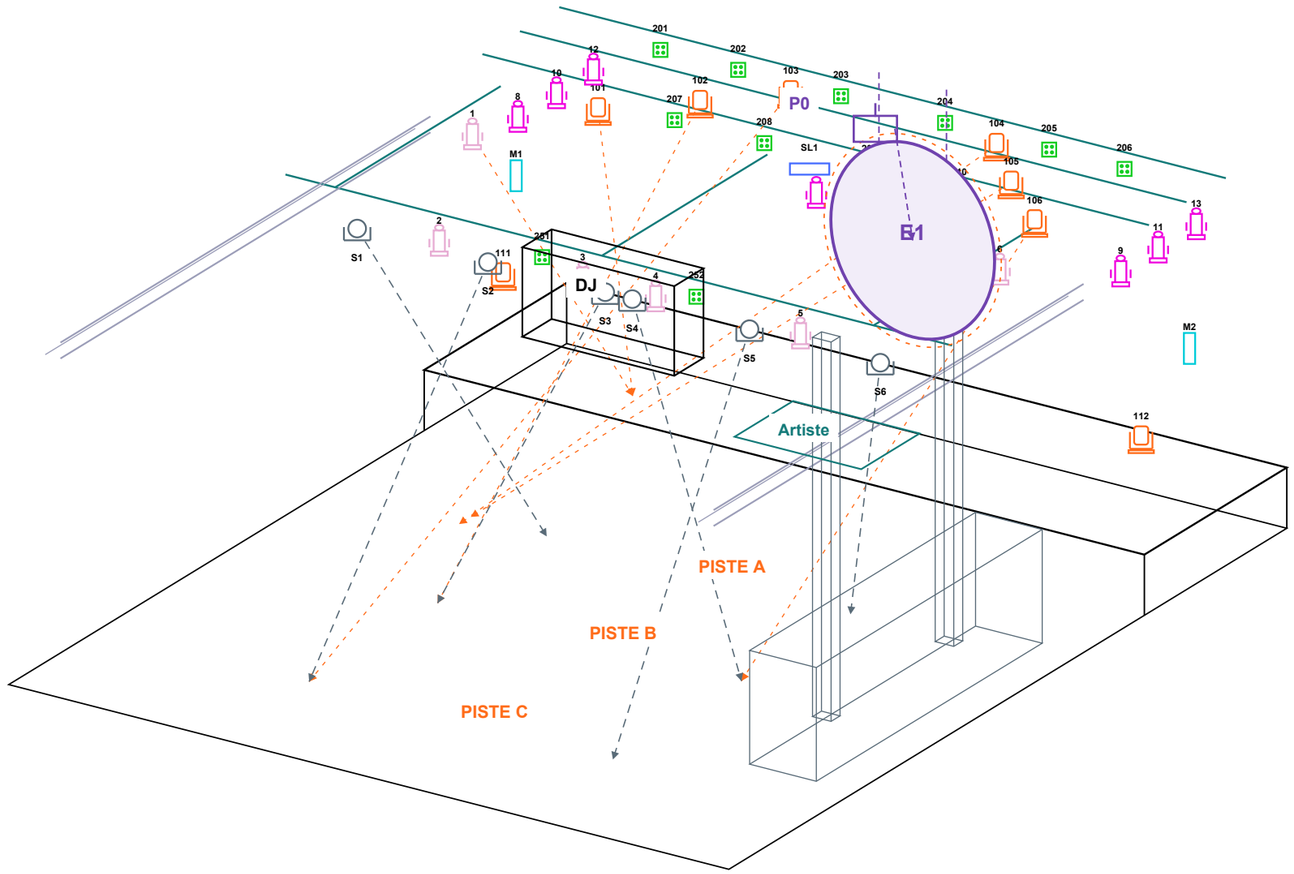

S1-S6 : 6 PAR proposés au-dessus de la piste. 106 et Zoom 5 conservés ; appareils auparavant exclus réactivés.

COTES À REPORTER ET RÉGLAGES POUR LE DT

Élément	Cote / destination	Application
E1 - écran	x 0 ; y +3,30 ; Ø 1,94 m calculé	Fond de scène, à la place de la toile existante. Bas proposé +1,08 m / sol salle.
P0 - vidéo	x 0 ; y +2,34 ; z +3,40 m indicatifs	Point du plan LX original conservé. Support Chief VCMU existant ; cadrage à vérifier.
DJ / artiste	DJ : x -3,00 ; y +2,10. Artiste : x 0 ; y +1,10.	Table 1,80 x 0,75 m. Artiste dans l’axe de scène, devant la projection.
PAR S1-S6	y -4,25 ; x -3,10 / -1,55 / -0,16 / +0,16 / +1,55 / +3,10.	Hauteur de corps proposée +3,30 m. S1/S6 : A ; S3/S4 : B ; S2/S5 : C.

Sources : fiche Audio-LX et plan LX du Ministère ; Panasonic PT-RZ770 Spec File. Cotes de projet proposées, à confirmer sur place.

ÉQUIPEMENTS TECHNIQUES LX - FICHE SALLE

Appareil	Qté	Donnée principale
Colorado 1 Tri Tour	12	LED RGB / ARC1
Intimidator Spot 375Z	8	6 suspendus + 2 bas
Source Four 25-50°	6	6 conservées
Source Four 36°	8	575 W / 7 dessinés
DMG SL1 Mix	1	200 W
DMG Mini Mix	2	100 W
PAR 56 WFL	6	500 W / S1-S6 proposés

Console : GrandMA3 Command Wing Compact / PC.
Gradateurs : 4 Lite-Putter DX-1210.
DMX : Chauvet Data Stream 4.
Brouillard : Antari F-1W.
Bar : éclairage maintenu.

VIDÉOPROJECTION - DONNÉES DOCUMENTÉES

Panasonic PT-RZ770
Laser DLP, 7 000 lm nominaux.
1920 x 1200 / 16:10 ; HDMI.

Installation existante : Chief VCMU, ultra-courte focale, à 5 pi (1,52 m) de l’écran 16:9 de 150 pouces selon la salle.

Projet : toile ronde Ø 1,94 m calculé, avec masque circulaire.

Courte focale annoncée : ET-DLE03S. Référence exacte et cadrage à confirmer ; p. 4.

ÉCRAN ROND AU FOND DE SCÈNE / PROJECTEUR AU POINT ORIGINAL

Panasonic PT-RZ770 sur support Chief VCMU existant. Écran rond centré à la place de la toile de la salle. Aucune relocalisation du projecteur sur B4.

Élément	Donnée retenue	Vérification en salle
Écran E1	20 pi / 6,096 m de circonférence ; Ø 1,94 m calculé	Mesurer le cerceau monté ; vérifier planéité et suspension.
Emplacement	Fond de scène, axe x 0 ; y +3,30 m indicatif	Devant le rideau du fond ; hauteur à ajuster au cadrage.
Projecteur P0	Point du plan LX original conservé	Cotes graphiques : x 0 ; y +2,34 ; z +3,40 m indicatifs.
Optique annoncée	Panasonic ET-DLE03S - courte focale	Lire la référence exacte sur la lentille : ET-DLE035 à confirmer.
Installation documentée	Support Chief VCMU ; écran salle 16:9 de 150 pouces	Fiche salle : recul 5 pi / 1,52 m, repère de mesure non précisé.
Image visible	Cercle Ø 1.92 m ; bord blanc 1 cm	Masquer le contenu hors cercle ; vérifier la netteté sur toute la toile.

CADRAGE À VALIDER - CALCUL CONDITIONNEL ET ESSAI

Hypothèse ET-DLE035	Calcul pour le gabarit minimal	Portée
Image native 16:10	3.297 x 2.060 m ; diagonale 3.888 m	Gabarit minimal : cercle + marge de réglage.
Recul au miroir interne	0,3205 x 3.888 + 0,0047 = 1.251 m	Formule Panasonic ; approximation ±5 %, pas une cote de pose.
Projecteur maintenu en place	Mesurer l’image obtenue au point existant	Une image plus grande peut être masquée ; vérifier couverture, décalage vertical et focus.

Essai requis : afficher une mire, régler le centre puis les bords, ajuster le masque circulaire et la hauteur de la toile. La maquette représente l’implantation demandée ; elle ne certifie pas le cadrage ni la netteté de l’installation réelle.

Sources : plan LX et fiche Audio-LX du Ministère ; Panasonic ET-DLE035, annexe 9. Modèle exact à confirmer.


Le Ministère - Grand Remix

BARRES ET PRIORITÉS D’ACCROCHE - REPÉRAGE DEPUIS LE PLAN SOURCE

30 OCTOBRE 2026

POUR VALIDATION DT

GRILLE SEULE - SECTIONS VIDES VISIBLES - COTES GRAPHIQUES APPROXIMATIVES

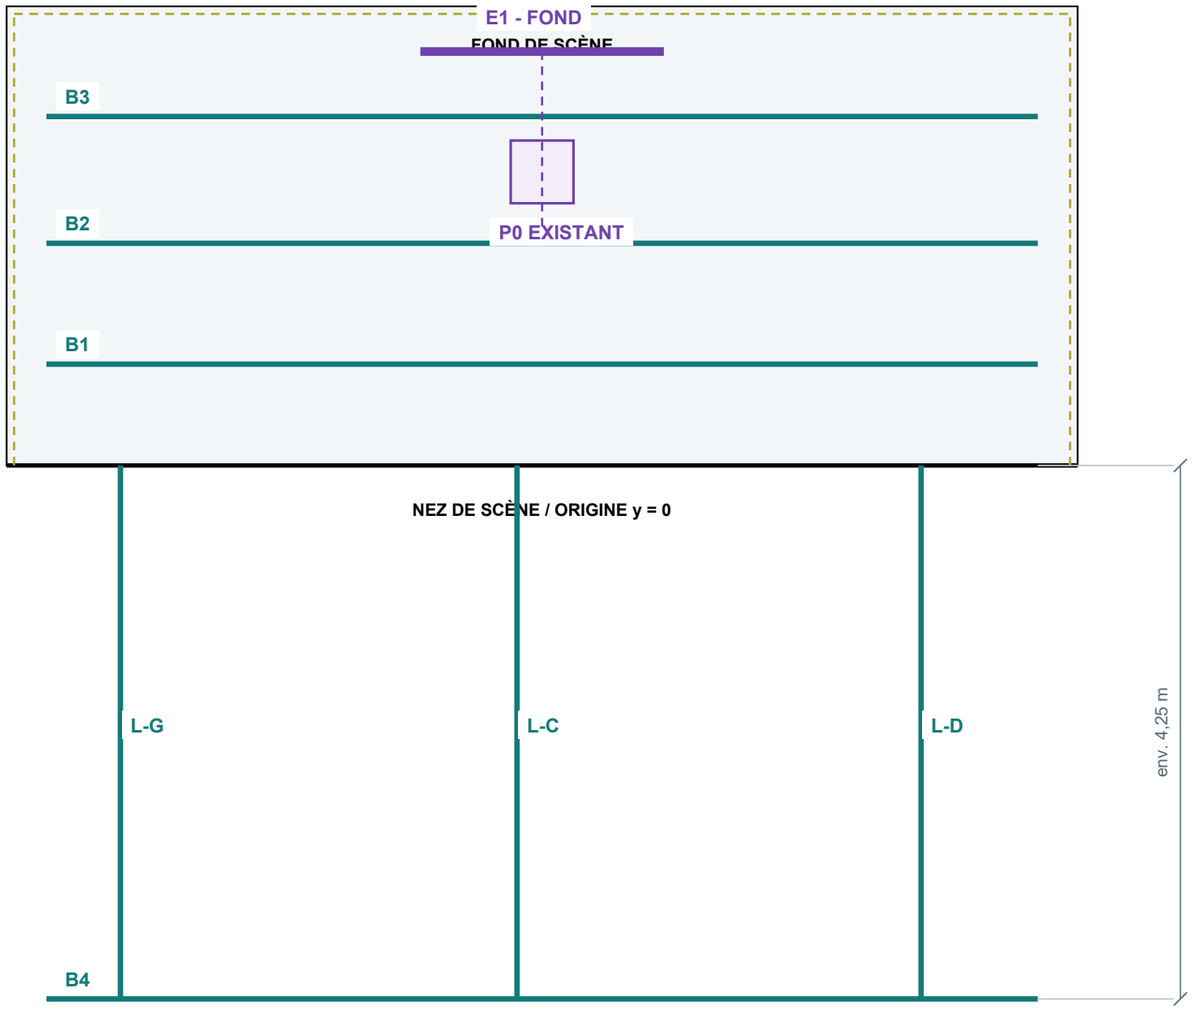

Vert : tubes repérés. Jaune : rails à rideaux, accroche interdite.

Une section sans appareil n’est pas un point de charge validé.

POINTS PROPOSÉS ET LIMITES DU REPÉRAGE

Traverses B1-B3.
y ≈ +0,807 / +1,77 / +2,78 m.

Traverse B4.
y ≈ -4,25 m. PAR S1-S6 proposés ; Zoom 5 conservé.

Longitudinales L-G / L-C / L-D.
x ≈ -3,36 / -0,20 / +3,02 m. Continuité et extrémités à relever.

Section publiée.
Tube carré 2 x 2 pouces / 50,8 mm.

Implantation retenue.
P0 : support existant conservé.
E1 : centré au fond, suspension au plafond à confirmer.
106 et Zoom 5 conservés.

Accord du DT avant montage.
Confirmer nature des tubes, charges admissibles, suspension E1 et sécurité secondaire. Aucun rail à rideaux, conduit ou élément décoratif utilisé.

Repérage graphique, sans relevé complet des points d’accroche.

DESTINATIONS ET POINTAGES - VIDÉO ACTIVE

Appareils	Destination	Slam + vidéo	Danse + vidéo
101, 8, 10, 12, 201, 202, 207, 1, M1	DJ	DISPONIBLE	DISPONIBLE
102, 103, 104, 105, 111, 106	ARTISTE / PISTE	DISPONIBLE	DISPONIBLE
112*, S1, S2, S3, S4, S5, S6*	PISTE	DISPONIBLE	DISPONIBLE
7, 9, 11, 13, 203, 204, 205, 206, 208, 209, 210, 6	ARTISTE	DISPONIBLE	DISPONIBLE
251, 252, 2, 3, 4, SL1, 5	AVANT-SCENE	DISPONIBLE	DISPONIBLE
M2	AVANT-SCENE DROITE	DISPONIBLE	DISPONIBLE

DISPONIBLE : focus utilisable, selon l'ambiance. Les appareils éteints restent en place.
112* : OFF à l'accueil, à l'ouverture et dans Pinky love. S6* : selon ambiance.

ACCUEIL	Pan / tilt / zoom	Cible x / y / z (m)
102	-1.8° / 68.9° / 10°	-2.100 / -7.000 / +0.000
103	+14.1° / 71.0° / 10°	+1.200 / -6.800 / +0.000
104	-14.1° / 65.6° / 15°	-0.600 / -4.500 / +0.000
105	-49.8° / 59.8° / 12°	-2.600 / -2.000 / +0.000
111	+56.0° / 73.6° / 10°	+0.300 / -1.800 / +0.000

Accueil proposé : axes fixes, blanc à 100 %, sans gobo ni flash. Angles de repérage, non calibrés DMX.

Cibles fixes x / y / z (m)
Zoom 1 / 101 vers DJ : -3,00 / +2,61 / +2,00 ; Zoom 1 à 25°.
201 vers platines : -3,125 / +2,10 / +1,62 ; sans flash.
Artiste : 0,00 / +1,10 / +1,6096.
203 / 204 / 206 / 210 vers haut du corps : 0,00 / +1,10 / +2,00.
SL1 vers avant-scène : -0,30 / +0,20 / +1,20.

CONSIGNES POUR LE FOCUS ET LA PROGRAMMATION

1. Protéger E1.
Aucun éclairage direct sur la face ou le dos. Réserve de contrôle : rayon 1,20 m, soit Ø 2,10 m + 15 cm de marge radiale. Gabarit de conception, à vérifier par essai.

2. Découpes et lyres.
Régler couteaux et zoom ; calibrer les zéros. Contrôler les bords du faisceau sur tout le parcours et limiter les amplitudes. Garder le trajet vidéo libre.

3. Lyre 112 vers le public.
Base : pan -30°, tilt 58°, zoom 12°, balayage ±6°. Cible : x +2,6243 ; y -1,0457 ; z 0 m. Focus à valider sans débordement sur E1.

4. États et permanences.
Bar maintenu ; platines lisibles avec 201, sans flash. 9, 11, 13, 205, 206, M2 et Zoom 6 réactivés ; 106 et Zoom 5 conservés. Ambiances suggérées : p. 8.

5. Essai de focus.
Mire blanche puis noire ; chaque appareil séparément. Corriger orientation et découpe, puis tester les mouvements et le brouillard. Laisser éteint tout faisceau atteignant directement la toile.

Le Ministère - Grand Remix

APPAREILS - CAPACITÉS ET LIMITES

Appareil / inventaire	Fonctions envisagées pour le spectacle	Réalité du matériel / points à confirmer
Intimidator Spot 375Z IRC 8 inventoriés	Pan 540° ; tilt 270° ; zoom 10-23°. Roue : blanc, orange, lime, cyan, rouge, vert, magenta, jaune. Sept gobos rotatifs plus ouverture. Parcours de pan/tilt à programmer sur la console.	Huit lyres disponibles, dont 106 conservée à son point existant. Zéros, parcours et focus à valider. Motifs issus du manuel ; jeu installé à vérifier. Prismes non retenus dans cette étude. Accents proposés jusqu'à 2 Hz, distincts des capacités maximales du matériel.
ETC Source Four 36° 8 inventoriés, 7 dessinés	Intensité ; blanc ou noir (éteint).	575 W selon la salle. Appareil fixe : orientation et couteaux manuels, aucun moteur. Gélatines non confirmées : aucune couleur ajoutée. Le huitième appareil reste non localisé.
ETC Source Four Zoom 25-50° 6 inventoriés	Intensité ; blanc ou noir (éteint).	750 W. Zoom, focus et couteaux manuels. Ouverture de référence : 25°, à adapter sur place. Zoom 5 conservé et Zoom 6 réactivé ; focus revus vers l'avant de scène.
COLORado 1-Tri Tour 12 inventoriés	Mélange RGB, intensité visuelle ; noir.	Fixe, orientation manuelle. 210 orienté vers le haut du corps de l'artiste. Manuel v2 rev.4 : cœur 15°, champ doux 28° ; version/diffuseur à vérifier. ARC.1 : trois canaux RGB, sans dimmer séparé.
DMG SL1 MIX / MINI MIX 1 SL1 / 2 MINI	Couleur LED et intensité. SL1 : accents blancs à 8 Hz, crête 80 % dans Rouge intense.	200 / 100 W ; six couleurs, blanc 1 700-10 000 K. SL1 : strobe natif 0,1-25 Hz dans les profils compatibles. Le patch source à quatre canaux ne donne pas accès au canal strobe dédié : reconfiguration à valider avec le DT. Diffusion et accessoires réels à relever.
PAR 56 WFL 6 proposés	Intensité ; blanc ou noir (éteint).	500 W, fixes. Base blanche de la piste, graduable ; implantation S1-S6 proposée. Ampoule et photométrie non documentées. Disponibilité, gradateurs et accroche à confirmer.

Kit existant conservé. 106 et Zoom 5 restent en place. 9, 11, 13, 205, 206, M2 et Zoom 6 sont réactivés dans les huit ambiances. Orientations revues pour l'artiste au centre et la protection de l'écran au fond de scène. Les découpes restent blanches : aucune gélatine supposée.

SOURCES FABRICANT - CONSULTÉES LE 7 OCTOBRE 2026

Chauvet - Intimidator Spot 375Z IRC, manuel rev.6 (gobos p.7)

Chauvet - COLORado 1-Tri Tour, manuel v2 rev.4

ETC - Source Four et documentation Zoom

Rosco - DMG MINI / SL1 MIX, guide utilisateur

Rosco - DMX Profiles nov.2022 (quatre canaux p.3 ; strobe Full 8b p.10)

Le Ministère - Grand Remix

POUR VALIDATION DT

HUIT AMBIANCES SUGGÉRÉES

Pistes artistiques à faire évoluer selon les morceaux et les besoins du spectacle. Elles illustrent la direction souhaitée ; **conduite et patch à finaliser avec la direction technique.** Écran rond au fond de scène ; artiste dans l'axe central. Les pourcentages décrivent la simulation, et non une consigne physique ou DMX. À valider avec le DT.

Ambiance	Intention lumière	Brouillard F1 Pourcentage indicatif
01 Entrée du public	Salle blanche à pleine intensité ; mouvements très discrets. DJ en couleur. Appoint blanc modéré sur scène ; 112 OFF.	**OFF**
02 Ouverture	DJ magenta/violet. Artiste éclairé de face en blanc. Piste éteinte ; bar et appoints de scène maintenus.	**OFF**
03 Bleu océan	Bleu/cyan avec passages blancs et violets. Gobo 6 - Ondes, mouvements lents. Sur les lyres : cyan de la roue, pas de bleu profond.	**ON - 30 %**
04 Rouge intense	Fond rouge, gobo 7 - Anneaux, mouvements rapides. Accents blancs SL1 à 8 Hz ; réduction partielle des autres sources durant les accents.	**ON - 35 %**
05 Jaune et rouge	Jaune, rouge et orange, avec un léger appoint blanc des découpes réactivées. Gobo 2, mouvements souples et fondus.	**ON - 25 %**
06 Pinky love	Rose, magenta et violet ; gobos variés. Accents blancs des PAR et magenta de 111 jusqu'à 2 Hz. Artiste présent ; 112 OFF.	**ON - 35 %**
07 Transition DJ	Artiste absent. DJ orange/magenta/rouge. Faisceaux mobiles dans la salle, gobos variés et accents jusqu'à 2 Hz.	**ON - 35 %**
08 Finale hip-hop	Couleurs et gobos variés, mouvements rapides entre scène et public. Blanc réduit sur l'artiste ; accents de salle jusqu'à 2 Hz.	**ON - 35 %**

Focus : appoints blancs modérés des découpes ; LED dans la palette de chaque ambiance. Réglages et transitions proposés, à adapter aux morceaux et à vérifier sur la toile.

Le Ministère - Grand Remix


BROUILLARD ET VALIDATION EN SALLE

POUR VALIDATION DT

F1 - Antari F-1W de la salle

Position proposée **entre l'enceinte gauche et le poste DJ**, table reculée de 30 cm. Centre : **x -3,62 ; y +1,43 ; z +0,6096 m**.
Gabarit 60,8 x 27,5 x 28,6 cm indicatif ; encombrement réel à relever.

VUE DE DESSUS - COTES INDICATIVES

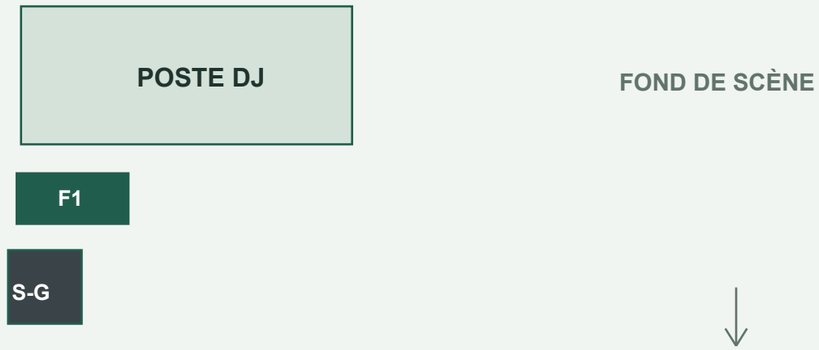

S-G : enceinte. F1 : dégagement / ventilation à confirmer.

Diffusion

Proposition : OFF à l'accueil et à l'ouverture. Débits suggérés p. 8. La valeur visuelle de la maquette n'est pas une consigne DMX ; réduire si la brume diminue le contraste.

Dégagements

Emplacement à valider. Le manuel F-1 prescrit au moins **50 cm libres autour** ; identifier le F-1W installé et confirmer ses consignes. Sortie, ventilation et accès dégagés. Manuel Antari F-1, p. 3 / 6.

À confirmer avant montage

P0 : projecteur au point du plan LX original. Support existant conservé. Confirmer la référence exacte de la courte focale, le cadrage et la netteté sur l'écran rond ; p. 4.

Écran E1 - construction proposée

Tissu blanc léger traité ignifuge, tendu sur un cerceau en PVC de ¾ **po**.

Circonférence communiquée : 20 pi (6,096 m). Diamètre calculé : **1,94 m**, à vérifier sur l'écran monté. Écran centré au fond de scène, à la place de l'écran existant ; hauteur à régler au cadrage.

Poids indicatif : 2,4 à 2,9 kg. Hypothèses : 20 pi de PVC ¾ po Schedule 40, tissu 100-180 g/m², assemblage inclus. À confirmer par pesée. Masse du tube : Charlotte Pipe, p. 28.

Principe d'attache confirmé par l'organisation : monofilament transparent (fil de pêche) vers le plafond. Points d'ancrage, caractéristiques du fil et sécurité secondaire à documenter avec le DT (p. 5).

Essai avant l'arrivée du public

1. Mire blanche puis noire : vérifier couverture et masque.
2. Allumer chaque appareil séparément : contrôler les deux faces de E1.
3. Tester les parcours complets, puis le brouillard et les reflets.
4. Vérifier visage de l'artiste, poste DJ, piste et éblouissement.

Validation finale du DT

Confirmer patch SL1, zéros et focus ; programmer la GrandMA3. Les images illustrent les intentions, sans certification photométrique. **Montage et essais physiques restent à valider en salle.**