

VUE PUBLIC : DJ À GAUCHE / ÉCRAN + VIDÉO À DROITE - TOP 1:65

8,53 m / 28 pi

3,66 m / 12 pi

Parterre 10,67 m / 35 pi

FOND DE SCÈNE

DJ FRÄNZE

SLAM

A - AVANT

B - MILIEU

C - FOND

RÉGIE

P1

VENTILATION

VENTILATION

1 2 3 4 5 6

S1 S2 S3 S4 S5 S6

251 252

101 102 103 104 105 106

201 202 203 204 205 206

207 208 209 210

111 112

M1 M2

P0

E1 Ø 1,50 m

KIT LX ET AJOUT PROPOSÉ

Kit du plan original conservé. Orange : Intimidator vers la piste. Gris : pointage proposé des 6 PAR 56 S1-S6, pris dans l'inventaire de la salle.

DJ À GAUCHE VUE PUBLIC

Table proposée 1,80 x 0,75 m. Centre : x = -2,00 ; y = +1,80. À mi-profondeur de scène.

ÉCRAN AU COIN AVANT DROIT

E1 : centre x = +3,52 ; y = 0,00. Plan de l'écran aligné sur le nez de scène ; bord droit aligné sur le bord de scène, x = +4,27. Ø environ 1,50 m.

ESSAI : VIDÉOPROJECTEUR AU FOND

P1 : repère optique x = +3,07 ; y = -9,50 ; z = +3,00 m. ET-DLE350 requise pour ce cadrage ; disponibilité non confirmée. Corps derrière le repère. Le plan A à l'avant reste l'implantation retenue.

LUMIÈRES DANS LA SALLE

6 PAR 56 S1-S6 proposés sur la barre salle à y = -4,25 m. S1/S6 vers A ; S3/S4 vers B ; S2/S5 vers C. Implantation et disponibilité à valider.

CADRAGE DU PLAN

Origine au centre du nez de scène. x positif à droite du public ; y positif vers le fond de scène. Dimensions nominales de la fiche.

0 1 2 m

LÉGENDE - APPAREILS DU MINISTÈRE

Symbole	Appareil	Qté	DMX
	ETC Source Four 36°	8*	1
	ETC Source Four 25/50 Zoom	6	1
	Colorado 1 Tour-Tri	12	ARC1 / 3
	Intimidator Spot 375Z	8	15
	DMG SL1 Mix 200 W	1	4**
	DMG Mini Mix 100 W	2	4**
	PAR 56 WFL 500 W	6*	1

* Source Four 36° : 8 inventoriés, 7 dessinés.
PAR 56 : S1-S6 = emplacements proposés, à valider.
** Modes repris du plan LX ; conserver le patch.

IMPLANTATION DEMANDÉE - REPÈRES

E1 : écran suspendu Ø 1,50 m au coin avant droit, sans recul devant le nez de scène. Bord droit à l'aplomb du bord de scène. Bas proposé +1,80 m, haut +3,30 m / sol salle.

P1 : essai à 9,50 m, calculé pour une ET-DLE350. Repère au plan de référence optique, pas au centre du corps. Lens shift, accroche, ventilation, câblage et protection du faisceau à valider. La salle ne confirme pas cette lentille.

Piste : 6 PAR 56 proposés dans la salle pour une base fixe graduable, complétée par les 8 Intimidator existants. Les PAR ne sont pas attestés libres ou déjà installés à ces positions.

CARTOUCHE ET BASE DU PLAN

DT : Rémi LeGresley - Le Ministère
Base : dossier Audio-LX fourni + plan LX 2023 envoyé par Rémi.
Statut : implantation et pointages proposés. Emplacements LX repris graphiquement ; conserver les points réels. Accroches E1/P1 à valider.

FRONT - VUE DEPUIS LE PUBLIC - 1:50

8 / 10 / 12

201

202 / 207

203 / 208

251

7

SL1

204 / 209

252

205 / 210

206

9 / 11 / 13

1

101

2

102

103

3

4

104

105

5

106

6

S1

S2

S3

S4

S5

M1

111

DJ FRÄNZE

E1

Ø 1,50 m

bas +1,80 m*

112

1,50 m

SLAM AU CENTRE

E1 au coin avant droit. * Hauteur proposée ; à régler avec l'optique, la visibilité et les accroches.

LÉGENDE - APPAREILS DU MINISTÈRE			
Symbole	Appareil	Qté	DMX
	ETC Source Four 36°	8*	1
	ETC Source Four 25/50 Zoom	6	1
	Colorado 1 Tour-Tri	12	ARC1 / 3
	Intimidator Spot 375Z	8	15
	DMG SL1 Mix 200 W	1	4**
	DMG Mini Mix 100 W	2	4**
	PAR 56 WFL 500 W	6*	1

LEFT - COUPE SUR E1, À DROITE VUE PUBLIC - 1:65

PLAN B : essai, pas une modification du plan A. Écran rond 1,50 m dans une image native 16:10 de 2,40 x 1,50 m. La formule Panasonic ET-DLE350 donne 8,63 à 13,12 m : le recul de 9,50 m est dans cette plage. Lentille non confirmée dans le kit de la salle.

Trajet schématique. Cercle décentré de 0,45 m à droite dans le raster pour tenir son bord au bord de scène. Axe raster x +3,07 m ; centre E1 x +3,52 m. Hauteur d'axe proposée +3,00 m. La couverture et le passage au-dessus du public ne sont pas validés par ce calcul de recul.


The diagram illustrates a stage layout with the following elements and dimensions:

- Stage (SCÈNE):** A rectangular area on the left. A dimension of 0,61 m is indicated for a specific section.
- Equipment on Stage:**
 - Three cameras labeled 104, 105, and 106 are positioned along the top edge.
 - A camera labeled 112 is positioned below the top edge.
 - A monitor labeled M2 is positioned below the top edge.
 - A screen labeled E1 is positioned at the back of the stage.
 - A camera labeled 6 is positioned to the right of the stage.
 - A camera labeled 252 is positioned further to the right.
- Audience Area (PUBLIC / DANSE):** An area on the right with three stick figures representing the audience.
- Camera and Screen:**
 - A camera labeled S1-S6 is positioned between the stage and the audience.
 - A dashed line indicates the camera's field of view towards the screen E1.
 - A label "P1 - ESSAI ARRIÈRE" is positioned to the right of the camera.
 - A label "S1-S6 : PAR salle proposés" is positioned below the camera.
- Dimensions and Labels:**
 - A horizontal dimension line indicates a "recul optique 9,50 m*" (optical setback of 9.50 m).
 - A vertical dimension line indicates a height of 0,61 m.

NOTES TECHNIQUES DE MONTAGE

1. Kit existant. Conserver les positions et le patch du plan LX original. Les PAR S1-S6 sont une proposition complémentaire avec du matériel inventorié, non une implantation existante confirmée.
2. Écran E1. Ø environ 1,50 m, suspendu au coin avant droit vue public. Plan de l'écran sur le nez de scène ($y = 0$) ; bord droit sur le bord de scène. Suspension et sécurité secondaire à définir par le DT.
3. Lumières dans la salle. Proposer S1-S6 sur la barre transversale existante, à 4,25 m du nez de scène. Vérifier place disponible, charge, accroches, gradateurs et disponibilité des PAR. Puissance totale : $6 \times 500 \text{ W} = 3 \text{ kW}$.
4. Projection. Essai PT-RZ770 + ET-DLE350 compatible, non confirmée disponible. Recul 9,50 m ; axe +3,00 m. Étudier support, réglage optique, ventilation, public et protection du faisceau. Le support avant documenté ne valide pas une accroche au fond.
5. Public dansant. PAR : base fixe graduable. Intimidator : effets complémentaires, pan/tilt limités autour d'E1. Régler l'éblouissement et la couverture au fond.
6. Accroches. Aucun appareil sur les rails à rideaux. Points approuvés par la salle uniquement. Le 8e Source Four 36° reste non localisé.

ISOMÉTRIE DE REPÉRAGE - SANS ÉCHELLE - IMPLANTATION PROPOSÉE

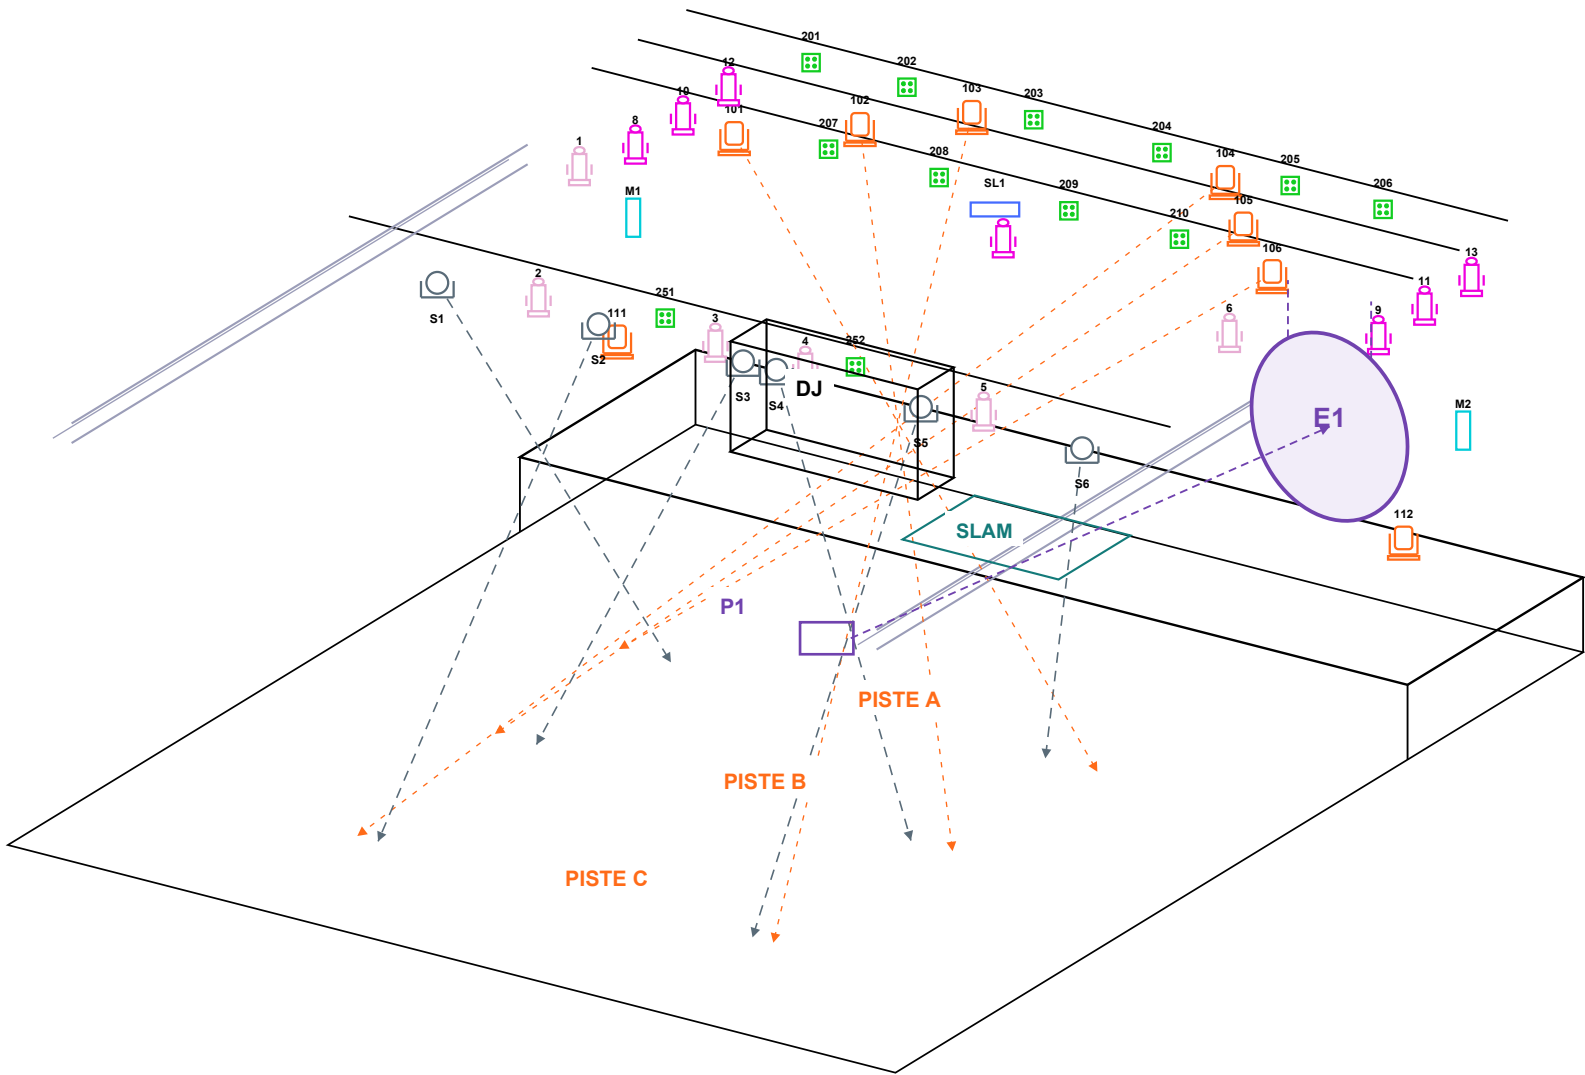

S1-S6 : 6 PAR proposés au-dessus de la piste. Les autres appareils conservent les positions du plan LX existant.

COTES À REPORTER ET RÉGLAGES POUR LE DT

Élément	Cote / destination	Application
E1 - écran	x +3,52 ; y 0,00 ; Ø 1,50 m	Coin avant droit : bord droit x +4,27. Bas proposé +1,80 m / sol salle.
P1 - vidéo	Repère optique x +3,07 ; y -9,50 ; z +3,00 m	Essai ET-DLE350 : 9,50 m. Cercle décentré +0,45 m dans le raster.
DJ / slam	DJ : x -2,00 ; y +1,80. Slam : x 0 ; y +1,10.	Table 1,80 x 0,75 m proposée ; passage central dégagé.
PAR S1-S6	y -4,25 ; x -3,10 / -1,55 / -0,16 / +0,16 / +1,55 / +3,10.	Hauteur de corps proposée +3,30 m. S1/S6 : A ; S3/S4 : B ; S2/S5 : C.

Sources : dossier Audio-LX du Ministère (dimensions, inventaire, support et installation vidéo) ; plan LX communiqué par Rémi ; spécifications Panasonic PT-RZ770. Les cotes du nouveau setup sont des propositions de conception, pas un relevé de l'existant.

ÉQUIPEMENTS TECHNIQUES LX - FICHE SALLE

Appareil	Qté	Donnée principale
Colorado 1 Tri Tour	12	LED RGB / ARC1
Intimidator Spot 375Z	8	6 suspendus + 2 bas
Source Four 25-50°	6	750 W / TL3
Source Four 36°	8	575 W / 7 dessinés
DMG SL1 Mix	1	200 W
DMG Mini Mix	2	100 W
PAR 56 WFL	6	500 W / S1-S6 proposés

Commande : GrandMA3 Command Wing Compact sur PC.
Gradateurs : 4 Lite-Putter DX-1210.
Distribution DMX : 1 Chauvet Data Stream 4.
Brouillard : Antari F-1W, usage à convenir.
Complément : conserver l'éclairage général de salle pour accueil et circulation.

VIDÉOPROJECTION - DONNÉES DOCUMENTÉES

Panasonic PT-RZ770
Laser DLP ; 7 000 lumens nominaux.
Résolution native : 1920 x 1200, 16:10.
HDMI disponible ; câble annoncé par Rémi.

Option arrière testée :
ET-DLE350 compatible ; plage calculée 8,63 à 13,12 m. Choix d'essai : 9,50 m. La lentille standard ne couvre ici que 4,15 à 5,82 m.

Écran de ce projet : cercle Ø 1,50 m. Prévoir un masque circulaire. Une image 16:10 de 1,50 m de haut mesure 2,40 m de large avant masque.

À confirmer : disponibilité ET-DLE350, référence de distance, accroche arrière et trajet du faisceau. Le dossier de salle décrit seulement une installation ultra-courte à 5 pi (1,52 m).

HYPOTHÈSES ET RÉSULTATS - PANASONIC PT-RZ770			POINTS À CONFIRMER AVEC LE DT
Base : cercle de diamètre 1,50 m inscrit dans une image native 16:10, sans agrandissement numérique du raster. Le masque circulaire est placé à droite dans l'image pour que le raster ne dépasse pas le bord droit de la scène. Hauteur image = 1,50 m ; largeur = 1,50 x 16 / 10 = 2,40 m. Diagonale = racine(2,40² + 1,50²) = 2,8302 m = 111,425 pouces.			1. Lentille Référence réellement montée et disponibilité d'une ET-DLE350. Le dossier nomme le projecteur, mais seulement une installation ultra-courte. 2. Montage au fond Repère de distance, support, charges, refroidissement, alimentation et HDMI / transport vidéo. 3. Public et faisceau La hauteur d'axe +3,00 m est une hypothèse. Régler le lens shift ; vérifier ombres, ventilation, visibilité et prescriptions Panasonic de protection du faisceau avec l'optique longue. 4. Écran Ø 1,50 m, au coin avant droit. Suspension et hauteur à confirmer. Aucun déplacement supplémentaire à droite sans dépasser le bord du modèle. 5. Comparaison A : projecteur à l'avant, repère 1,85 m non validé optiquement. B : essai arrière à 9,50 m, ET-DLE350 requise, non confirmée disponible.
Optique compatible	Formule Panasonic (m)	Plage calculée	
Standard / ET-DLE170	D x 0,0379 - 0,0746 / D x 0,0529 - 0,0725	4,15 à 5,82 m	
ET-DLE250	D x 0,0500 - 0,0800 / D x 0,0789 - 0,0792	5,49 à 8,71 m	
ET-DLE350	D x 0,0787 - 0,1351 / D x 0,1190 - 0,1346	8,63 à 13,12 m	
Essai à 9,50 m : rapport distance / largeur = 9,50 / 2,40 = 3,96:1. La formule spécifique PT-RZ770 / ET-DLE350 confirme que cette distance entre dans sa plage. Les équations du fabricant sont approximatives et demandent un réglage sur place. Espace longitudinal : parterre de 10,668 m ; le repère optique à 9,50 m laisse 1,168 m jusqu'au fond de salle pour le corps, le support et les dégagements. Ce solde n'est pas une garantie d'installation. Position latérale : centre du cercle x +3,5172 m ; bord droit x +4,2672 m. Raster centré x +3,0672 m, cercle décalé à droite de 0,45 m. En 1920 x 1200 : centre du masque (1320, 600), rayon 600 pixels. Position de départ à tester. Conclusion : faisabilité de recul confirmée par calcul avec une ET-DLE350. Faisabilité de l'installation et disponibilité de cette lentille non confirmées. Le plan A à l'avant reste l'implantation en cours.			Sources : fiche Audio-LX Le Ministère ; Panasonic PT-RZ770 Spec File, page 15, formules 16:10 ; page 16, plage de décentrement. Calcul réalisé le 7 octobre 2026.