


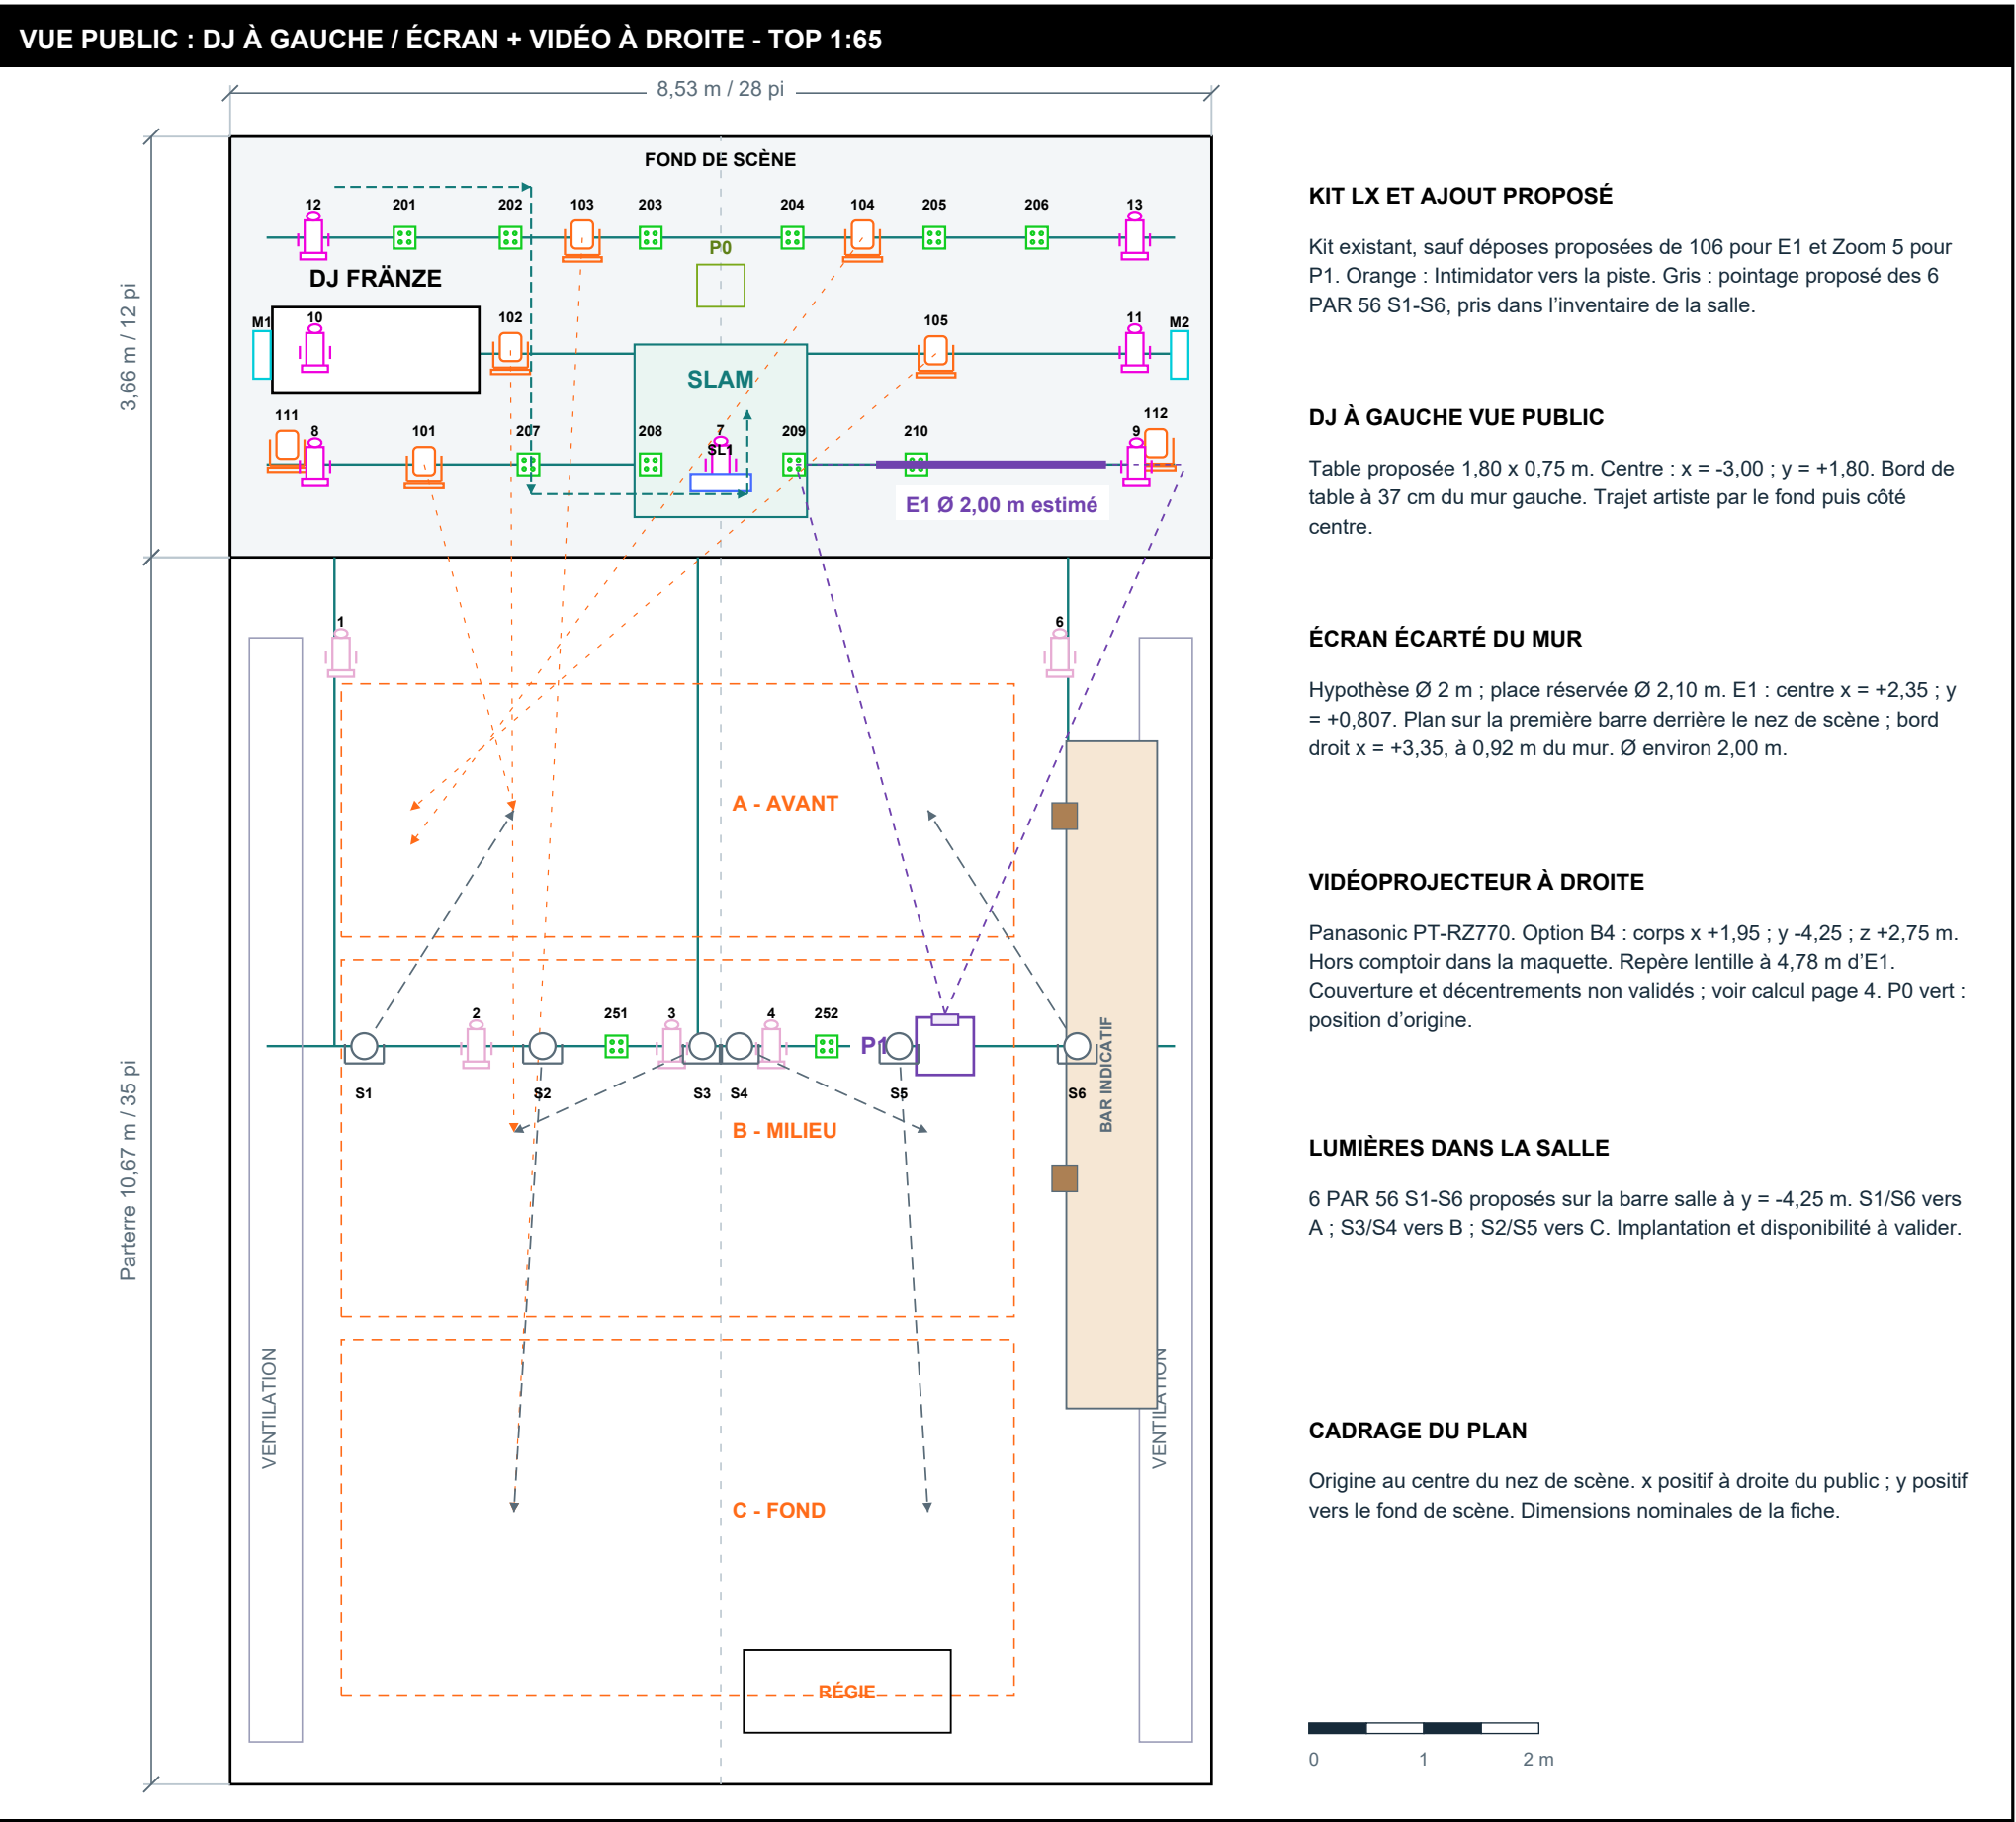

LÉGENDE - APPAREILS DU MINISTÈRE

| Symbole                                                                             | Appareil                   | Qté | DMX      |
|-------------------------------------------------------------------------------------|----------------------------|-----|----------|
|  | ETC Source Four 36°        | 8*  | 1        |
|  | ETC Source Four 25/50 Zoom | 6   | 1        |
|  | Colorado 1 Tour-Tri        | 12  | ARC1 / 3 |
|  | Intimidator Spot 375Z      | 8   | 15       |
|  | DMG SL1 Mix 200 W          | 1   | 4**      |
|  | DMG Mini Mix 100 W         | 2   | 4**      |
|  | PAR 56 WFL 500 W           | 6*  | 1        |

\* Source Four 36° : 8 inventoriés, 7 dessinés.

PAR 56 : S1-S6 = emplacements proposés, à valider.

\*\* Modes repris du plan LX ; conserver le patch.

IMPLANTATION DEMANDÉE - REPÈRES

E1 : écran suspendu Ø 2,00 m estimé à l'avant droit, sur la première barre, à 0,807 m derrière le nez de scène. Bord droit à 0,92 m du mur droit. Bas proposé +1,05 m, haut +3,05 m / sol salle.

P1 : option B4 x +1,95 ; y -4,25 ; z +2,75 m. Enveloppe indicative de 0,50 x 0,50 m, à 0,805 m du bord du comptoir modélisé. Lentille indicative à 4,78 m de l'écran. Lentille réelle, décentrement et accroche non validés.

Piste : 6 PAR 56 proposés dans la salle pour une base fixe graduable, complétée par 6 Intimidator pendant la vidéo (112 éteint, 106 déposé proposé). Les PAR ne sont pas attestés libres ou déjà installés à ces positions.


CARTOUCHE ET BASE DU PLAN

DT : Rémi LeGresley - Le Ministère

Base : dossier Audio-LX fourni + plan LX 2023 envoyé par Rémi.

Statut : implantation et pointages proposés. Emplacements LX repris graphiquement ; 106 et Zoom 5 déposés proposés. Accroches E1/P1 à valider.

FRONT - VUE DEPUIS LE PUBLIC - 1:50

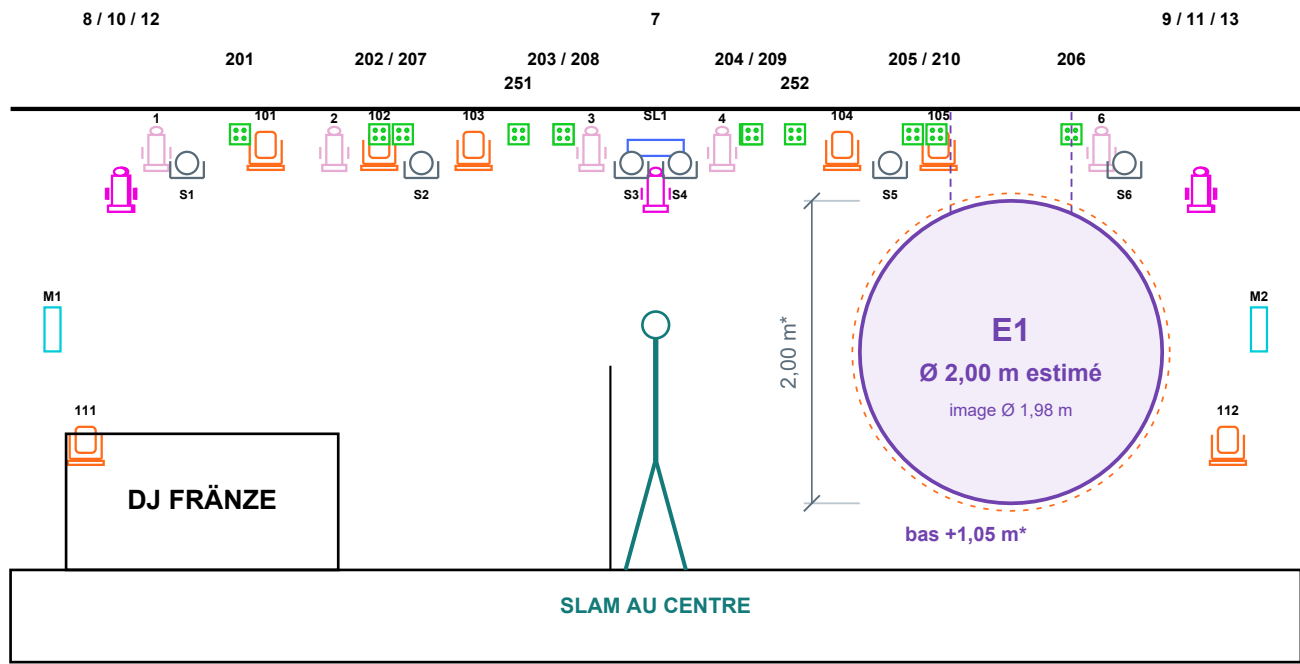


E1 écarté du mur droit. \* Hauteur proposée ; à régler avec l'optique, la visibilité et les accroches.

LEFT - COUPE SUR E1, À DROITE VUE PUBLIC - 1:65

P1 est une proposition de repositionnement. La fiche décrit l'installation existante à 5 pi (1,52 m) de son écran 150 pouces. Dans V17 : corps à 4,25 m devant le nez de scène, repère de lentille indicatif à 4,78 m. La lentille de la salle est inconnue : essai spatial, non validé optiquement.

Trajet vidéo schématique : la lentille ultra-courte peut imposer un décalage et un trajet différents. B4 est repérée sur le plan source. Adaptation du Chief VCMU au tube carré, hauteur, charge et lentille à confirmer.

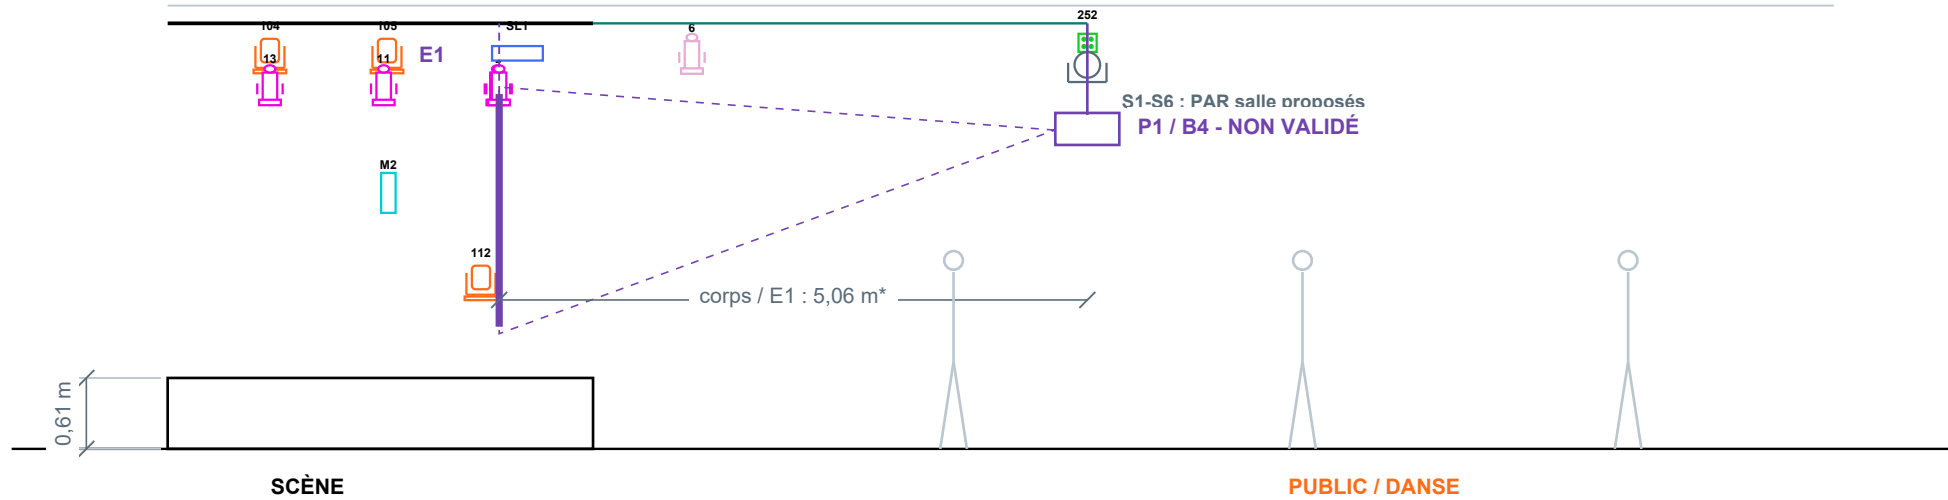

LÉGENDE - APPAREILS DU MINISTÈRE


| Symbole | Appareil                   | Qté | DMX      |
|---------|----------------------------|-----|----------|
|         | ETC Source Four 36°        | 8*  | 1        |
|         | ETC Source Four 25/50 Zoom | 6   | 1        |
|         | Colorado 1 Tour-Tri        | 12  | ARC1 / 3 |
|         | Intimidator Spot 375Z      | 8   | 15       |
|         | DMG SL1 Mix 200 W          | 1   | 4**      |
|         | DMG Mini Mix 100 W         | 2   | 4**      |
|         | PAR 56 WFL 500 W           | 6*  | 1        |

\* Source Four 36° : 8 inventoriés, 7 dessinés.  
PAR 56 : S1-S6 = emplacements proposés, à valider.  
\*\* Modes repris du plan LX ; conserver le patch.

NOTES TECHNIQUES DE MONTAGE

- Kit existant. Conserver les positions et le patch, sauf déposes proposées de 106 pour E1 et du Zoom 5 pour P1. Les PAR S1-S6 sont une proposition complémentaire avec du matériel inventorié, non une implantation existante confirmée.
- Écran E1. Ø environ 2,00 m, suspendu à l'avant droit, écarté du mur vue public. Plan de l'écran sur la première barre (y = +0,807) ; bord droit à 0,92 m du mur. Suspension et sécurité secondaire à définir par le DT.
- Lumières dans la salle. Proposer S1-S6 sur la barre transversale existante, à 4,25 m du nez de scène. Vérifier place disponible, charge, accroches, gradateurs et disponibilité des PAR. Puissance totale : 6 x 500 W = 3 kW.
- Projection. PT-RZ770 et Chief VCMU documentés. Lentille installée non nommée : ne pas appliquer le ratio du zoom standard à l'installation ultra-courte. P1 hors du bar modélisé. Repère lentille à 4,78 m de l'écran, option sur B4 compatible en recul avec ET-DLE150 ; disponibilité et décentrement à vérifier. Lentille de la salle inconnue.
- Public dansant. PAR : base fixe graduable. Intimidator : effets complémentaires, lyres fixes pendant la vidéo ; transit avec dimmer fermé. Régler l'éblouissement et la couverture au fond.
- Accroches. Aucun appareil sur les rails à rideaux. Points approuvés par la salle uniquement. Le 8e Source Four 36° reste non localisé.

ISOMÉTRIE DE REPÉRAGE - SANS ÉCHELLE - IMPLANTATION PROPOSÉE

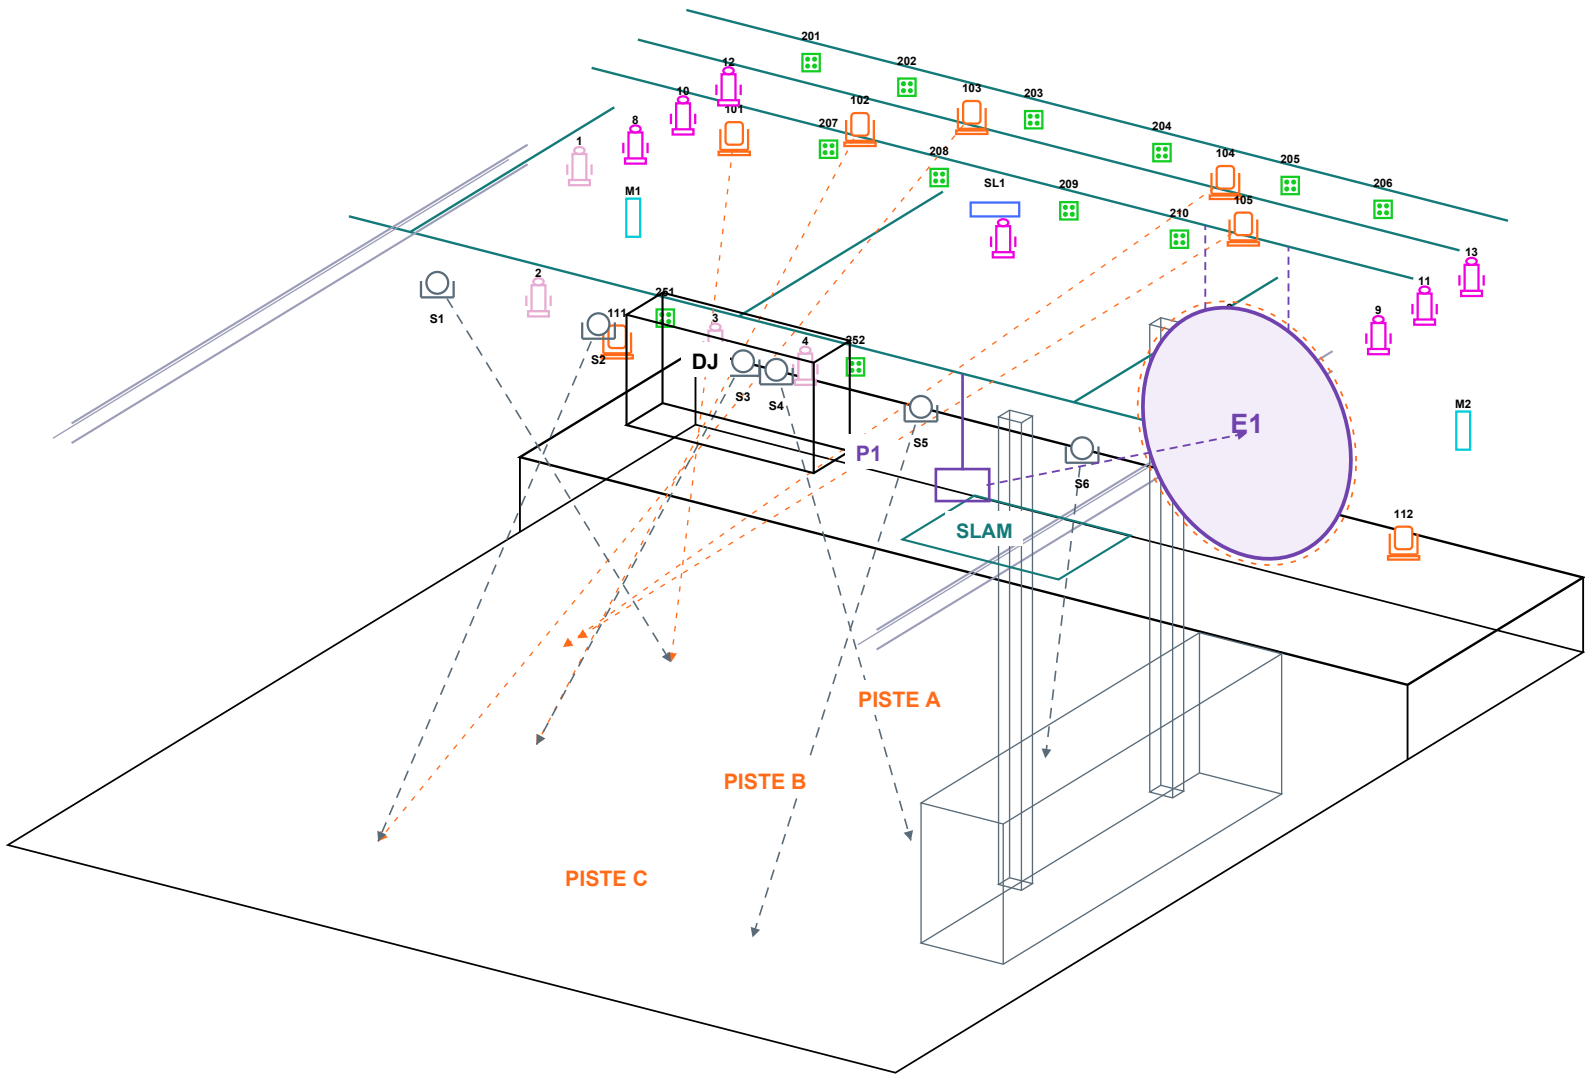

S1-S6 : 6 PAR proposés au-dessus de la piste. 106 et Zoom 5 : déposes proposées pour E1/P1 ; autres points conservés.

COTES À REPORTER ET RÉGLAGES POUR LE DT

| Élément    | Cote / destination                                         | Application                                                                                     |
|------------|------------------------------------------------------------|-------------------------------------------------------------------------------------------------|
| E1 - écran | x +2,35 ; y +0,807 ; Ø 2,00 m estimé                       | Bord droit x +3,35 ; mur à 0,92 m. Bas proposé +1,05 m / sol salle.                             |
| P1 - vidéo | x +1,95 ; y -4,25 ; z +2,75 m                              | Hors comptoir modélisé. Repère lentille à 4,78 m. Optique, décentrement et support non validés. |
| DJ / slam  | DJ : x -3,00 ; y +1,80. Slam : x 0 ; y +1,10.              | Table 1,80 x 0,75 m ; mur gauche à 37 cm. Passage artiste derrière puis côté centre.            |
| PAR S1-S6  | y -4,25 ; x -3,10 / -1,55 / -0,16 / +0,16 / +1,55 / +3,10. | Hauteur de corps proposée +3,30 m. S1/S6 : A ; S3/S4 : B ; S2/S5 : C.                           |

Sources : dossier Audio-LX du Ministère (dimensions, inventaire, support et installation vidéo) ; plan LX communiqué par Rémi ; spécifications Panasonic PT-RZ770. Les cotes du nouveau setup sont des propositions de conception, pas un relevé de l'existant.

ÉQUIPEMENTS TECHNIQUES LX - FICHE SALLE

| Appareil              | Qté | Donnée principale                |
|-----------------------|-----|----------------------------------|
| Colorado 1 Tri Tour   | 12  | LED RGB / ARC1                   |
| Intimidator Spot 375Z | 8   | 5 suspendus + 2 bas ; 106 déposé |
| Source Four 25-50°    | 6   | 5 actifs ; Zoom 5 déposé proposé |
| Source Four 36°       | 8   | 575 W / 7 dessinés               |
| DMG SL1 Mix           | 1   | 200 W                            |
| DMG Mini Mix          | 2   | 100 W                            |
| PAR 56 WFL            | 6   | 500 W / S1-S6 proposés           |

Commande : GrandMA3 Command Wing Compact sur PC.  
Gradateurs : 4 Lite-Putter DX-1210.  
Distribution DMX : 1 Chauvet Data Stream 4.  
Brouillard : Antari F-1W, usage à convenir.  
Complément : conserver l'éclairage général de salle pour accueil et circulation.

VIDÉOPROJECTION - DONNÉES DOCUMENTÉES

Panasonic PT-RZ770  
Laser DLP ; 7 000 lumens nominaux.  
Résolution native : 1920 x 1200, 16:10.  
HDMI disponible ; câble annoncé par Rémi.


Installation décrite par la salle :  
Support Chief VCMU ; ultra short throw ; à 5 pi (1,52 m) de l'écran existant 16:9 de 150 pouces.

Écran de ce projet : cercle Ø 2,00 m estimé. Prévoir un masque circulaire. Gabarit V17 : 3,392 x 2,12 m avant masque, image visible Ø 1,98 m, bord noir intérieur de 1 cm. Réserve native pour réglage du masque.

À relever : référence de lentille et repère exact des 5 pi. Le modèle est connu ; le ratio de l'optique installée n'est pas fourni.

| DONNÉES COMMUNES - V17 - ESSAI SPATIAL, PAS UN PLAN DE MONTAGE VALIDÉ   |                                             |                                                                   |
|---|---------------------------------------------|-------------------------------------------------------------------|
| B4 reste un essai non retenu avec la lentille actuelle ; reprendre le point vidéo avec le DT. Le PDF et la maquette lisent le même fichier implantation.json : positions E1/P1/DJ, dimensions principales, trajet artiste, bar, poteaux et 40 appareils actifs ; 106 et Zoom 5 déposés proposés. Le repère de géométrie est identique dans les deux livrables. Cette concordance ne remplace pas un relevé architectural. |                                             |                                                                   |
|   |                                             |                                                                   |
|   |                                             |                                                                   |
| Élément   | Repères communs en mètres                   | Niveau de validation                                              |
| Scène / parterre   | 8,5344 x 3,6576 ; parterre 8,5344 x 10,668  | Dimensions nominales du dossier de salle                          |
| Écran E1   | x 2.35 ; y 0.81 ; z 2.05 ; diamètre 2.00    | Proposé : suspension et visibilité à valider                      |
| Projecteur P1   | x 1.95 ; y -4.25 ; z 2.75                   | Option B4 ; lentille installée et adaptation support non validées |
| DJ   | x -3.00 ; y 1.80 ; table 1,80 x 0,75        | Proposé ; dégagement mur 0,367 m                                  |
| Bar / poteaux   | Mêmes volumes indicatifs dans les deux vues | Aucun relevé coté disponible ; collisions réelles non garanties   |
| Lumières   | 34 existants actifs + 6 PAR proposés = 40   | Positions reprises graphiquement ; accroches réelles à conserver  |

| CALCUL DE COUVERTURE - IDENTIFIER LA LENTILLE AVANT DE FIXER LE REcul   |
|---|
| Dimension estimée : Ø 2,00 m non mesuré ; réserve d'encombrement Ø 2,10 m. Depuis V16 : E1 seul décalé de 0,40 m vers la droite ; recul et hauteur conservés. P1 reste provisoire.<br>Image demandée : cercle Ø 2,00 m estimé ; image visible Ø 1,98 m, bord noir de 1 cm. Gabarit natif 16:10 = 3,392 x 2,12 m, diagonale 157.481 pouces. Réserve optique de 2,12 m en hauteur ; masque à ajuster au diamètre réel, jusque 2,10 m. Le gabarit doit être noir hors du cercle.                       |
| Option B4 : corps P1 x +1,95 ; y -4,25 ; z +2,75 m. Écran x +2,35 ; y +0,807 ; z +2,05 m. Lentille indicative avancée de 0,28 m : L = 4,25 - 0,28 + 0,807 = 4,777 m. Décentrement horizontal : 0,40 m non validé ; écart vertical : 2,75 - 0,01 - 2,05 = 0,69 m.   |
| Zoom standard / ET-DLE170 : plage de recul 5.894 à 8.258 m, d'après les formules constructeur. Recul insuffisant à B4 pour ce gabarit avec réserve.<br>ET-DLE150 : plage 4.450 à 6.454 m : 4,777 m est dans la plage. Décentrement vertical et repère réel à contrôler.<br>ET-DLE085 : plage 2.693 à 3.357 m ; ne convient pas à ce recul et à ce gabarit.   |
| Conclusion conditionnelle : la position B4 est une option avec une optique appropriée, pas une installation confirmée avec la lentille actuelle. La salle décrit un montage ultra-court sans identifier sa lentille. Référence et disponibilité de l'optique indispensables avant de retenir B4.   |
| Accroche : barre transversale reprise graphiquement ; cotes non relevées. Chief VCMU inventorié, mais adaptation, charge et longueur de suspension non documentées. Zoom 5 réservé à la dépose pour P1 ; 106 pour E1. Le dessin ne certifie ni leur déplacement ni la capacité de la structure. Corps à 0,805 m du comptoir indicatif ; ancien gabarit à environ 0,015 m du comptoir en plan : marge insuffisante, point vidéo à reprendre ; visibilité, ventilation et obstacles réels à vérifier. |
| Source : Panasonic PT-RZ770 Spec File, pages 15–16 ; plan LX et fiche Audio-LX du Ministère. Les rayons sont un gabarit cible, pas une simulation de la lentille installée.   |

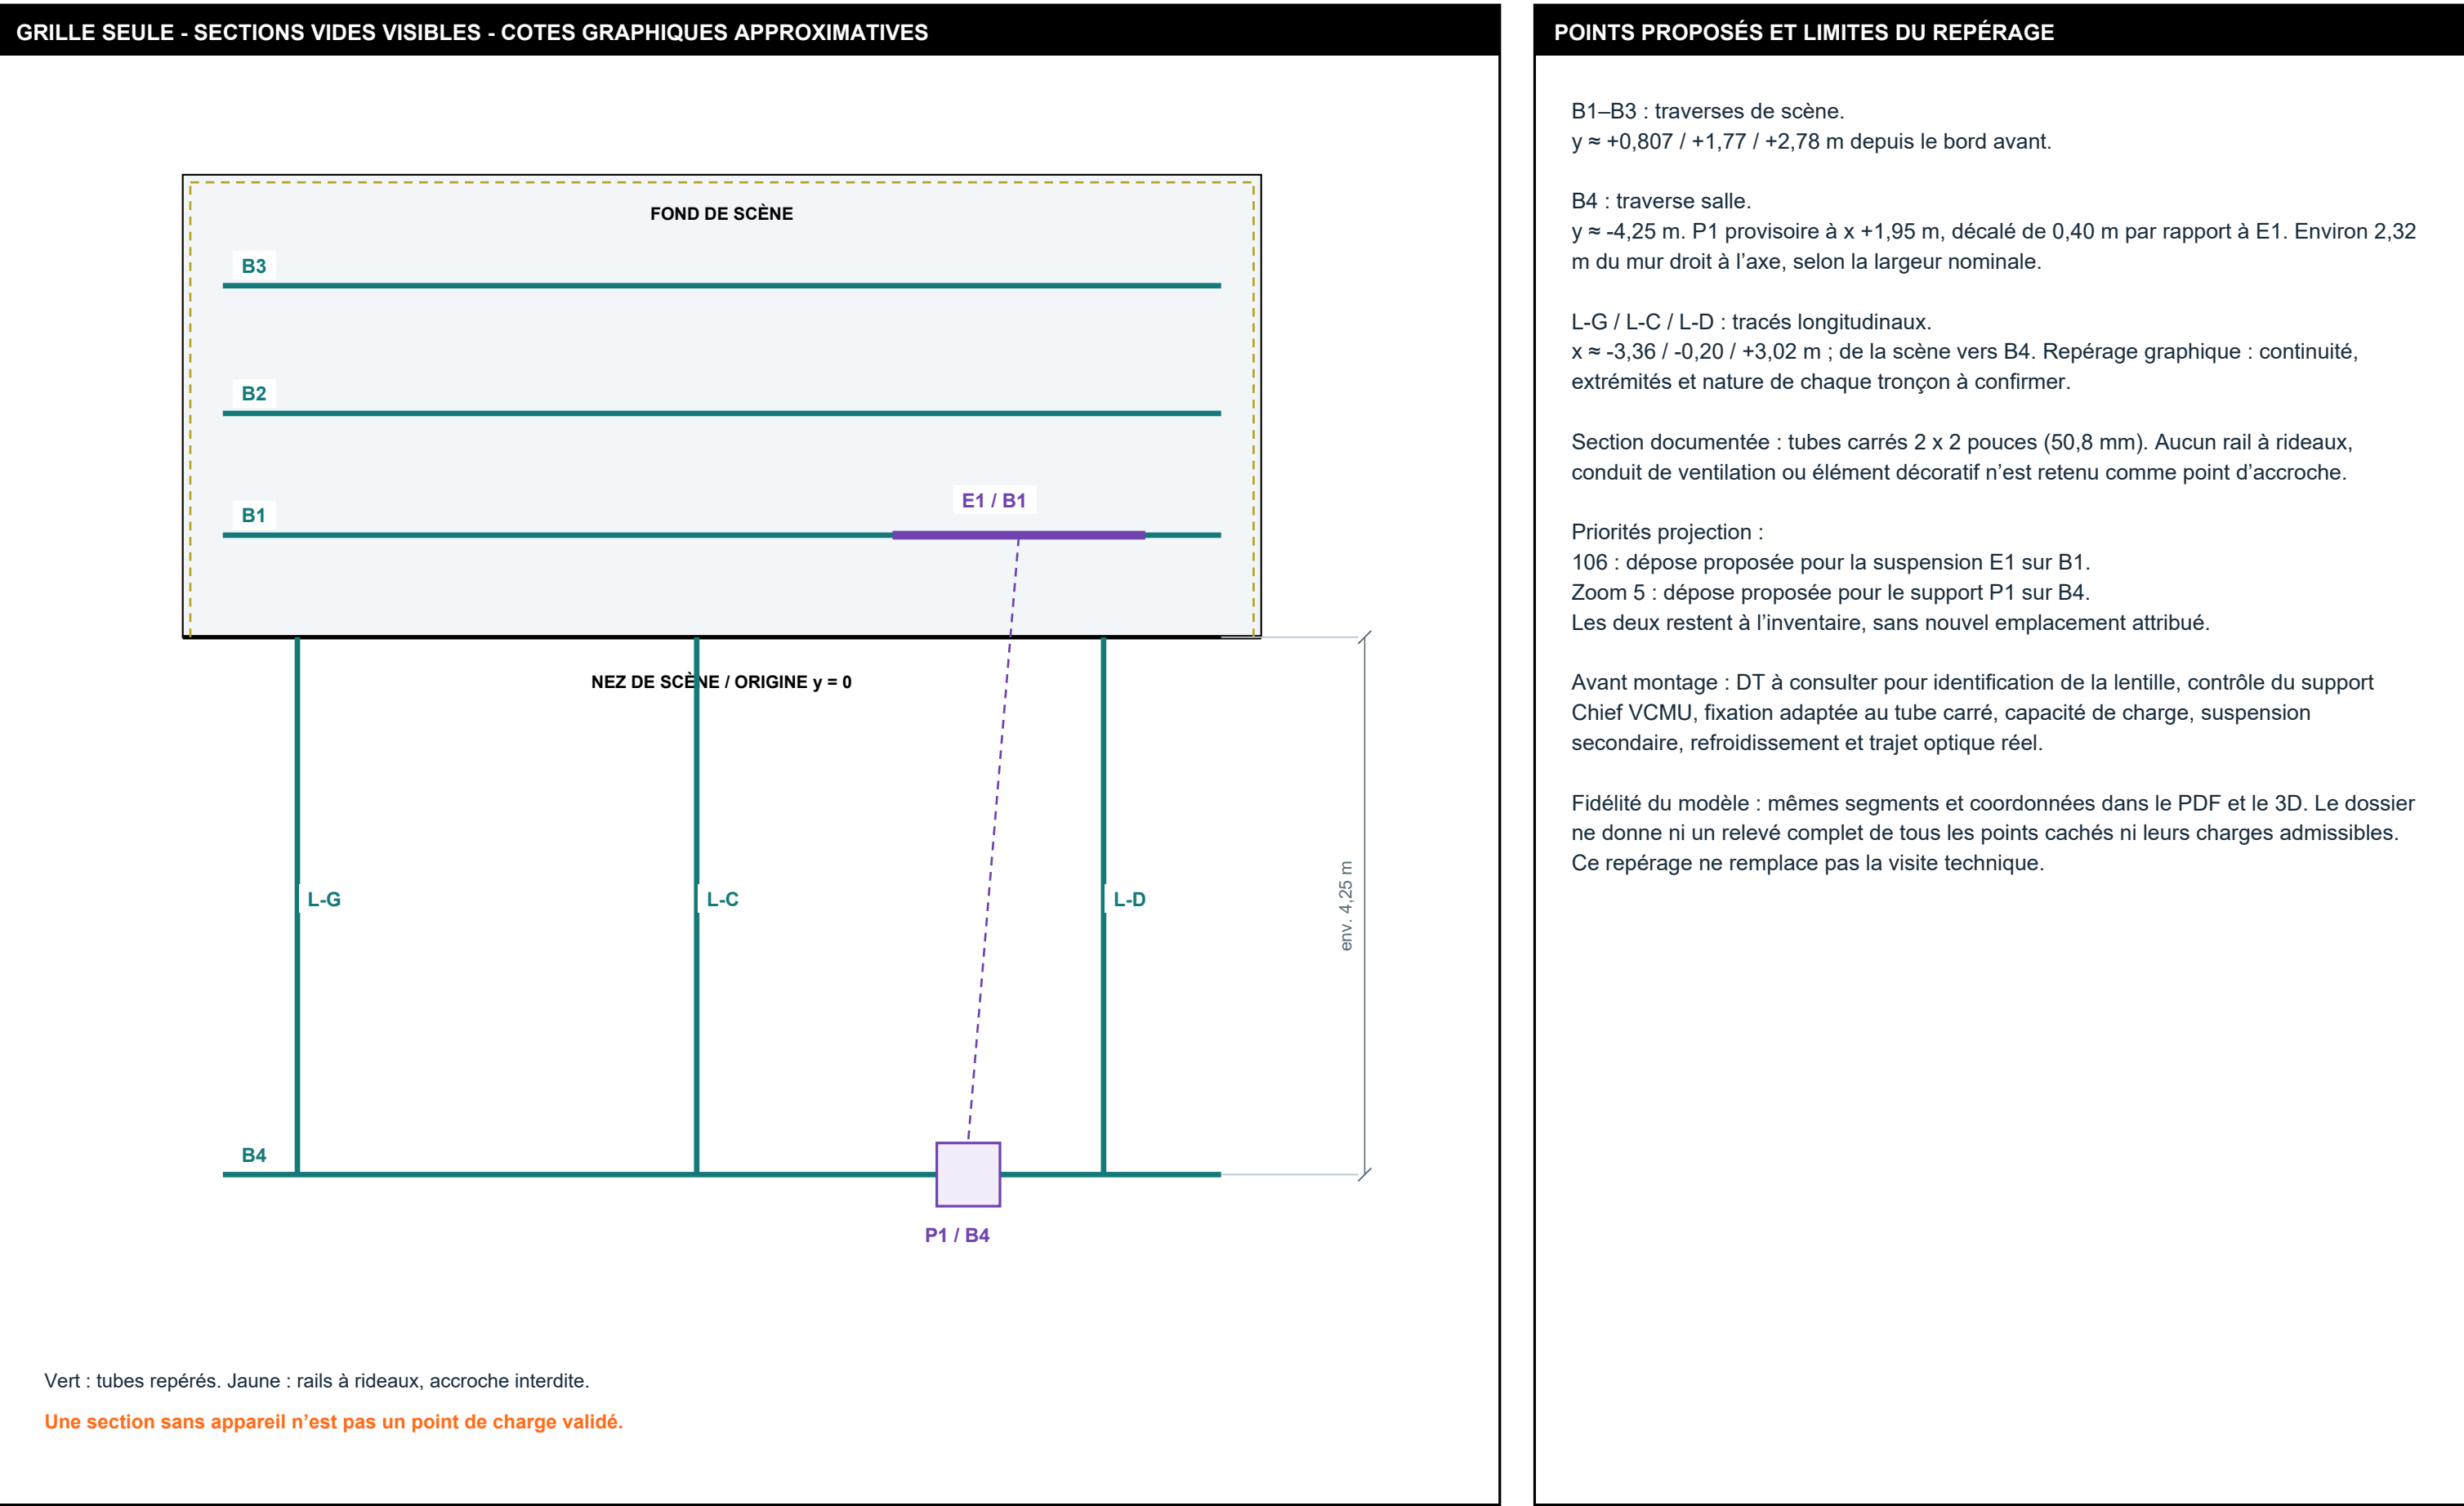

| ORIENTATIONS PARTAGÉES AVEC LE 3D - VIDÉO ACTIVE   |                 |              |               |
|---|-----------------|--------------|---------------|
| Appareils   | Destination     | Slam + vidéo | Danse + vidéo |
| 101, 102, 103, 104, 105, 111   | ARTISTE / PISTE | ALLUMÉ       | ALLUMÉ        |
| 112   | ARTISTE / PISTE | ÉTEINT       | ÉTEINT        |
| 7, 203, 204, 205, 208, 209, 251, 252, 2, 3, 4, SL1   | ARTISTE         | ALLUMÉ       | ALLUMÉ        |
| 8, 10, 12, 201, 202, 207, 1, M1   | DJ              | ALLUMÉ       | ALLUMÉ        |
| 9, 11, 13, 206, 210, 6, M2   | ARTISTE         | ÉTEINT       | ÉTEINT        |
| S1, S2, S3, S4, S5, S6   | PISTE           | ALLUMÉ       | ALLUMÉ        |
| Cibles au sol : artiste x 0 / y +1,10 ; DJ x -3,00 / y +1,80. Piste : voir flèches du plan. Allumé = état proposé après réglage du focus. Éteint = faisceau non retenu pendant la vidéo, sans dépose physique. Source Four : utiliser les couteaux pour couper les débordements ; Zoom : resserrer si nécessaire. Ne pas confondre ces coupures avec les déposes proposées de 106 et 5. Les niveaux précis restent à programmer en salle. |                 |              |               |

| CONSIGNES POUR LE FOCUS ET LA PROGRAMMATION   |
|---|
| 1. Lumières derrière E1. Orienter vers le centre artiste ou le DJ, en évitant aussi le dos de la toile. Aucun éclairage direct sur l'une ou l'autre face du cercle.   |
| 2. Appareils à risque. Les états ci-contre coupent les faisceaux dont le volume illustratif s'approche trop de l'écran. Une rotation ne garantit pas l'absence de débordement : contrôler les contours et la diffusion réelle.                                                                                          |
| 3. Lyres. Positions de focus fixes tant que la projection est active. Retirer les mouvements automatiques dans cet état. Transitions avec dimmer fermé ; réouverture au point vérifié. Aucune valeur pan/tilt DMX inventée.                                                                                             |
| 4. Zone protégée. Contrôle conservateur autour d'une sphère de rayon 1,20 m centrée sur E1 : réserve écran Ø 2,10 m plus 15 cm. Les rayons de faisceau sont des gabarits de conception, pas des mesures photométriques.                                                                                                 |
| 5. Trajet vidéo. Garder appareils, câbles et accessoires hors du faisceau vidéo réel. Les appareils derrière la toile ne bloquent pas une projection frontale si aucun élément ne dépasse devant elle ; ils peuvent néanmoins éclairer son dos. Recontrôler après identification de la lentille et du nouveau point P1. |
| 6. Validation réelle. Tester une mire blanche puis noire avec chaque appareil séparément, de face et derrière la toile. Corriger couteaux, zoom et orientation ; laisser éteint tout appareil qui lave l'image. Vérifier aussi les reflets et le brouillard.                                                            |
| Portée : consignes et maquette mises à jour ; aucun réglage de la GrandMA3 ni déplacement réel exécuté.   |