

VUE PUBLIC : DJ À GAUCHE / ÉCRAN + VIDÉO À DROITE - TOP 1:65

8,53 m / 28 pi

3,66 m / 12 pi

FOND DE SCÈNE

DJ FRÄNZE

SLAM

A - AVANT

B - MILIEU

C - FOND

RÉGIE

VENTILATION

VENTILATION

0 1 2 m

KIT LX FIXE

Conserver les accroches et les numéros existants. Les flèches orange montrent les directions proposées vers la piste.

DJ À GAUCHE VUE PUBLIC

Table proposée 1,80 x 0,75 m. Centre : x = -2,00 ; y = +1,80. À mi-profondeur de scène.

ÉCRAN À DROITE VUE PUBLIC

E1 : centre x = +2,15 ; y = -0,30. Écran suspendu devant le nez de scène. Ø environ 1,50 m.

VIDÉOPROJECTEUR À DROITE

Panasonic PT-RZ770. Repère proposé x = +2,15 ; y = -2,15. Recul cible 1,85 m, marge incluse, à valider optiquement. P0 vert : position d'origine.

PUBLIC DANSANT

101 + 106 vers A ; 102 + 105 vers B ; 103 + 104 vers C : affectation de départ, à ajuster au focus.

CADRAGE DU PLAN

Origine au centre du nez de scène. x positif à droite du public ; y positif vers le fond de scène. Dimensions nominales de la fiche.

LÉGENDE - APPAREILS DU MINISTÈRE			
Symbole	Appareil	Qté	DMX
	ETC Source Four 36°	8*	1
	ETC Source Four 25/50 Zoom	6	1
	Colorado 1 Tour-Tri	12	ARC1 / 3
	Intimidator Spot 375Z	8	15
	DMG SL1 Mix 200 W	1	4**
	DMG Mini Mix 100 W	2	4**
	PAR 56 WFL 500 W	6*	1

IMPLANTATION DEMANDÉE - REPÈRES

E1 : écran rond suspendu Ø 1,50 m. Bas proposé +1,80 m, haut +3,30 m / sol salle.

P1 : recul cible 1,85 m, soit +0,33 m par rapport au recul de la fiche. Marge souhaitée de +0,30 à +0,50 m, soumise à l'optique et au support.


Lumières public : les 8 Intimidator sont existants. Les 6 suspendus forment la base ; 111/112 complètent si leurs angles conviennent.

CARTOUCHE ET BASE DU PLAN

DT : Rémi LeGresley - Le Ministère

Base : dossier Audio-LX fourni + plan LX 2023 envoyé par Rémi.


Statut : implantation et pointages proposés. Emplacements LX repris graphiquement ;
conserver les points réels. Accroches E1/P1 à valider.

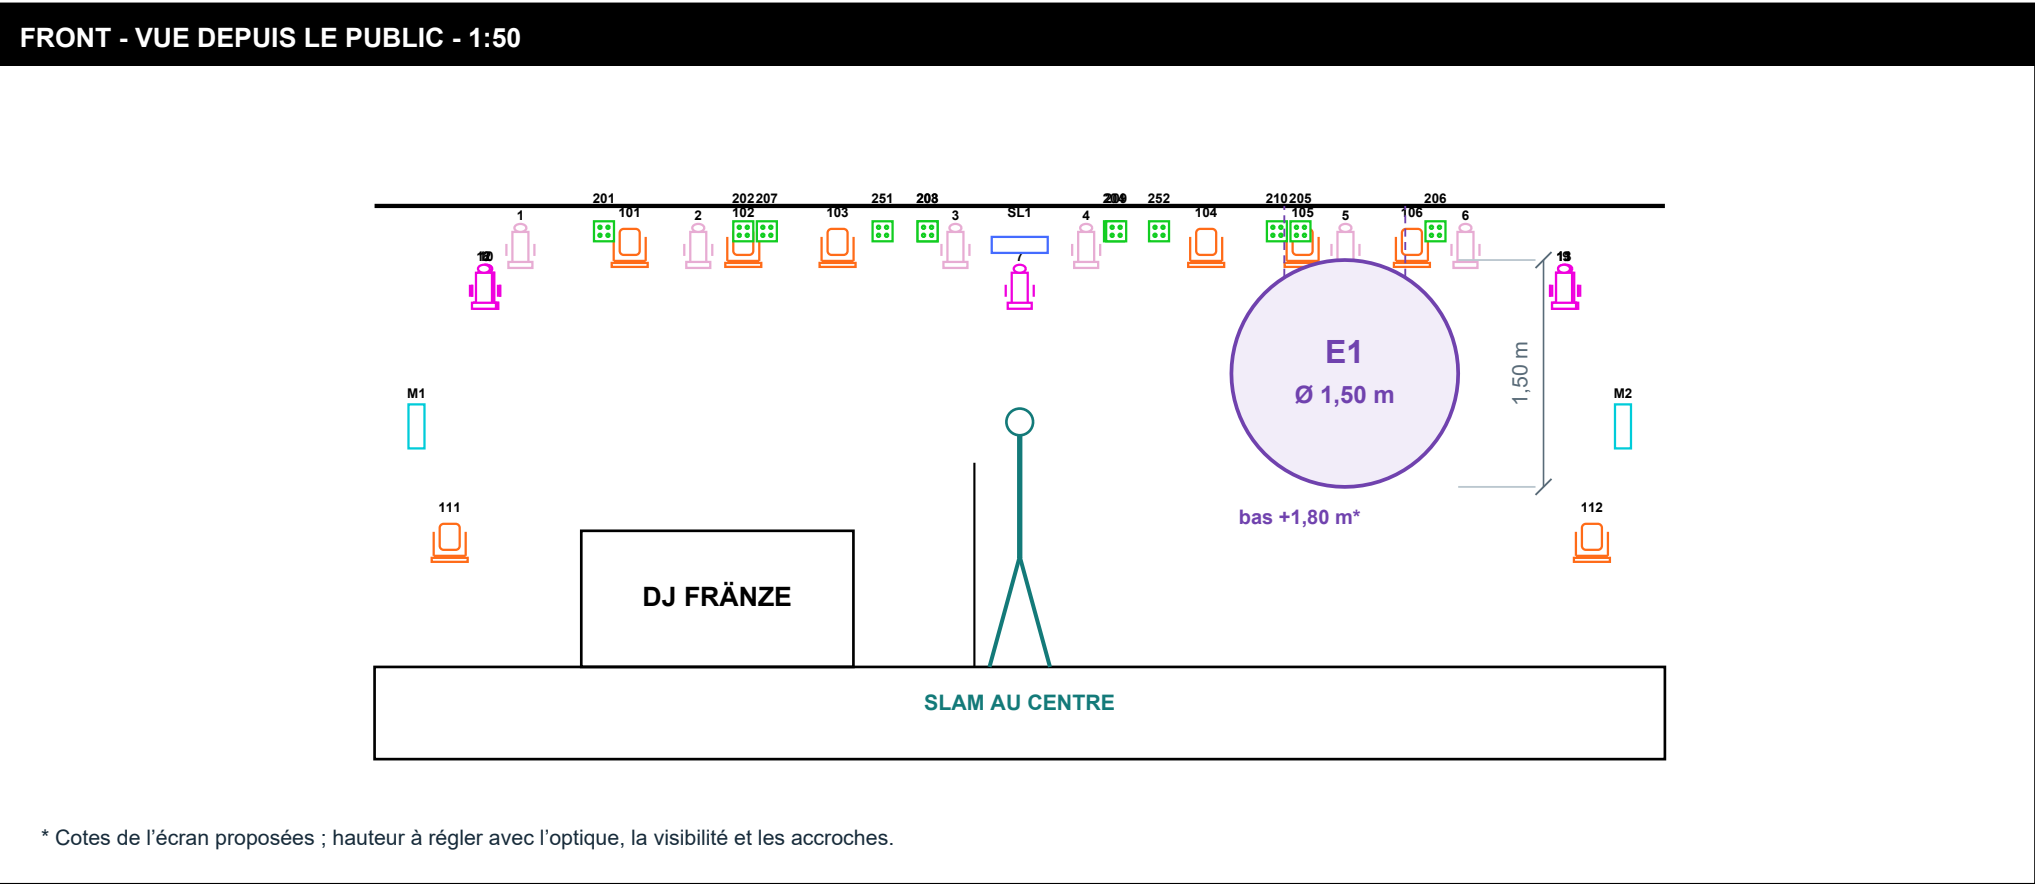

LÉGENDE - APPAREILS DU MINISTÈRE


Symbole	Appareil	Qté	DMX
	ETC Source Four 36°	8*	1
	ETC Source Four 25/50 Zoom	6	1
	Colorado 1 Tour-Tri	12	ARC1 / 3
	Intimidator Spot 375Z	8	15
	DMG SL1 Mix 200 W	1	4**
	DMG Mini Mix 100 W	2	4**
	PAR 56 WFL 500 W	6*	1

* Source Four 36° : 8 inventoriés, 7 dessinés.
Le 8e Source Four et les 6 PAR 56 sont non localisés.
** Modes repris du plan LX ; conserver le patch.

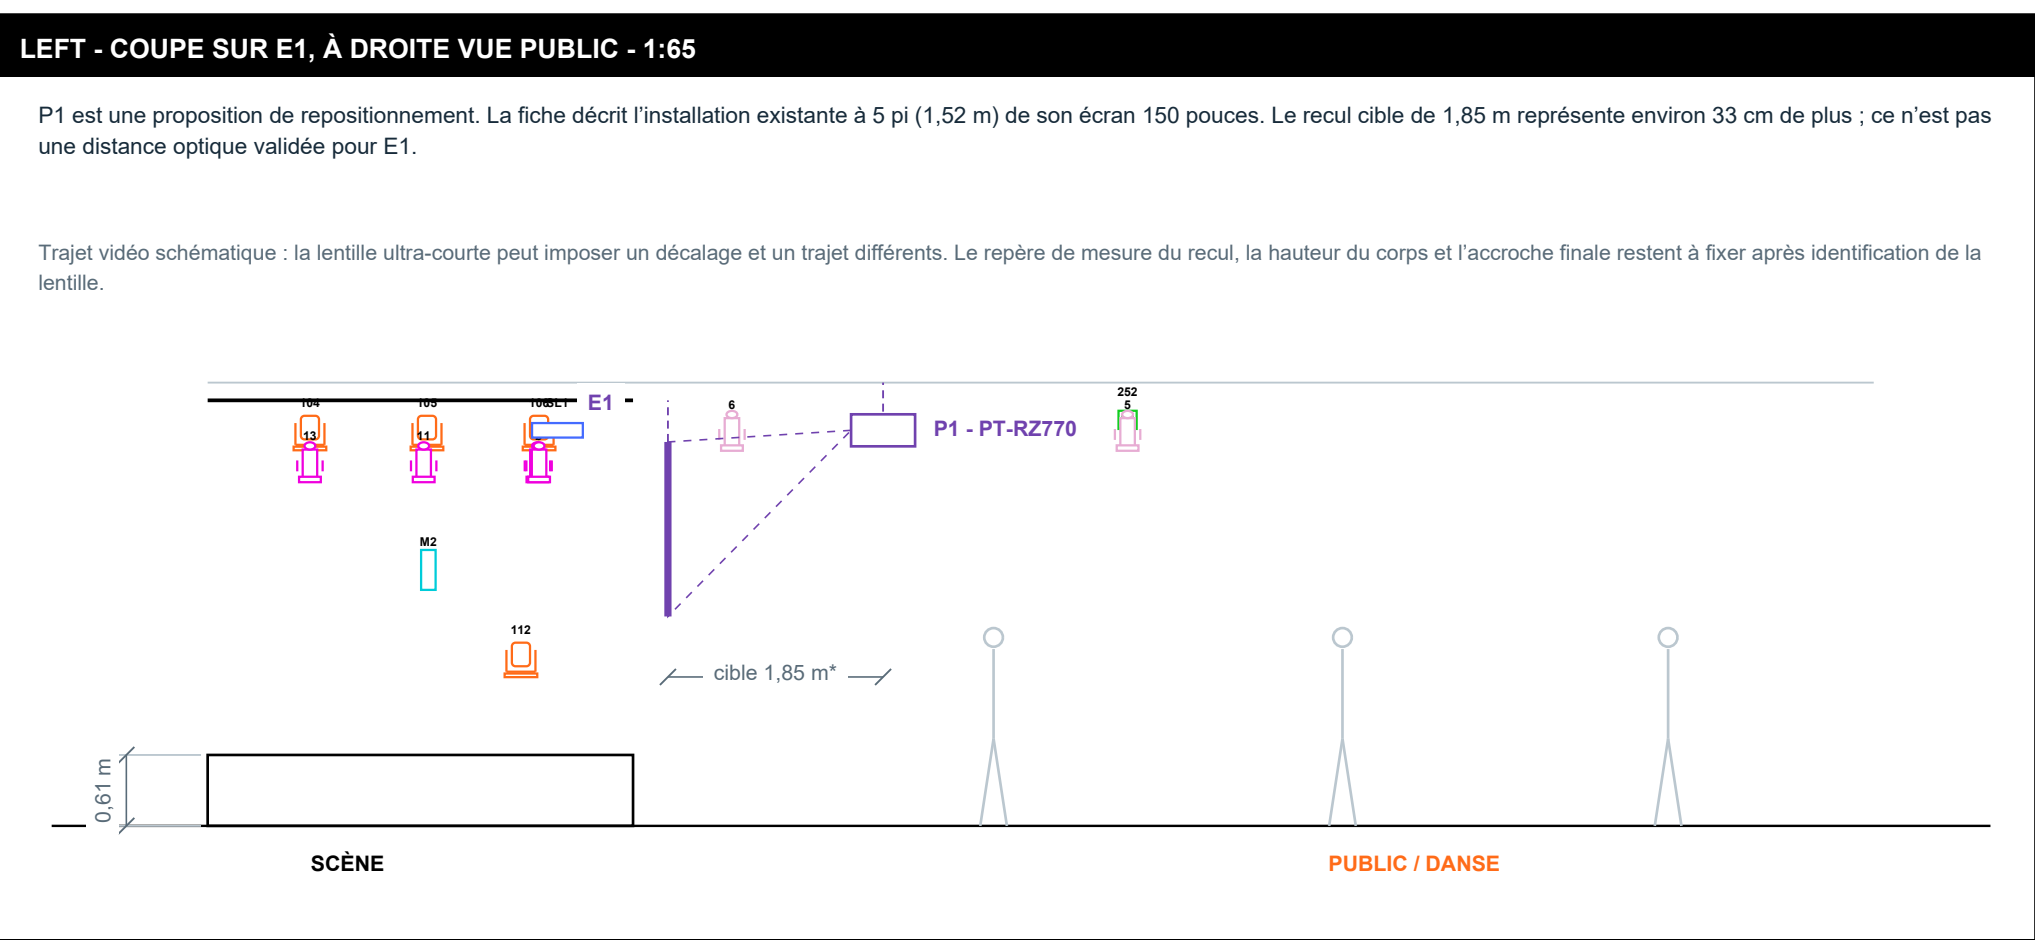

- NOTES TECHNIQUES DE MONTAGE
- Appareils fixes. Ne pas déplacer le kit LX : reprendre ses emplacements et son patch existants. Les pointages vers A/B/C sont à programmer avec Rémi.
 - Écran E1. Ø environ 1,50 m, à droite vue public, juste devant la scène. Deux points de suspension sont représentés comme intention ; ancrages et sécurité secondaire à définir par le DT.
 - Rails jaunes. Le dossier interdit l'accrochage des appareils sur les rails à rideaux. Utiliser uniquement les points approuvés par la salle.
 - Projection. Panasonic PT-RZ770 et support Chief VCMU indiqués dans la fiche. La lentille installée n'y est pas nommée. Ne pas appliquer le ratio du zoom standard à l'installation ultra-courte.
 - Public dansant. Limiter pan/tilt pour protéger E1. Vérifier la portée vers C et l'éblouissement de 111/112.
 - Réserve de matériel. Le 8e Source Four 36° et les 6 PAR 56 ne sont pas localisés sur le plan existant : leur affectation demande le repérage du DT.

ISOMÉTRIE DE REPÉRAGE - SANS ÉCHELLE - IMPLANTATION PROPOSÉE

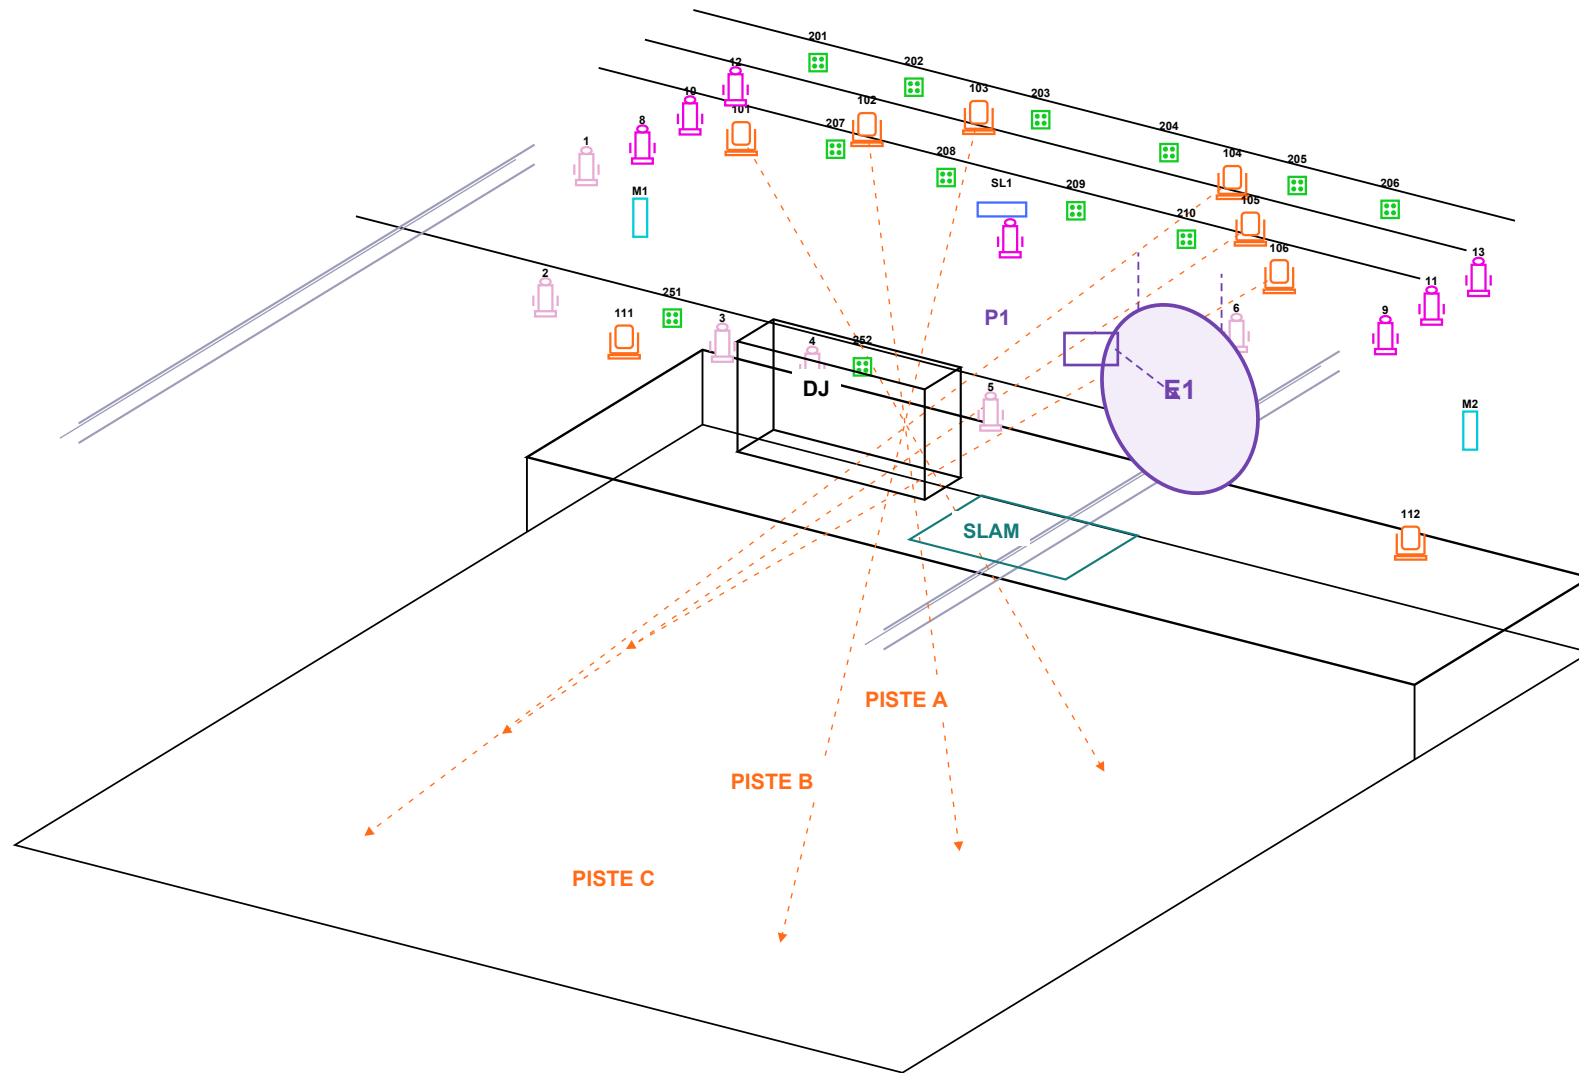

Même code couleur que le plan LX : positions existantes + intentions de pointage. Le réglage final se fait sur place.

COTES À REPORTER ET RÉGLAGES POUR LE DT

Élément	Cote / destination	Application
E1 - écran	x +2,15 ; y -0,30 ; Ø 1,50 m	Bas +1,80 m / sol salle proposé. Hauteur à régler avec l'optique.
P1 - vidéo	x +2,15 ; y -2,15 ; recul cible 1,85 m	Marge incluse : +0,33 m par rapport à la fiche. Compatibilité à valider.
DJ / slam	DJ : x -2,00 ; y +1,80. Slam : x 0 ; y +1,10.	Table 1,80 x 0,75 m proposée ; passage central dégagé.
Lumière salle	101/106 : A ; 102/105 : B ; 103/104 : C.	Pointage initial ; 111/112 en complément si les angles conviennent.

Sources : dossier Audio-LX du Ministère (dimensions, inventaire, support et installation vidéo) ; plan LX communiqué par Rémi ; spécifications Panasonic PT-RZ770. Les cotes du nouveau setup sont des propositions de conception, pas un relevé de l'existant.

ÉQUIPEMENTS TECHNIQUES LX - FICHE SALLE

Appareil	Qté	Donnée principale
Colorado 1 Tri Tour	12	LED RGB / ARC1
Intimidator Spot 375Z	8	6 suspendus + 2 bas
Source Four 25-50°	6	750 W / TL3
Source Four 36°	8	575 W / 7 dessinés
DMG SL1 Mix	1	200 W
DMG Mini Mix	2	100 W
PAR 56 WFL	6	500 W / non localisés

Commande : GrandMA3 Command Wing Compact sur PC.
Gradateurs : 4 Lite-Putter DX-1210 ; 1 Chauvet Data Stream 4.
Brouillard : Antari F-1W, usage à convenir.
Complément : conserver l'éclairage général de salle pour accueil et circulation.

VIDÉOPROJECTION - DONNÉES DOCUMENTÉES

Panasonic PT-RZ770
Laser DLP ; 7 000 lumens nominaux.
Résolution native : 1920 x 1200, 16:10.
HDMI disponible ; câble annoncé par Rémi.

Installation décrite par la salle :
Support Chief VCMU ; ultra short throw ; à 5 pi (1,52 m) de l'écran existant 16:9 de 150
pouces.

Écran de ce projet : cercle Ø 1,50 m. Prévoir un masque circulaire. Une image 16:10 de 1,50 m de haut mesure 2,40 m de large avant masque.

À relever : référence de lentille et repère exact des 5 pi. Le modèle est connu ; le ratio de l'optique installée n'est pas fourni.