

VUE PUBLIC : DJ À GAUCHE / ÉCRAN + VIDÉO À DROITE - TOP 1:65

KIT LX ET AJOUT PROPOSÉ

Kit du plan original conservé. Orange : Intimidator vers la piste. Gris : pointage proposé des 6 PAR 56 S1-S6, pris dans l'inventaire de la salle.

DJ À GAUCHE VUE PUBLIC

Table proposée 1,80 x 0,75 m. Centre : x = -2,00 ; y = +1,80. À mi-profondeur de scène.

ÉCRAN À DROITE VUE PUBLIC

E1 : centre x = +2,15 ; y = -0,30. Écran suspendu devant le nez de scène. Ø environ 1,50 m.

VIDÉOPROJECTEUR À DROITE

Panasonic PT-RZ770. Repère proposé x = +2,15 ; y = -2,15. Recul cible 1,85 m, marge incluse, à valider optiquement. P0 vert : position d'origine.

LUMIÈRES DANS LA SALLE

6 PAR 56 S1-S6 proposés sur la barre salle à y = -4,25 m. S1/S6 vers A ; S3/S4 vers B ; S2/S5 vers C. Implantation et disponibilité à valider.

CADRAGE DU PLAN

Origine au centre du nez de scène. x positif à droite du public ; y positif vers le fond de scène. Dimensions nominales de la fiche.

LÉGENDE - APPAREILS DU MINISTÈRE

Symbole	Appareil	Qté	DMX
	ETC Source Four 36°	8*	1
	ETC Source Four 25/50 Zoom	6	1
	Colorado 1 Tour-Tri	12	ARC1 / 3
	Intimidator Spot 375Z	8	15
	DMG SL1 Mix 200 W	1	4**
	DMG Mini Mix 100 W	2	4**
	PAR 56 WFL 500 W	6*	1

* Source Four 36° : 8 inventoriés, 7 dessinés.

PAR 56 : S1-S6 = emplacements proposés, à valider.

** Modes repris du plan LX ; conserver le patch.

IMPLANTATION DEMANDÉE - REPÈRES

E1 : écran rond suspendu Ø 1,50 m. Bas proposé +1,80 m, haut +3,30 m / sol salle.

P1 : recul cible 1,85 m, soit +0,33 m par rapport au recul de la fiche. Marge souhaitée de +0,30 à +0,50 m, soumise à l'optique et au support.

Piste : 6 PAR 56 proposés dans la salle pour une base fixe graduable, complétée par les 8 Intimidator existants. Les PAR ne sont pas attestés libres ou déjà installés à ces positions.


CARTOUCHE ET BASE DU PLAN

DT : Rémi LeGresley - Le Ministère

Base : dossier Audio-LX fourni + plan LX 2023 envoyé par Rémi.

Statut : implantation et pointages proposés. Emplacements LX repris graphiquement ; conserver les points réels. Accroches E1/P1 à valider.

FRONT - VUE DEPUIS LE PUBLIC - 1:50

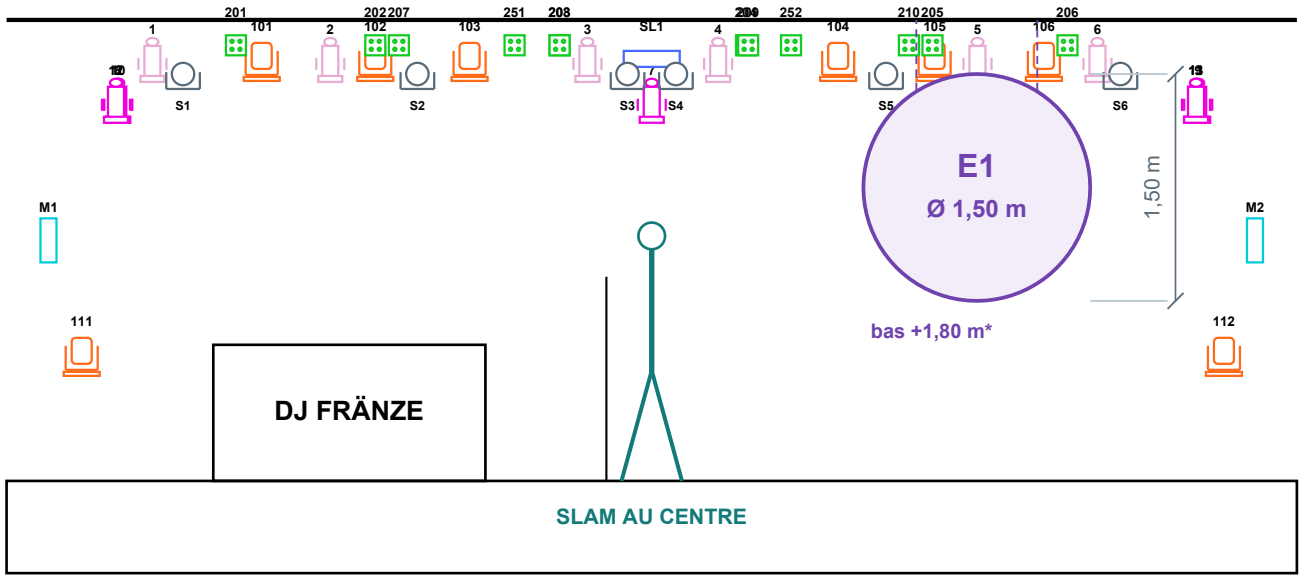

* Cotes de l'écran proposées ; hauteur à régler avec l'optique, la visibilité et les accroches.

LÉGENDE - APPAREILS DU MINISTÈRE


Symbole	Appareil	Qté	DMX
	ETC Source Four 36°	8*	1
	ETC Source Four 25/50 Zoom	6	1
	Colorado 1 Tour-Tri	12	ARC1 / 3
	Intimidator Spot 375Z	8	15
	DMG SL1 Mix 200 W	1	4**
	DMG Mini Mix 100 W	2	4**
	PAR 56 WFL 500 W	6*	1

* Source Four 36° : 8 inventoriés, 7 dessinés.
PAR 56 : S1-S6 = emplacements proposés, à valider.
** Modes repris du plan LX ; conserver le patch.

LEFT - COUPE SUR E1, À DROITE VUE PUBLIC - 1:65

P1 est une proposition de repositionnement. La fiche décrit l'installation existante à 5 pi (1,52 m) de son écran 150 pouces. Le recul cible de 1,85 m représente environ 33 cm de plus ; ce n'est pas une distance optique validée pour E1.


Trajet vidéo schématique : la lentille ultra-courte peut imposer un décalage et un trajet différents. Le repère de mesure du recul, la hauteur du corps et l'accroche finale restent à fixer après identification de la lentille.

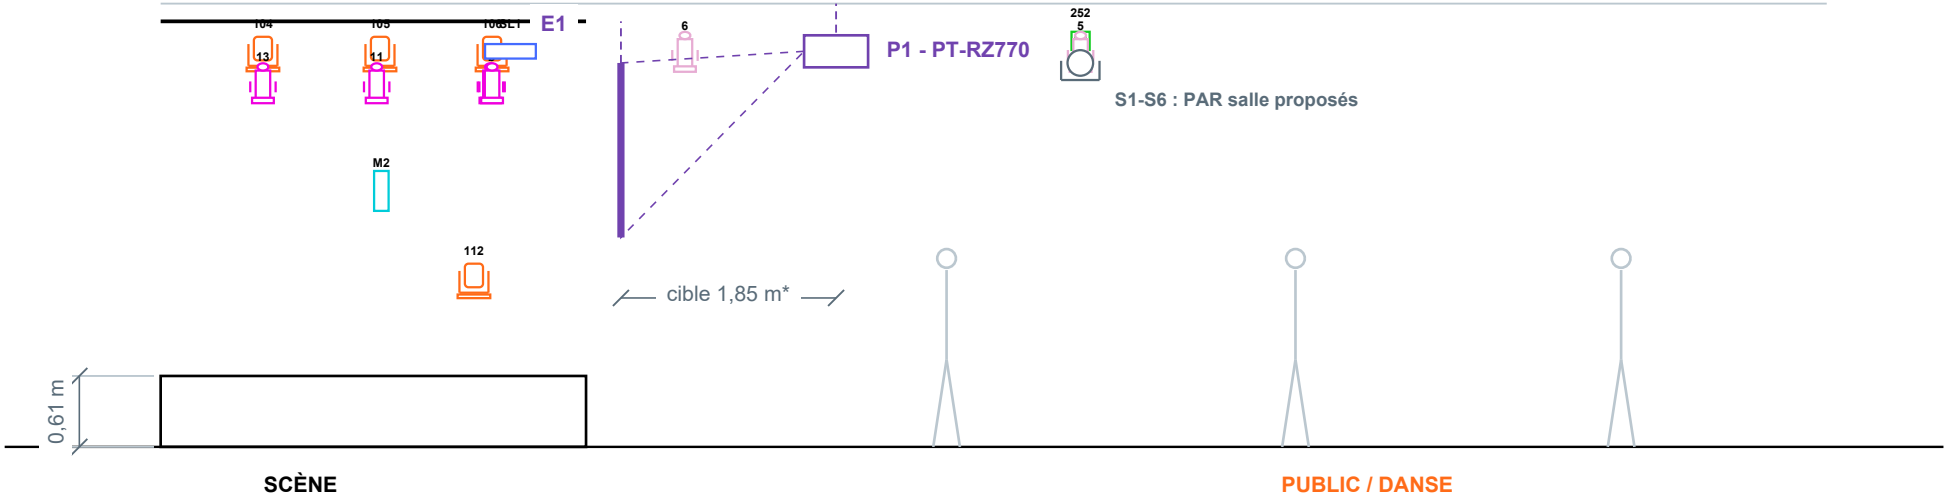

NOTES TECHNIQUES DE MONTAGE

- Kit existant. Conserver les positions et le patch du plan LX original. Les PAR S1-S6 sont une proposition complémentaire avec du matériel inventorié, non une implantation existante confirmée.
- Écran E1. Ø environ 1,50 m, à droite vue public, juste devant la scène. Suspension et sécurité secondaire à définir par le DT.
- Lumières dans la salle. Proposer S1-S6 sur la barre transversale existante, à 4,25 m du nez de scène. Vérifier place disponible, charge, accroches, gradateurs et disponibilité des PAR. Puissance totale : 6 x 500 W = 3 kW.
- Projection. PT-RZ770 et Chief VCMU documentés. Lentille installée non nommée : ne pas appliquer le ratio du zoom standard à l'installation ultra-courte.
- Public dansant. PAR : base fixe graduable. Intimidator : effets complémentaires, pan/tilt limités autour d'E1. Régler l'éblouissement et la couverture au fond.
- Accroches. Aucun appareil sur les rails à rideaux. Points approuvés par la salle uniquement. Le 8e Source Four 36° reste non localisé.

ISOMÉTRIE DE REPÉRAGE - SANS ÉCHELLE - IMPLANTATION PROPOSÉE

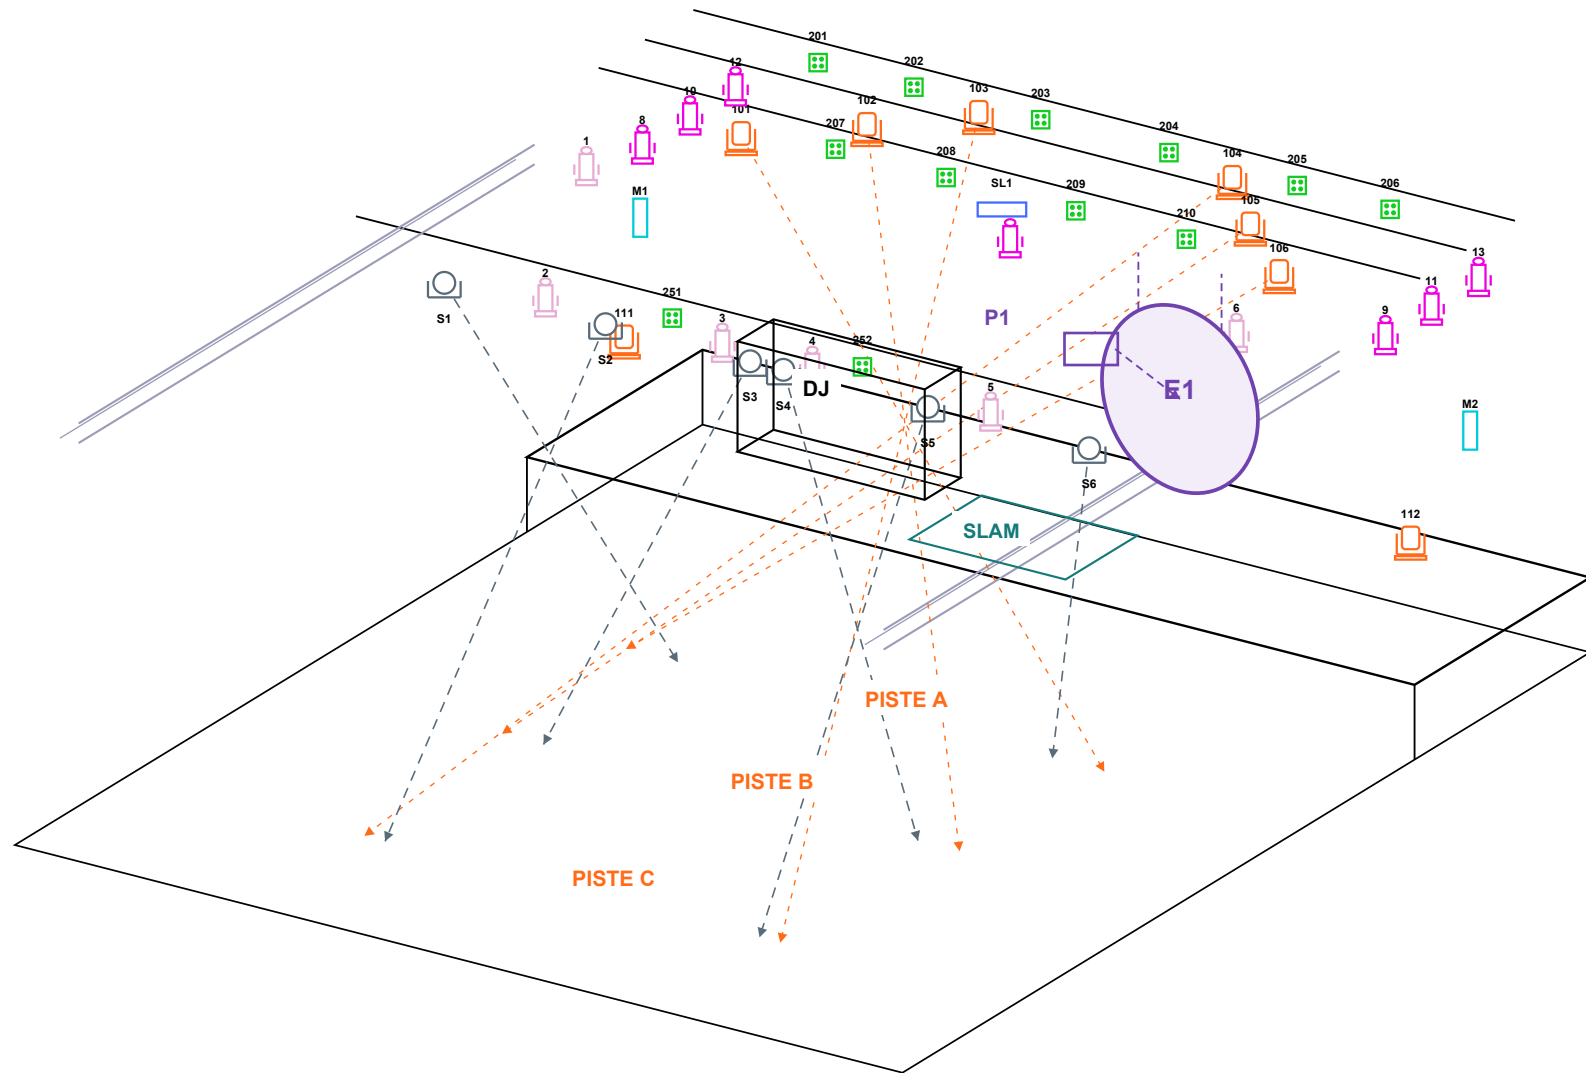

S1-S6 : 6 PAR proposés au-dessus de la piste. Les autres appareils conservent les positions du plan LX existant.

COTES À REPORTER ET RÉGLAGES POUR LE DT

Élément	Cote / destination	Application
E1 - écran	x +2,15 ; y -0,30 ; Ø 1,50 m	Bas +1,80 m / sol salle proposé. Hauteur à régler avec l'optique.
P1 - vidéo	x +2,15 ; y -2,15 ; recul cible 1,85 m	Marge incluse : +0,33 m par rapport à la fiche. Compatibilité à valider.
DJ / slam	DJ : x -2,00 ; y +1,80. Slam : x 0 ; y +1,10.	Table 1,80 x 0,75 m proposée ; passage central dégagé.
PAR S1-S6	y -4,25 ; x -3,10 / -1,55 / -0,16 / +0,16 / +1,55 / +3,10.	Hauteur de corps proposée +3,30 m. S1/S6 : A ; S3/S4 : B ; S2/S5 : C.

Sources : dossier Audio-LX du Ministère (dimensions, inventaire, support et installation vidéo) ; plan LX communiqué par Rémi ; spécifications Panasonic PT-RZ770. Les cotes du nouveau setup sont des propositions de conception, pas un relevé de l'existant.

ÉQUIPEMENTS TECHNIQUES LX - FICHE SALLE

Appareil	Qté	Donnée principale
Colorado 1 Tri Tour	12	LED RGB / ARC1
Intimidator Spot 375Z	8	6 suspendus + 2 bas
Source Four 25-50°	6	750 W / TL3
Source Four 36°	8	575 W / 7 dessinés
DMG SL1 Mix	1	200 W
DMG Mini Mix	2	100 W
PAR 56 WFL	6	500 W / S1-S6 proposés

Commande : GrandMA3 Command Wing Compact sur PC.
Gradateurs : 4 Lite-Putter DX-1210 ; 1 Chauvet Data Stream 4.
Brouillard : Antari F-1W, usage à convenir.
Complément : conserver l'éclairage général de salle pour accueil et circulation.

VIDÉOPROJECTION - DONNÉES DOCUMENTÉES

Panasonic PT-RZ770
Laser DLP ; 7 000 lumens nominaux.
Résolution native : 1920 x 1200, 16:10.
HDMI disponible ; câble annoncé par Rémi.

Installation décrite par la salle :
Support Chief VCMU ; ultra short throw ; à 5 pi (1,52 m) de l'écran existant 16:9 de 150
pouces.

Écran de ce projet : cercle Ø 1,50 m. Prévoir un masque circulaire. Une image 16:10 de 1,50 m de haut mesure 2,40 m de large avant masque.

À relever : référence de lentille et repère exact des 5 pi. Le modèle est connu ; le ratio de l'optique installée n'est pas fourni.