



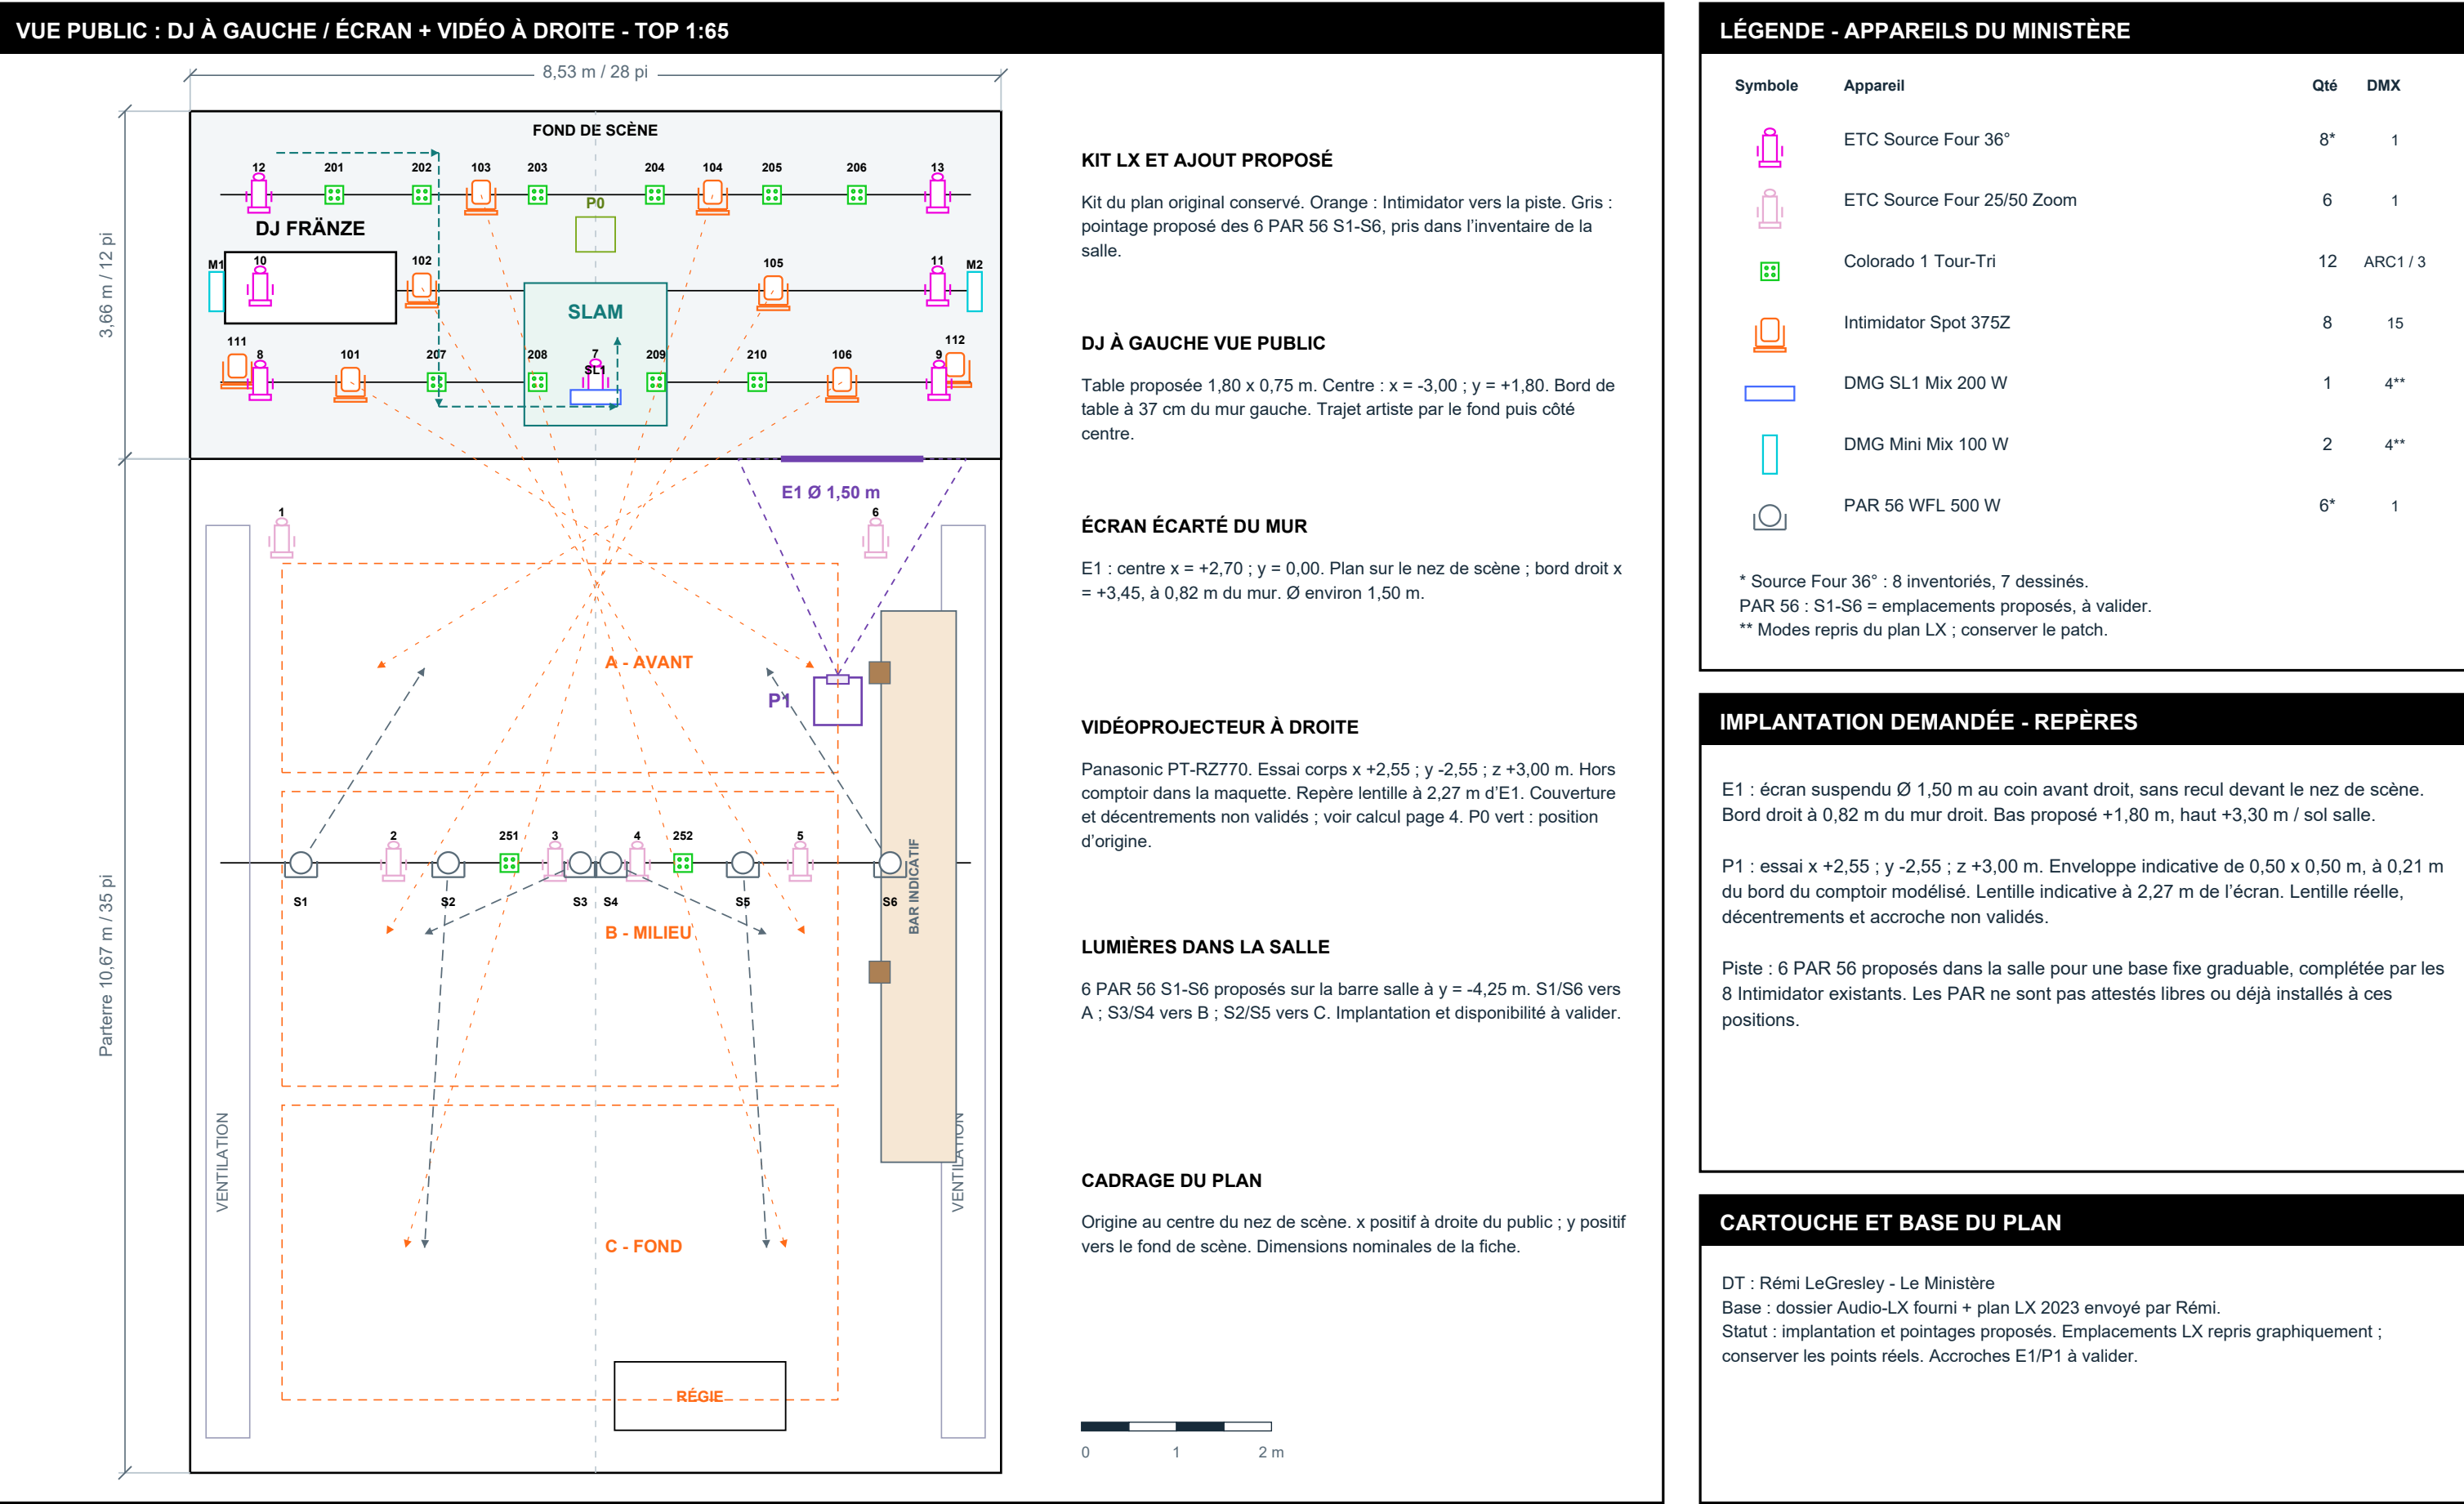

FRONT - VUE DEPUIS LE PUBLIC - 1:50

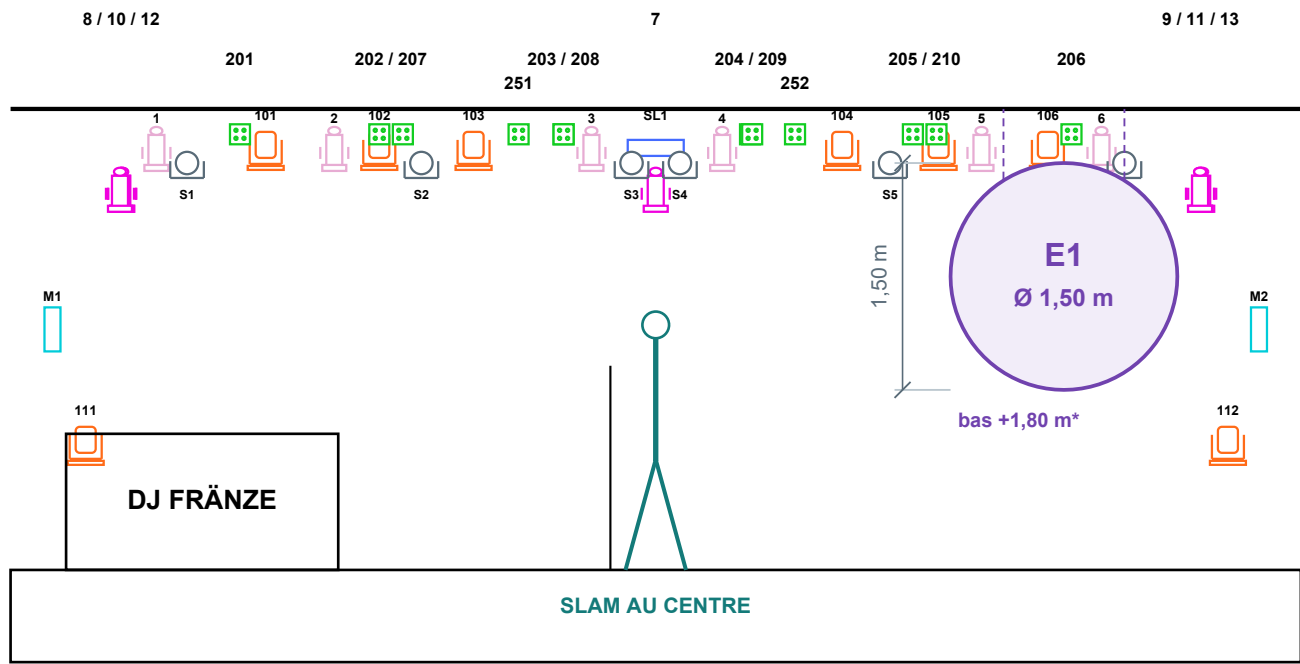


E1 écarté du mur droit. * Hauteur proposée ; à régler avec l'optique, la visibilité et les accroches.

LEFT - COUPE SUR E1, À DROITE VUE PUBLIC - 1:65

P1 est une proposition de repositionnement. La fiche décrit l'installation existante à 5 pi (1,52 m) de son écran 150 pouces. Dans V08 : corps à 2,55 m, repère de lentille indicatif à 2,27 m. La lentille de la salle est inconnue : essai spatial, non validé optiquement.

Trajet vidéo schématique : la lentille ultra-courte peut imposer un décalage et un trajet différents. Le repère de mesure du recul, la hauteur du corps et l'accroche finale restent à fixer après identification de la lentille.

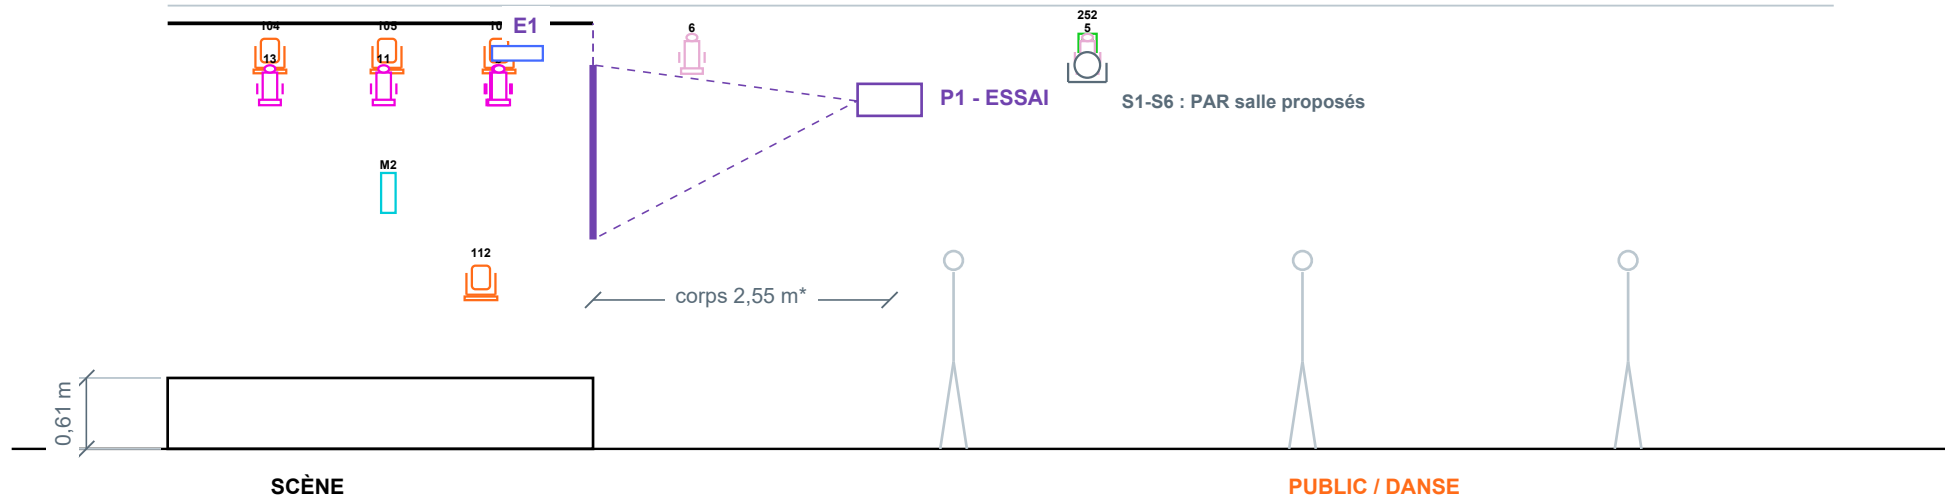

LÉGENDE - APPAREILS DU MINISTÈRE


Symbole	Appareil	Qté	DMX
	ETC Source Four 36°	8*	1
	ETC Source Four 25/50 Zoom	6	1
	Colorado 1 Tour-Tri	12	ARC1 / 3
	Intimidator Spot 375Z	8	15
	DMG SL1 Mix 200 W	1	4**
	DMG Mini Mix 100 W	2	4**
	PAR 56 WFL 500 W	6*	1

* Source Four 36° : 8 inventoriés, 7 dessinés.
PAR 56 : S1-S6 = emplacements proposés, à valider.
** Modes repris du plan LX ; conserver le patch.

NOTES TECHNIQUES DE MONTAGE

- Kit existant. Conserver les positions et le patch du plan LX original. Les PAR S1-S6 sont une proposition complémentaire avec du matériel inventorié, non une implantation existante confirmée.
- Écran E1. Ø environ 1,50 m, suspendu à l'avant droit, écarté du mur vue public. Plan de l'écran sur le nez de scène (y = 0) ; bord droit à 0,82 m du mur. Suspension et sécurité secondaire à définir par le DT.
- Lumières dans la salle. Proposer S1-S6 sur la barre transversale existante, à 4,25 m du nez de scène. Vérifier place disponible, charge, accroches, gradateurs et disponibilité des PAR. Puissance totale : 6 x 500 W = 3 kW.
- Projection. PT-RZ770 et Chief VCMU documentés. Lentille installée non nommée : ne pas appliquer le ratio du zoom standard à l'installation ultra-courte. P1 hors du bar modélisé. Repère lentille à 2,27 m de l'écran, compatible en distance avec ET-DLE085 seulement parmi les deux exemples calculés page 4. Lentille de la salle inconnue.
- Public dansant. PAR : base fixe graduable. Intimidator : effets complémentaires, pan/tilt limités autour d'E1. Régler l'éblouissement et la couverture au fond.
- Accroches. Aucun appareil sur les rails à rideaux. Points approuvés par la salle uniquement. Le 8e Source Four 36° reste non localisé.

ISOMÉTRIE DE REPÉRAGE - SANS ÉCHELLE - IMPLANTATION PROPOSÉE

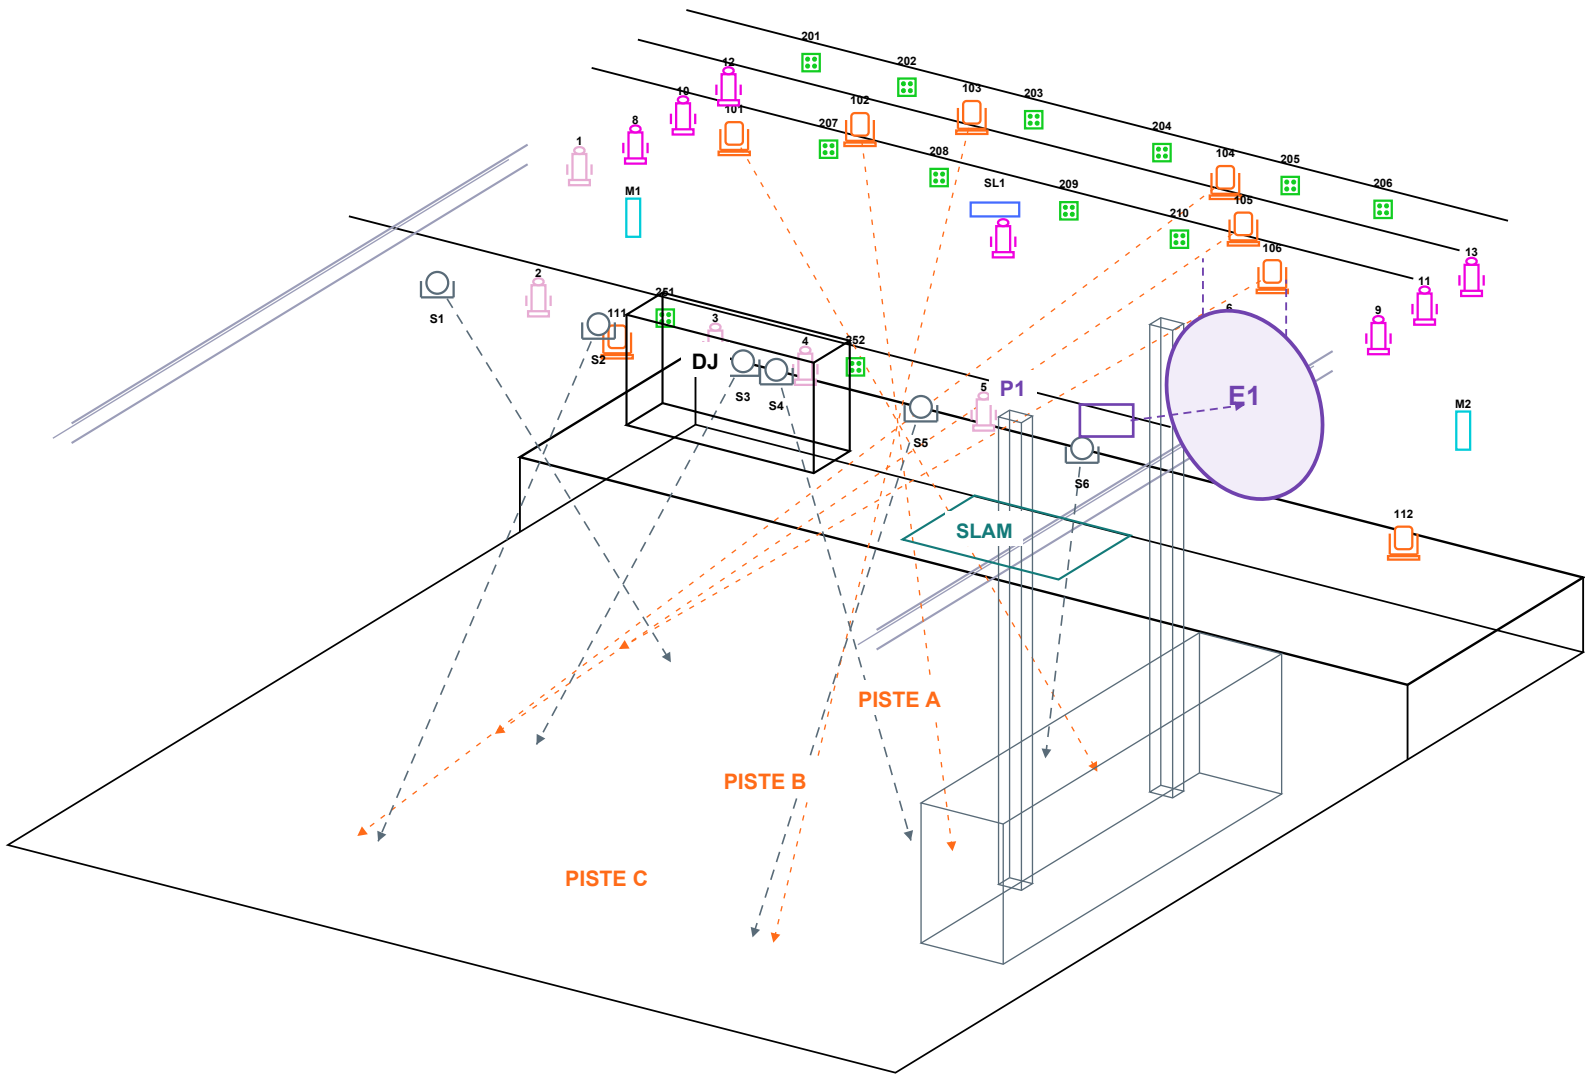

S1-S6 : 6 PAR proposés au-dessus de la piste. Les autres appareils conservent les positions du plan LX existant.

COTES À REPORTER ET RÉGLAGES POUR LE DT

Élément	Cote / destination	Application
E1 - écran	x +2,70 ; y 0,00 ; Ø 1,50 m	Bord droit x +3,45 ; mur à 0,82 m. Bas proposé +1,80 m / sol salle.
P1 - vidéo	x +2,55 ; y -2,55 ; z +3,00 m	Hors comptoir modélisé. Repère lentille à 2,27 m. Optique, décentrement et support non validés.
DJ / slam	DJ : x -3,00 ; y +1,80. Slam : x 0 ; y +1,10.	Table 1,80 x 0,75 m ; mur gauche à 37 cm. Passage artiste derrière puis côté centre.
PAR S1-S6	y -4,25 ; x -3,10 / -1,55 / -0,16 / +0,16 / +1,55 / +3,10.	Hauteur de corps proposée +3,30 m. S1/S6 : A ; S3/S4 : B ; S2/S5 : C.

Sources : dossier Audio-LX du Ministère (dimensions, inventaire, support et installation vidéo) ; plan LX communiqué par Rémi ; spécifications Panasonic PT-RZ770. Les cotes du nouveau setup sont des propositions de conception, pas un relevé de l'existant.

ÉQUIPEMENTS TECHNIQUES LX - FICHE SALLE

Appareil	Qté	Donnée principale
Colorado 1 Tri Tour	12	LED RGB / ARC1
Intimidator Spot 375Z	8	6 suspendus + 2 bas
Source Four 25-50°	6	750 W / TL3
Source Four 36°	8	575 W / 7 dessinés
DMG SL1 Mix	1	200 W
DMG Mini Mix	2	100 W
PAR 56 WFL	6	500 W / S1-S6 proposés

Commande : GrandMA3 Command Wing Compact sur PC.
Gradateurs : 4 Lite-Putter DX-1210.
Distribution DMX : 1 Chauvet Data Stream 4.
Brouillard : Antari F-1W, usage à convenir.
Complément : conserver l'éclairage général de salle pour accueil et circulation.

VIDÉOPROJECTION - DONNÉES DOCUMENTÉES

Panasonic PT-RZ770
Laser DLP ; 7 000 lumens nominaux.
Résolution native : 1920 x 1200, 16:10.
HDMI disponible ; câble annoncé par Rémi.

Installation décrite par la salle :
Support Chief VCMU ; ultra short throw ; à 5 pi (1,52 m) de l'écran existant 16:9 de 150 pouces.

Écran de ce projet : cercle Ø 1,50 m. Prévoir un masque circulaire. Une image 16:10 de 1,50 m de haut mesure 2,40 m de large avant masque.

À relever : référence de lentille et repère exact des 5 pi. Le modèle est connu ; le ratio de l'optique installée n'est pas fourni.

DONNÉES COMMUNES - V08 - ESSAI SPATIAL, PAS UN PLAN DE MONTAGE VALIDÉ		
Le PDF et la maquette lisent le même fichier implantation.json : positions E1/P1/DJ, dimensions principales, trajet artiste, bar, poteaux et 42 appareils repérés. Le repère de géométrie est identique dans les deux livrables. Cette concordance ne remplace pas un relevé architectural.		
Élément	Repères communs en mètres	Niveau de validation
Scène / parterre	8,5344 x 3,6576 ; parterre 8,5344 x 10,668	Dimensions nominales du dossier de salle
Écran E1	x 2.70 ; y 0.00 ; z 2.55 ; diamètre 1.50	Proposé : suspension et visibilité à valider
Projecteur P1	x 2.55 ; y -2.55 ; z 3.00	Enveloppe indicative ; lentille et support inconnus
DJ	x -3.00 ; y 1.80 ; table 1,80 x 0,75	Proposé ; dégagement mur 0,367 m
Bar / poteaux	Mêmes volumes indicatifs dans les deux vues	Aucun relevé coté disponible ; collisions réelles non garanties
Lumières	36 repérées existantes + 6 PAR proposés = 42	Positions reprises graphiquement ; accroches réelles à conserver

CALCUL DE COUVERTURE - IDENTIFIER LA LENTILLE AVANT DE FIXER LE REcul
Cercle de 1,50 m : image native 16:10 de 2,40 x 1,50 m, puis masque circulaire. Diagonale = sqrt(2,40² + 1,50²) / 0,0254 = 111.425 pouces. Le cercle n'est pas la diagonale du rectangle.
ET-DLE085 : Lmin = D x 0,0174 - 0,0471 = 1.892 m ; Lmax = D x 0,0216 - 0,0442 = 2.363 m. ET-DLE170 standard : Lmin = D x 0,0379 - 0,0746 = 4.148 m ; Lmax = D x 0,0529 - 0,0725 = 5.822 m.
Essai V08 : distance perpendiculaire du repère lentille indicatif à E1 = 2,55 - 0,28 = 2,27 m. Dans la plage ET-DLE085, hors plage standard. Décentrement latéral 0,15 m et vertical 0,44 m à contrôler avec la lentille et son repère réel.
La salle ne nomme pas sa lentille. Elle décrit une installation ultra-courte à 5 pieds d'un écran 150 pouces. Cela ne confirme ni ET-DLE085 ni ET-DLE170. Les rayons V08 montrent le gabarit à obtenir, pas le trajet optique réel. Bar et poteaux sont approximatifs. Ne pas monter à partir de ces seuls tracés.
Source de calcul : Panasonic PT-RZ770 Spec File, page 15, tableau 16:10 (mars 2020). Contrôle sur place requis : lentille, recul et décentrement, refroidissement, structure porteuse, cotes du bar et visibilité de l'écran.