


**VUE PUBLIC : DJ À GAUCHE / ÉCRAN + VIDÉO À DROITE - TOP 1:65**

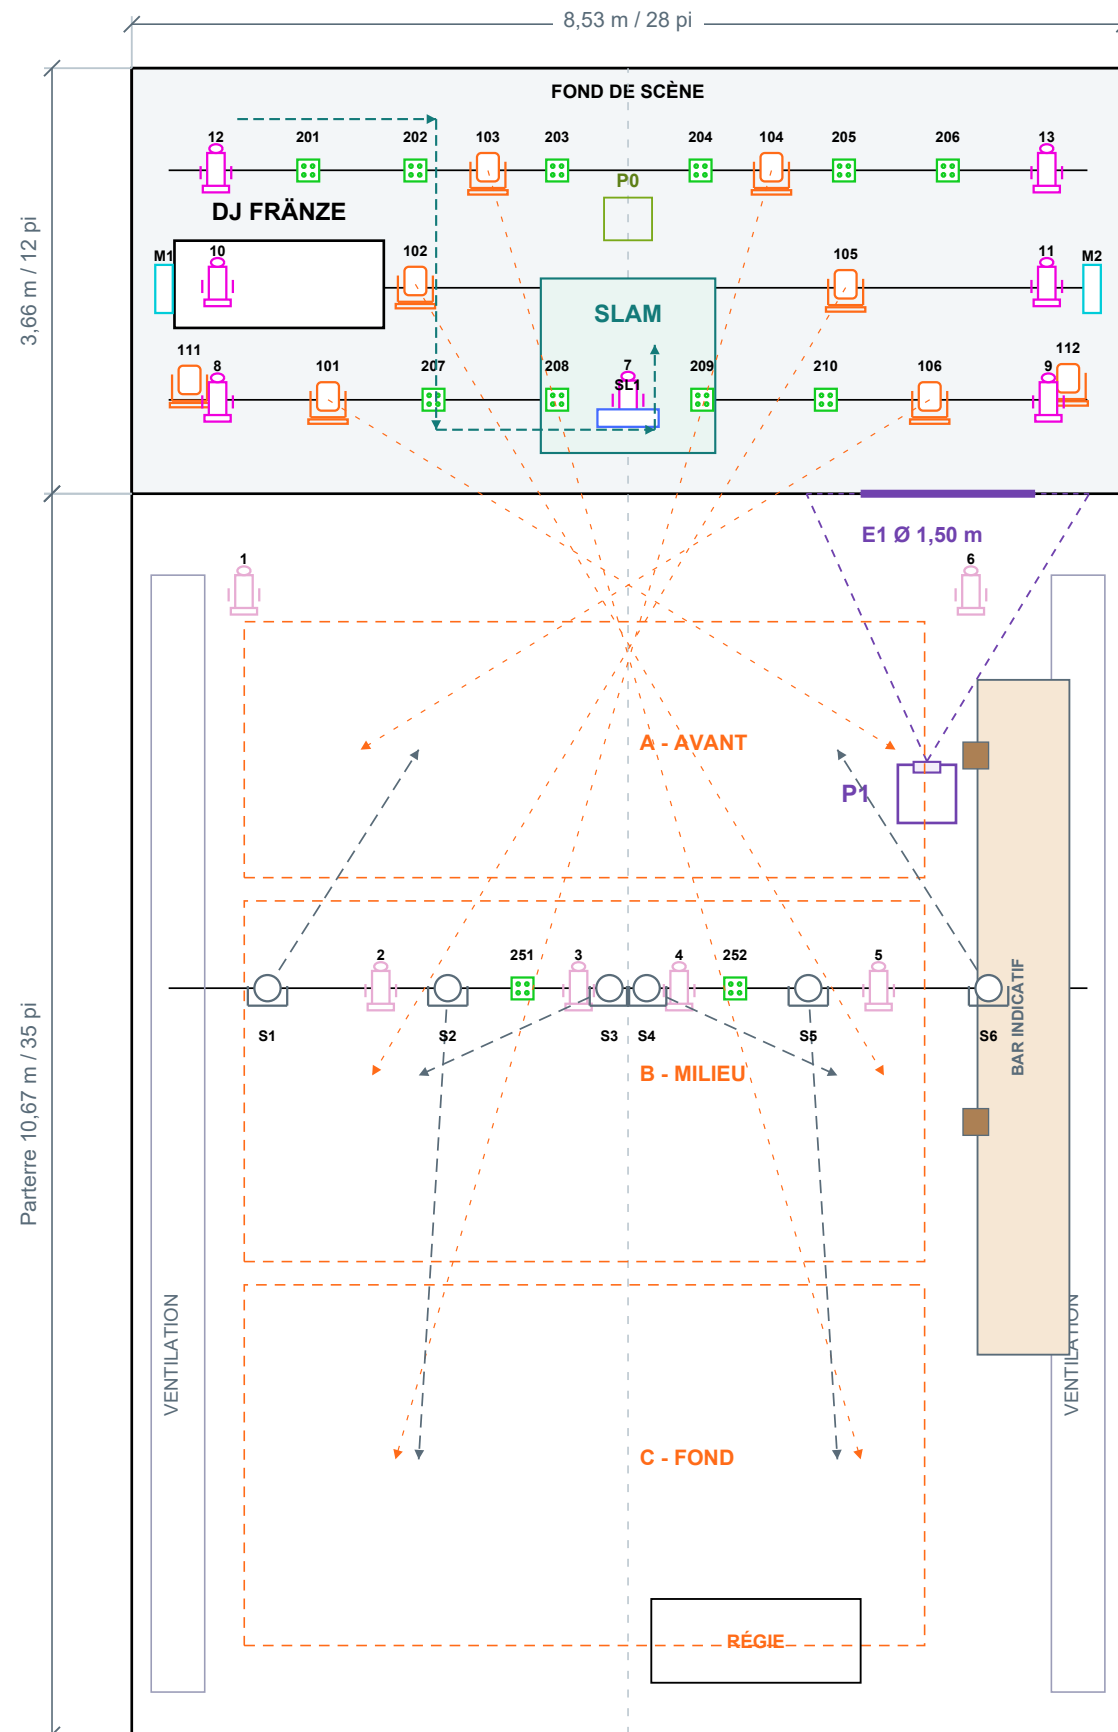

### KIT LX ET AJOUT PROPOSÉ

Kit du plan original conservé. Orange : Intimidator vers la piste. Gris : pointage proposé des 6 PAR 56 S1-S6, pris dans l'inventaire de la salle.

## DJ À GAUCHE VUE PUBLIC

Table proposée 1,80 x 0,75 m. Centre :  $x = -3,00$  ;  $y = +1,80$ . Bord de table à 37 cm du mur gauche. Trajet artiste par le fond puis côté centre.

## ÉCRAN ÉCARTÉ DU MUR

E1 : centre  $x = +2,75$  ;  $y = 0,00$ . Plan sur le nez de scène ; bord droit  $x = +3,50$ , à 0,77 m du mur. Ø environ 1,50 m.

## VIDÉOPROJECTEUR À DROITE

Panasonic PT-RZ770. Essai corps  $x + 2,57$ ;  $y - 2,58$ ;  $z + 3,00$  m. Hors comptoir dans la maquette. Repère lentille à  $2,30$  m d'E1. Couverture et décentrement non validés ; voir calcul page 4. P0 vert : position d'origine.

## LUMIÈRES DANS LA SALLE

6 PAR 56 S1-S6 proposés sur la barre salle à y = -4,25 m. S1/S6 vers A ; S3/S4 vers B ; S2/S5 vers C. Implantation et disponibilité à valider.

## CADRAGE DU PLAN

Origine au centre du nez de scène. x positif à droite du public ; y positif vers le fond de scène. Dimensions nominales de la fiche.



### LÉGENDE - APPAREILS DU MINISTÈRE

| Symbole                                                                             | Appareil                   | Qté | DMX      |
|-------------------------------------------------------------------------------------|----------------------------|-----|----------|
|  | ETC Source Four 36°        | 8*  | 1        |
|  | ETC Source Four 25/50 Zoom | 6   | 1        |
|  | Colorado 1 Tour-Tri        | 12  | ARC1 / 3 |
|  | Intimidator Spot 375Z      | 8   | 15       |
|  | DMG SL1 Mix 200 W          | 1   | 4**      |
|  | DMG Mini Mix 100 W         | 2   | 4**      |
|  | PAR 56 WFL 500 W           | 6*  | 1        |

\* Source Four 36° : 8 inventoriés, 7 dessinés.

PAR 56 : S1-S6 = emplacements proposés, à valider.

\*\* Modes repris du plan LX ; conserver le patch.

## IMPLANTATION DEMANDÉE - REPÈRES

E1 : écran suspendu Ø 1,50 m au coin avant droit, sans recul devant le nez de scène.  
Bord droit à 0,77 m du mur droit. Bas proposé +1,80 m, haut +3,30 m / sol salle.

P1 : essai x +2,57 ; y -2,58 ; z +3,00 m. Enveloppe indicative de 0,50 x 0,50 m, à 0,185 m du bord du comptoir modélisé. Lentille indicative à 2,30 m de l'écran. Lentille réelle, décentrement et accroche non validés.

Piste : 6 PAR 56 proposés dans la salle pour une base fixe graduable, complétée par les 8 Intimidator existants. Les PAR ne sont pas attestés libres ou déjà installés à ces positions.

## CARTOUCHE ET BASE DU PLAN

DT : Rémi LeGresley - Le Ministère

Base : dossier Audio-LX fourni + plan LX 2023 envoyé par Rémi.

Statut : implantation et pointages proposés. Emplacements LX repris graphiquement ;  
conserver les points réels. Accroches E1/P1 à valider.

FRONT - VUE DEPUIS LE PUBLIC - 1:50

8 / 10 / 12

201

202 / 207

203 / 208

251

7

204 / 209

252

205 / 210

206

9 / 11 / 13

1

101

2

102

103

3

SL1

4

104

105

5

106

6

S1

S2

S3

S4

S5

M1

111

DJ FRÄNZE

SLAM AU CENTRE

E1

Ø 1,50 m

image Ø 1,48 m

bas +1,80 m\*

1,50 m

M2

112

E1 écarté du mur droit. \* Hauteur proposée ; à régler avec l'optique, la visibilité et les accroches.

| LÉGENDE - APPAREILS DU MINISTÈRE                                                    |                            |     |          |
|-------------------------------------------------------------------------------------|----------------------------|-----|----------|
| Symbole                                                                             | Appareil                   | Qté | DMX      |
|  | ETC Source Four 36°        | 8*  | 1        |
|  | ETC Source Four 25/50 Zoom | 6   | 1        |
|  | Colorado 1 Tour-Tri        | 12  | ARC1 / 3 |
|  | Intimidator Spot 375Z      | 8   | 15       |
|  | DMG SL1 Mix 200 W          | 1   | 4**      |
|  | DMG Mini Mix 100 W         | 2   | 4**      |
|  | PAR 56 WFL 500 W           | 6*  | 1        |

**LEFT - COUPE SUR E1, À DROITE VUE PUBLIC - 1:65**

P1 est une proposition de repositionnement. La fiche décrit l'installation existante à 5 pi (1,52 m) de son écran 150 pouces. Dans V09 : corps à 2,58 m, repère de lentille indicatif à 2,30 m. La lentille de la salle est inconnue : essai spatial, non validé optiquement.

Trajet vidéo schématique : la lentille ultra-courte peut imposer un décalage et un trajet différents. Le repère de mesure du recul, la hauteur du corps et l'accroche finale restent à fixer après identification de la lentille.


The diagram illustrates a stage layout with the following elements:

- Stage (SCÈNE):** A rectangular area on the left, with a depth dimension of 0,61 m.
- Camera Positions:**
  - Top left: Three cameras labeled 104, 105, and 106, each with a small icon below it.
  - Below 105: A camera icon labeled 112.
  - Below 112: A vertical rectangle labeled M2.
  - Top center: A camera icon labeled 6.
  - Top right: A camera icon labeled 252 with a small '5' above it.
- Screen and Projection:**
  - A vertical purple line represents a screen or barrier.
  - To its right, a purple rectangle is labeled P1 - ESSAI.
  - Dashed purple lines form a cone from the top of the purple line towards the P1 - ESSAI rectangle.
  - Below the purple line, a dimension line indicates a distance of corps 2,58 m\*.
- Audience Area (PUBLIC / DANSE):** Three stylized human figures are shown on the right side of the diagram.
- Other Labels:**
  - E1 is labeled above the first camera (104).
  - S1-S6 : PAR salle proposés is written near the 252 camera.

## NOTES TECHNIQUES DE MONTAGE

1. Kit existant. Conserver les positions et le patch du plan LX original. Les PAR S1-S6 sont une proposition complémentaire avec du matériel inventorié, non une implantation existante confirmée.
2. Écran E1. Ø environ 1,50 m, suspendu à l'avant droit, écarté du mur vue public. Plan de l'écran sur le nez de scène ( $y = 0$ ) ; bord droit à 0,77 m du mur. Suspension et sécurité secondaire à définir par le DT.
3. Lumières dans la salle. Proposer S1-S6 sur la barre transversale existante, à 4,25 m du nez de scène. Vérifier place disponible, charge, accroches, gradateurs et disponibilité des PAR. Puissance totale :  $6 \times 500 \text{ W} = 3 \text{ kW}$ .
4. Projection. PT-RZ770 et Chief VCMU documentés. Lentille installée non nommée : ne pas appliquer le ratio du zoom standard à l'installation ultra-courte. P1 hors du bar modélisé. Repère lentille à 2,30 m de l'écran, compatible en distance avec ET-DLE085 seulement parmi les deux exemples calculés page 4. Lentille de la salle inconnue.
5. Public dansant. PAR : base fixe graduable. Intimidator : effets complémentaires, pan/tilt limités autour d'E1. Régler l'éblouissement et la couverture au fond.
6. Accroches. Aucun appareil sur les rails à rideaux. Points approuvés par la salle uniquement. Le 8e Source Four 36° reste non localisé.

ISOMÉTRIE DE REPÉRAGE - SANS ÉCHELLE - IMPLANTATION PROPOSÉE

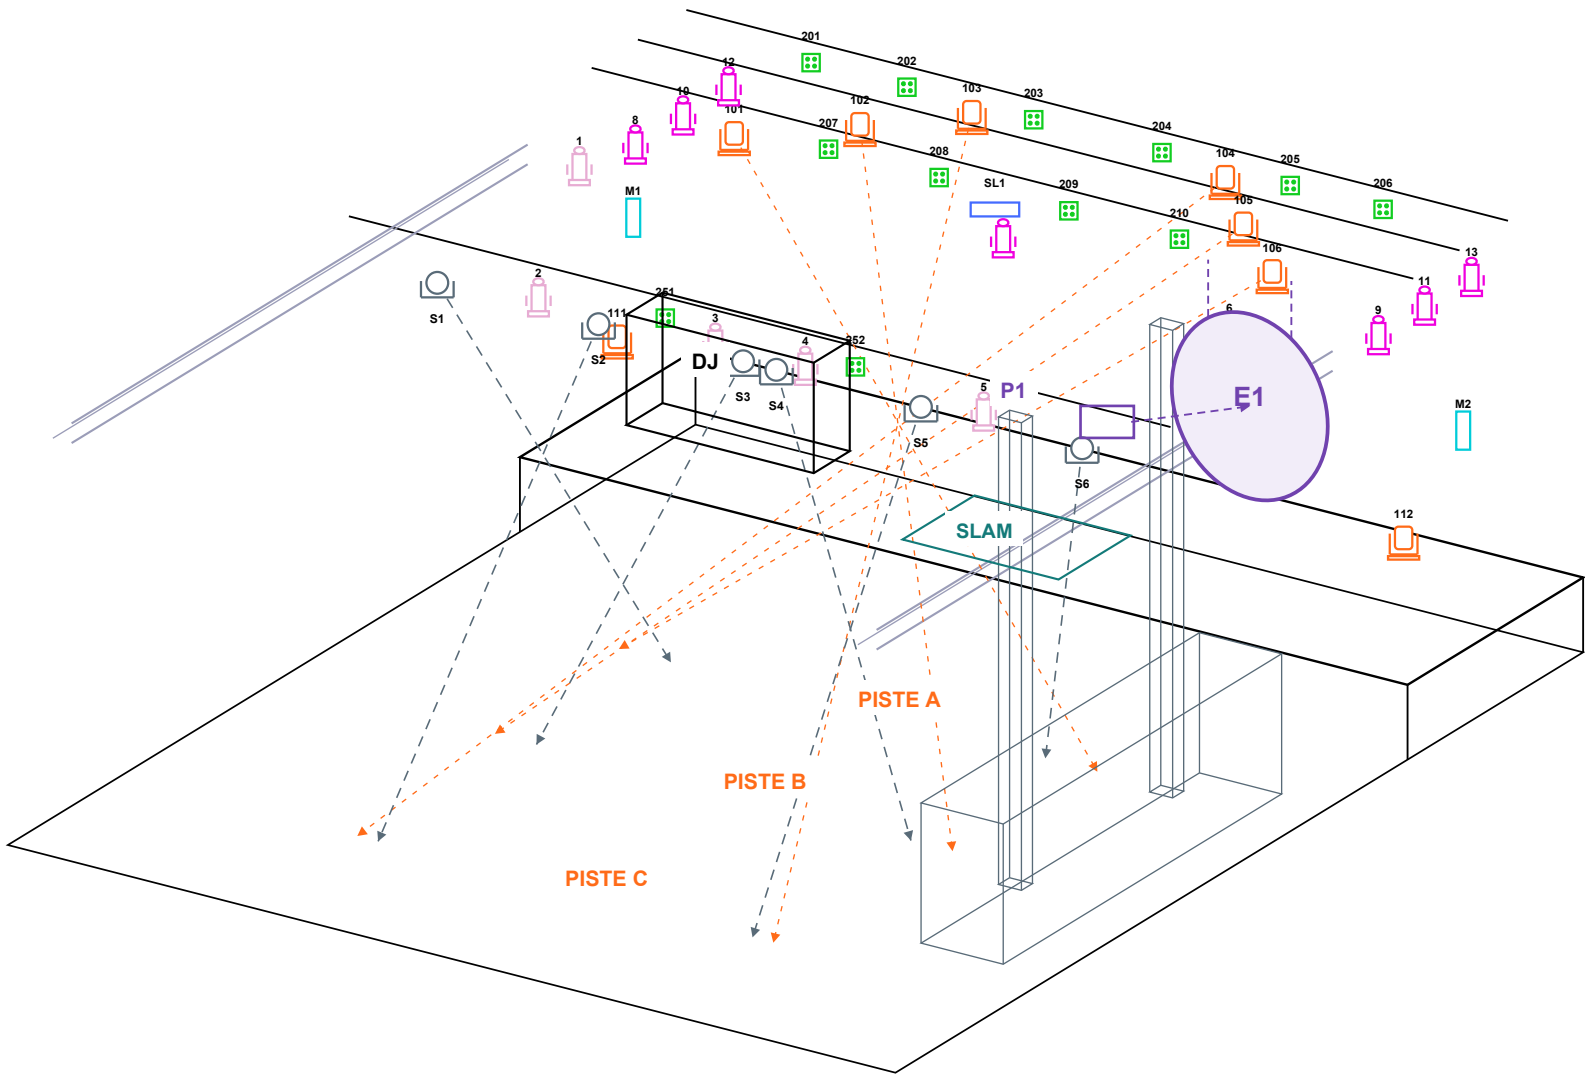

S1-S6 : 6 PAR proposés au-dessus de la piste. Les autres appareils conservent les positions du plan LX existant.

COTES À REPORTER ET RÉGLAGES POUR LE DT

| Élément    | Cote / destination                                         | Application                                                                                     |
|------------|------------------------------------------------------------|-------------------------------------------------------------------------------------------------|
| E1 - écran | x +2,75 ; y 0,00 ; Ø 1,50 m                                | Bord droit x +3,50 ; mur à 0,77 m. Bas proposé +1,80 m / sol salle.                             |
| P1 - vidéo | x +2,57 ; y -2,58 ; z +3,00 m                              | Hors comptoir modélisé. Repère lentille à 2,30 m. Optique, décentrement et support non validés. |
| DJ / slam  | DJ : x -3,00 ; y +1,80. Slam : x 0 ; y +1,10.              | Table 1,80 x 0,75 m ; mur gauche à 37 cm. Passage artiste derrière puis côté centre.            |
| PAR S1-S6  | y -4,25 ; x -3,10 / -1,55 / -0,16 / +0,16 / +1,55 / +3,10. | Hauteur de corps proposée +3,30 m. S1/S6 : A ; S3/S4 : B ; S2/S5 : C.                           |

Sources : dossier Audio-LX du Ministère (dimensions, inventaire, support et installation vidéo) ; plan LX communiqué par Rémi ; spécifications Panasonic PT-RZ770. Les cotes du nouveau setup sont des propositions de conception, pas un relevé de l'existant.

ÉQUIPEMENTS TECHNIQUES LX - FICHE SALLE

| Appareil              | Qté | Donnée principale      |
|-----------------------|-----|------------------------|
| Colorado 1 Tri Tour   | 12  | LED RGB / ARC1         |
| Intimidator Spot 375Z | 8   | 6 suspendus + 2 bas    |
| Source Four 25-50°    | 6   | 750 W / TL3            |
| Source Four 36°       | 8   | 575 W / 7 dessinés     |
| DMG SL1 Mix           | 1   | 200 W                  |
| DMG Mini Mix          | 2   | 100 W                  |
| PAR 56 WFL            | 6   | 500 W / S1-S6 proposés |

Commande : GrandMA3 Command Wing Compact sur PC.  
Gradateurs : 4 Lite-Putter DX-1210.  
Distribution DMX : 1 Chauvet Data Stream 4.  
Brouillard : Antari F-1W, usage à convenir.  
Complément : conserver l'éclairage général de salle pour accueil et circulation.

VIDÉOPROJECTION - DONNÉES DOCUMENTÉES

Panasonic PT-RZ770  
Laser DLP ; 7 000 lumens nominaux.  
Résolution native : 1920 x 1200, 16:10.  
HDMI disponible ; câble annoncé par Rémi.

Installation décrite par la salle :  
Support Chief VCMU ; ultra short throw ; à 5 pi (1,52 m) de l'écran existant 16:9 de 150 pouces.

Écran de ce projet : cercle Ø 1,50 m. Prévoir un masque circulaire. Gabarit V09 : 2,432 x 1,52 m avant masque, image visible Ø 1,48 m, bord noir intérieur de 1 cm. Réserve native pour réglage du masque.

À relever : référence de lentille et repère exact des 5 pi. Le modèle est connu ; le ratio de l'optique installée n'est pas fourni.

| DONNÉES COMMUNES - V09 - ESSAI SPATIAL, PAS UN PLAN DE MONTAGE VALIDÉ   |                                              |                                                                  |
|---|----------------------------------------------|------------------------------------------------------------------|
| Le PDF et la maquette lisent le même fichier implantation.json : positions E1/P1/DJ, dimensions principales, trajet artiste, bar, poteaux et 42 appareils repérés. Le repère de géométrie est identique dans les deux livrables. Cette concordance ne remplace pas un relevé architectural. |                                              |                                                                  |
|   |                                              |                                                                  |
|   |                                              |                                                                  |
| Élément   | Repères communs en mètres                    | Niveau de validation                                             |
| Scène / parterre   | 8,5344 x 3,6576 ; parterre 8,5344 x 10,668   | Dimensions nominales du dossier de salle                         |
| Écran E1   | x 2.75 ; y 0.00 ; z 2.55 ; diamètre 1.50     | Proposé : suspension et visibilité à valider                     |
| Projecteur P1   | x 2.57 ; y -2.58 ; z 3.00                    | Enveloppe indicative ; lentille et support inconnus              |
| DJ   | x -3.00 ; y 1.80 ; table 1,80 x 0,75         | Proposé ; dégagement mur 0,367 m                                 |
| Bar / poteaux   | Mêmes volumes indicatifs dans les deux vues  | Aucun relevé coté disponible ; collisions réelles non garanties  |
| Lumières   | 36 repérées existantes + 6 PAR proposés = 42 | Positions reprises graphiquement ; accroches réelles à conserver |

| CALCUL DE COUVERTURE - IDENTIFIER LA LENTILLE AVANT DE FIXER LE REcul   |
|---|
| Cercle de 1,50 m : gabarit 16:10 de 2,432 x 1,52 m : image visible masquée Ø 1,48 m sur écran Ø 1,50 m, bord noir intérieur de 1 cm. Réserve native pour réglage, sans halo extérieur. Diagonale = sqrt(2,432² + 1,52²) / 0,0254 = 112.911 pouces. Le cercle n’est pas la diagonale du rectangle.   |
| ET-DLE085 : Lmin = D x 0,0174 - 0,0471 = 1.918 m ; Lmax = D x 0,0216 - 0,0442 = 2.395 m.<br>ET-DLE170 standard : Lmin = D x 0,0379 - 0,0746 = 4.205 m ; Lmax = D x 0,0529 - 0,0725 = 5.900 m.   |
| Essai V09 : distance perpendiculaire du repère lentille indicatif à E1 = 2,58 - 0,28 = 2,30 m. Dans la plage ET-DLE085, hors plage standard. Décentrement latéral 0,18 m et vertical 0,44 m à contrôler avec la lentille et son repère réel. Depuis V08 : E1 +5 cm à droite ; P1 +2 cm à droite et +3 cm vers le fond.   |
| La salle ne nomme pas sa lentille. Elle décrit une installation ultra-courte à 5 pieds d'un écran 150 pouces. Cela ne confirme ni ET-DLE085 ni ET-DLE170. Les rayons V09 montrent le gabarit à obtenir, pas le trajet optique réel. Bar et poteaux approximatifs. Gabarit complet à seulement 1 cm du bar en plan ; boîtier à 18,5 cm du comptoir et 6 cm du poteau. Marges trop faibles pour valider sur des cotes estimées. Ne pas monter à partir de ces seuls tracés. |
| Source de calcul : Panasonic PT-RZ770 Spec File, page 15, tableau 16:10 (mars 2020). Contrôle sur place requis : lentille, recul et décentrements, refroidissement, structure porteuse, cotes du bar et visibilité de l’écran.   |