


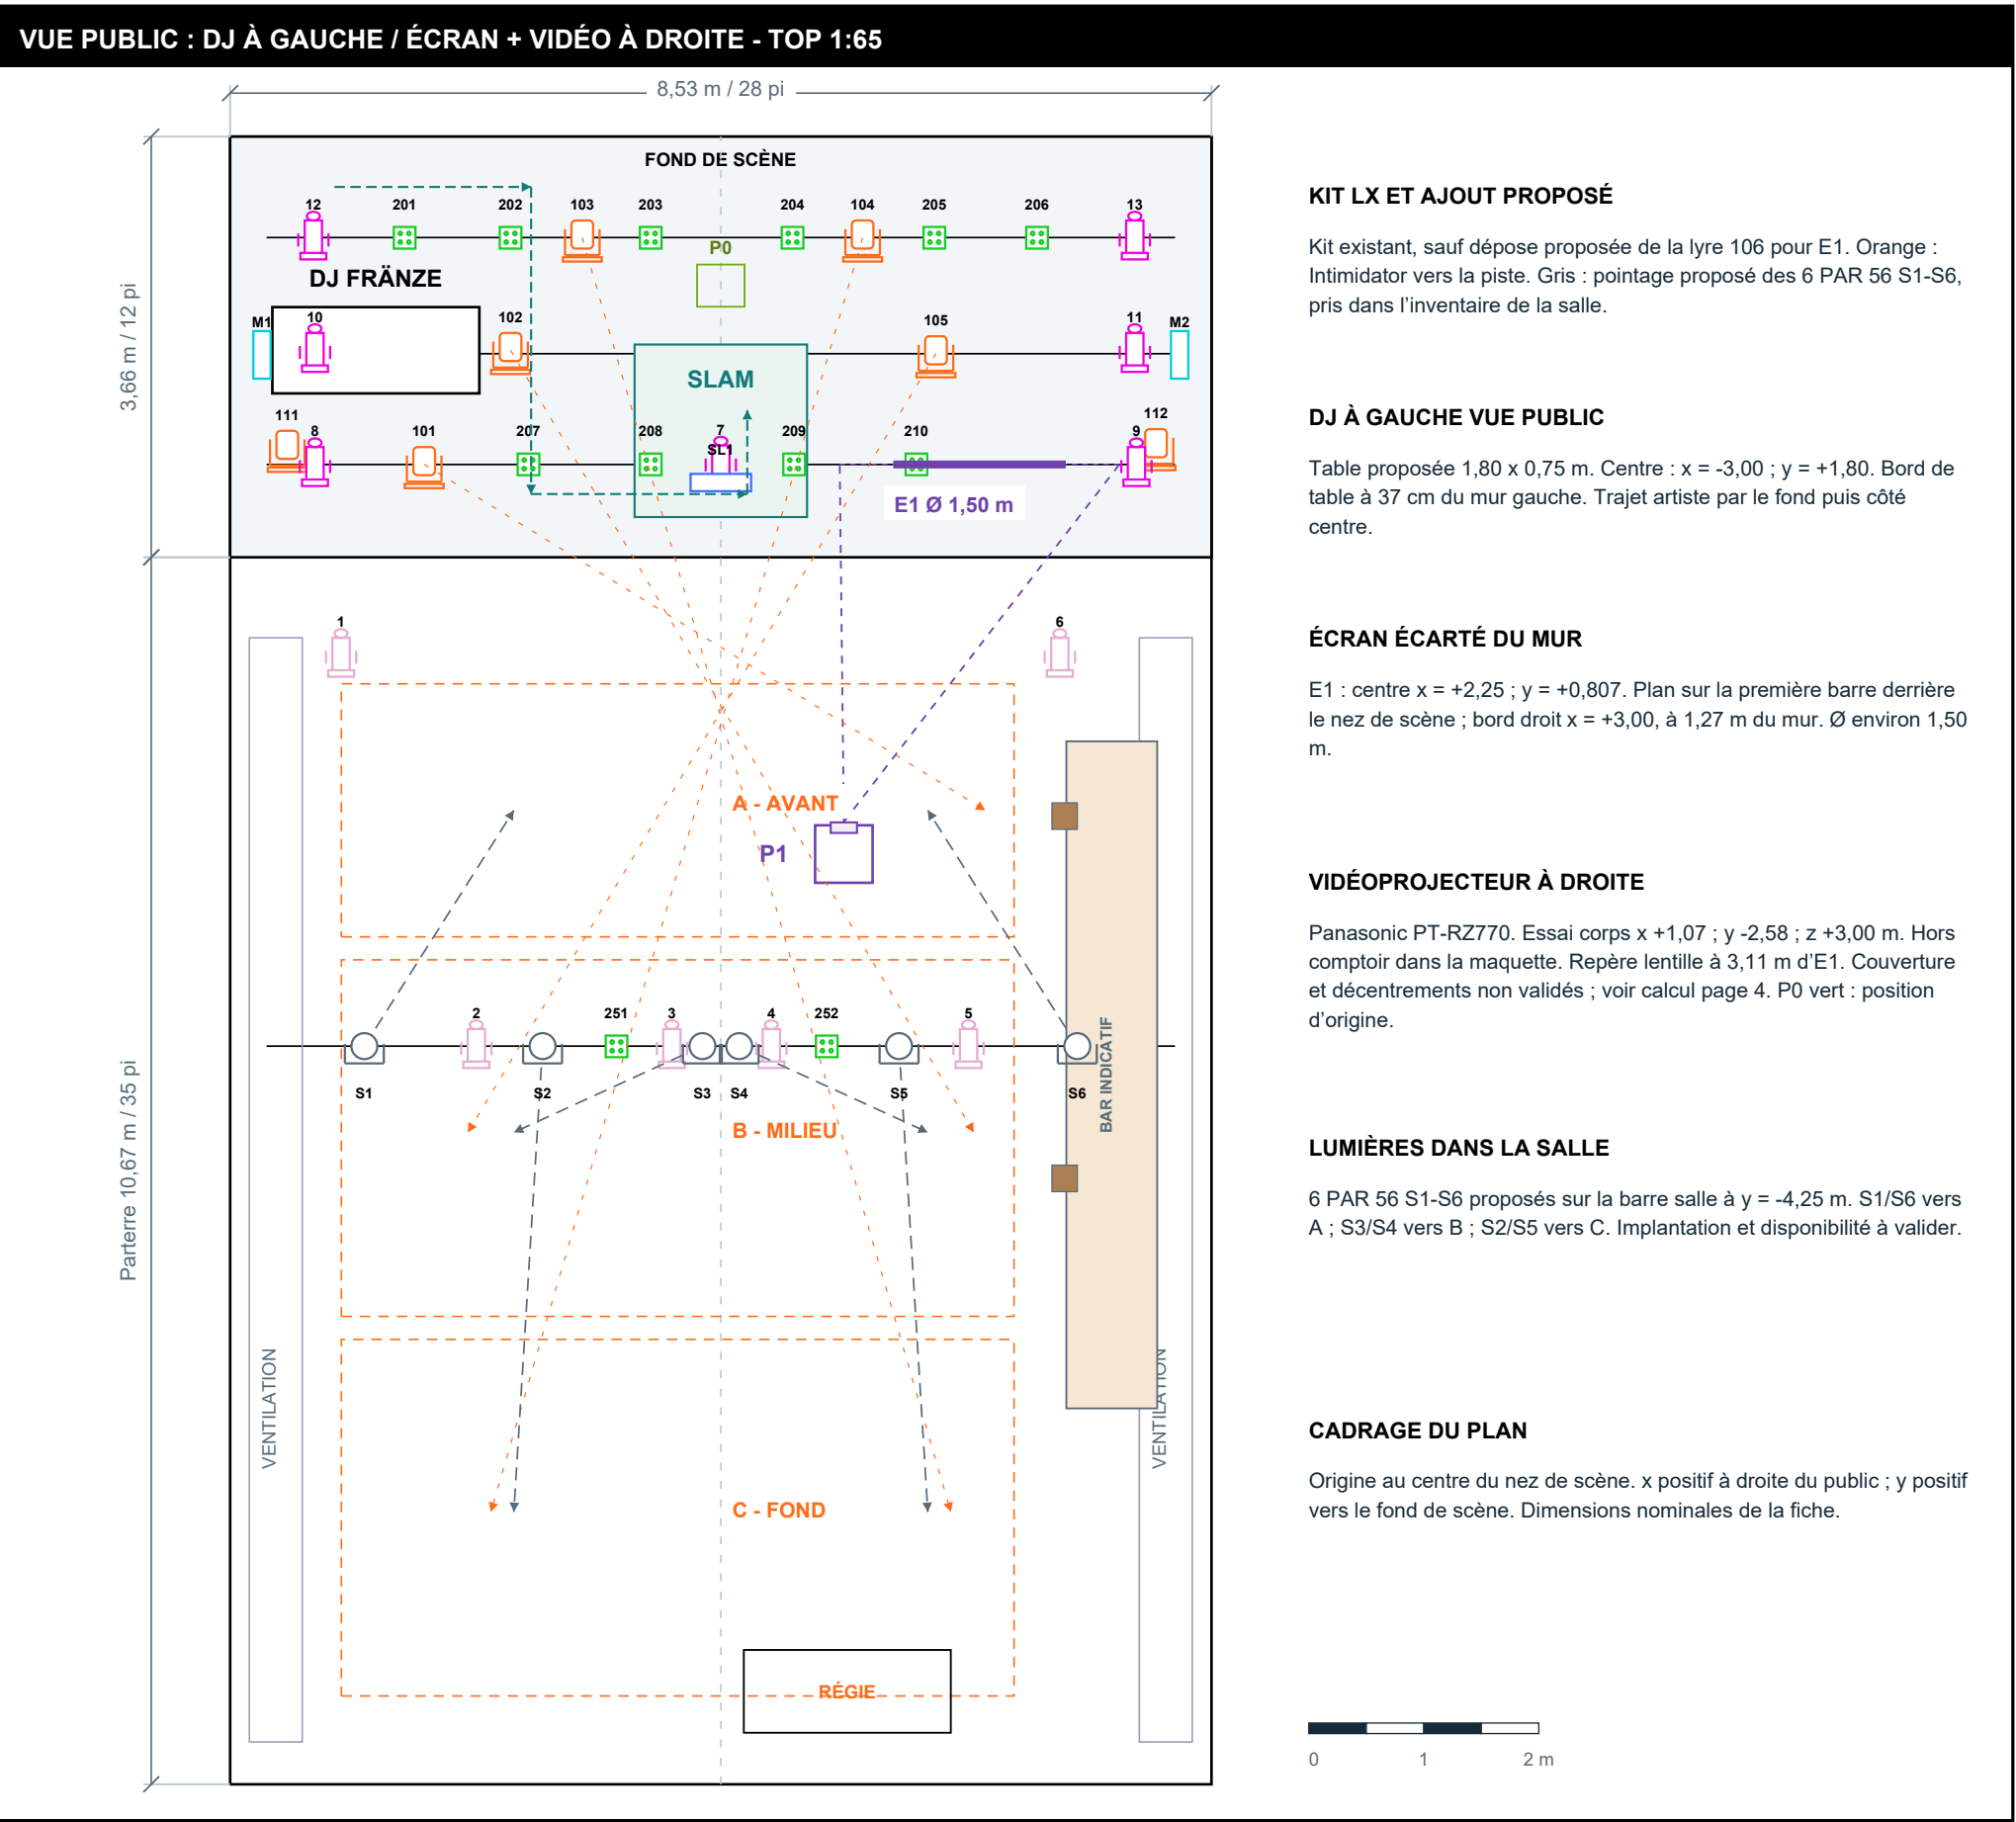


LÉGENDE - APPAREILS DU MINISTÈRE			
Symbole	Appareil	Qté	DMX
	ETC Source Four 36°	8*	1
	ETC Source Four 25/50 Zoom	6	1
	Colorado 1 Tour-Tri	12	ARC1 / 3
	Intimidator Spot 375Z	8	15
	DMG SL1 Mix 200 W	1	4**
	DMG Mini Mix 100 W	2	4**
	PAR 56 WFL 500 W	6*	1
* Source Four 36° : 8 inventoriés, 7 dessinés. PAR 56 : S1-S6 = emplacements proposés, à valider. ** Modes repris du plan LX ; conserver le patch.			

IMPLANTATION DEMANDÉE - REPÈRES	
E1 : écran suspendu Ø 1,50 m à l'avant droit, sur la première barre, à 0,807 m derrière le nez de scène. Bord droit à 1,27 m du mur droit. Bas proposé +1,30 m, haut +2,80 m / sol salle.	
P1 : essai x +1,07 ; y -2,58 ; z +3,00 m. Enveloppe indicative de 0,50 x 0,50 m, à 1,685 m du bord du comptoir modélisé. Lentille indicative à 3,11 m de l'écran. Lentille réelle, décentremments et accroche non validés.	
Piste : 6 PAR 56 proposés dans la salle pour une base fixe graduable, complétée par les 7 Intimidator actifs (106 déposé proposé). Les PAR ne sont pas attestés libres ou déjà installés à ces positions.	

CARTOUCHE ET BASE DU PLAN	
DT : Rémi LeGresley - Le Ministère Base : dossier Audio-LX fourni + plan LX 2023 envoyé par Rémi. Statut : implantation et pointages proposés. Emplacements LX repris graphiquement ; 106 déposé proposé. Accroches E1/P1 à valider.	

FRONT - VUE DEPUIS LE PUBLIC - 1:50

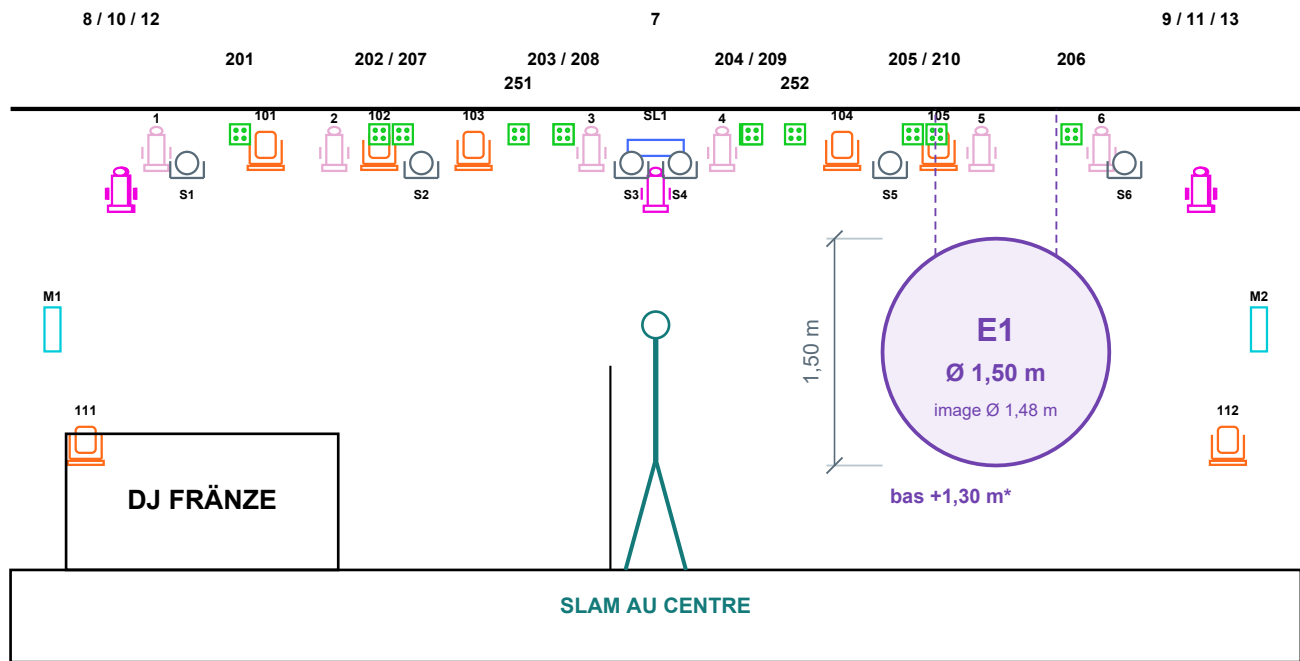


E1 écarté du mur droit. * Hauteur proposée ; à régler avec l'optique, la visibilité et les accroches.

LEFT - COUPE SUR E1, À DROITE VUE PUBLIC - 1:65

P1 est une proposition de repositionnement. La fiche décrit l'installation existante à 5 pi (1,52 m) de son écran 150 pouces. Dans V13 : corps à 2,58 m, repère de lentille indicatif à 3,11 m. La lentille de la salle est inconnue : essai spatial, non validé optiquement.

Trajet vidéo schématique : la lentille ultra-courte peut imposer un décalage et un trajet différents. Le repère de mesure du recul, la hauteur du corps et l'accroche finale restent à fixer après identification de la lentille.

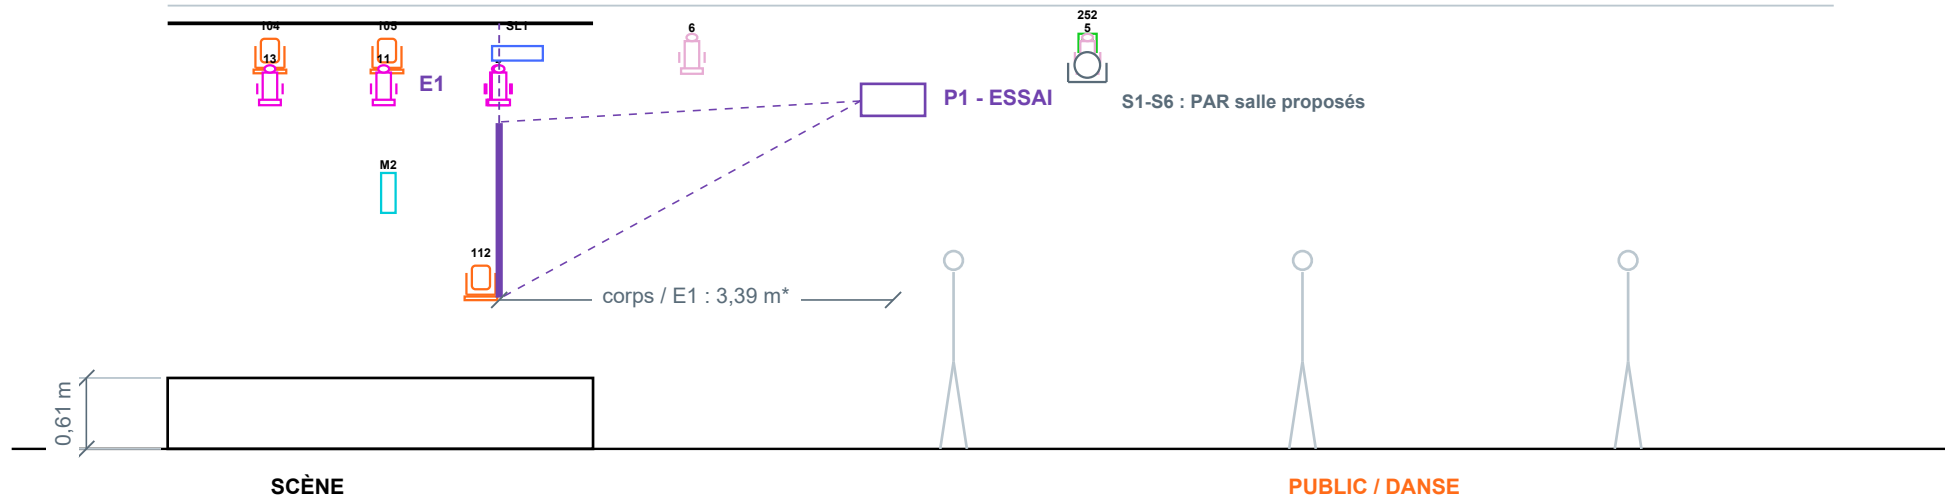

LÉGENDE - APPAREILS DU MINISTÈRE


Symbole	Appareil	Qté	DMX
	ETC Source Four 36°	8*	1
	ETC Source Four 25/50 Zoom	6	1
	Colorado 1 Tour-Tri	12	ARC1 / 3
	Intimidator Spot 375Z	8	15
	DMG SL1 Mix 200 W	1	4**
	DMG Mini Mix 100 W	2	4**
	PAR 56 WFL 500 W	6*	1

* Source Four 36° : 8 inventoriés, 7 dessinés.
PAR 56 : S1-S6 = emplacements proposés, à valider.
** Modes repris du plan LX ; conserver le patch.

NOTES TECHNIQUES DE MONTAGE

- Kit existant. Conserver les positions et le patch, sauf dépose proposée de la lyre 106 pour l'accroche E1. Les PAR S1-S6 sont une proposition complémentaire avec du matériel inventorié, non une implantation existante confirmée.
- Écran E1. Ø environ 1,50 m, suspendu à l'avant droit, écarté du mur vue public. Plan de l'écran sur la première barre (y = +0,807) ; bord droit à 1,27 m du mur. Suspension et sécurité secondaire à définir par le DT.
- Lumières dans la salle. Proposer S1-S6 sur la barre transversale existante, à 4,25 m du nez de scène. Vérifier place disponible, charge, accroches, gradateurs et disponibilité des PAR. Puissance totale : 6 x 500 W = 3 kW.
- Projection. PT-RZ770 et Chief VCMU documentés. Lentille installée non nommée : ne pas appliquer le ratio du zoom standard à l'installation ultra-courte. P1 hors du bar modélisé. Repère lentille à 3,11 m de l'écran, hors plage ET-DLE085 pour ce gabarit ; optique et décentremments à revalider. Lentille de la salle inconnue.
- Public dansant. PAR : base fixe graduable. Intimidator : effets complémentaires, pan/tilt limités autour d'E1. Régler l'éblouissement et la couverture au fond.
- Accroches. Aucun appareil sur les rails à rideaux. Points approuvés par la salle uniquement. Le 8e Source Four 36° reste non localisé.

ISOMÉTRIE DE REPÉRAGE - SANS ÉCHELLE - IMPLANTATION PROPOSÉE

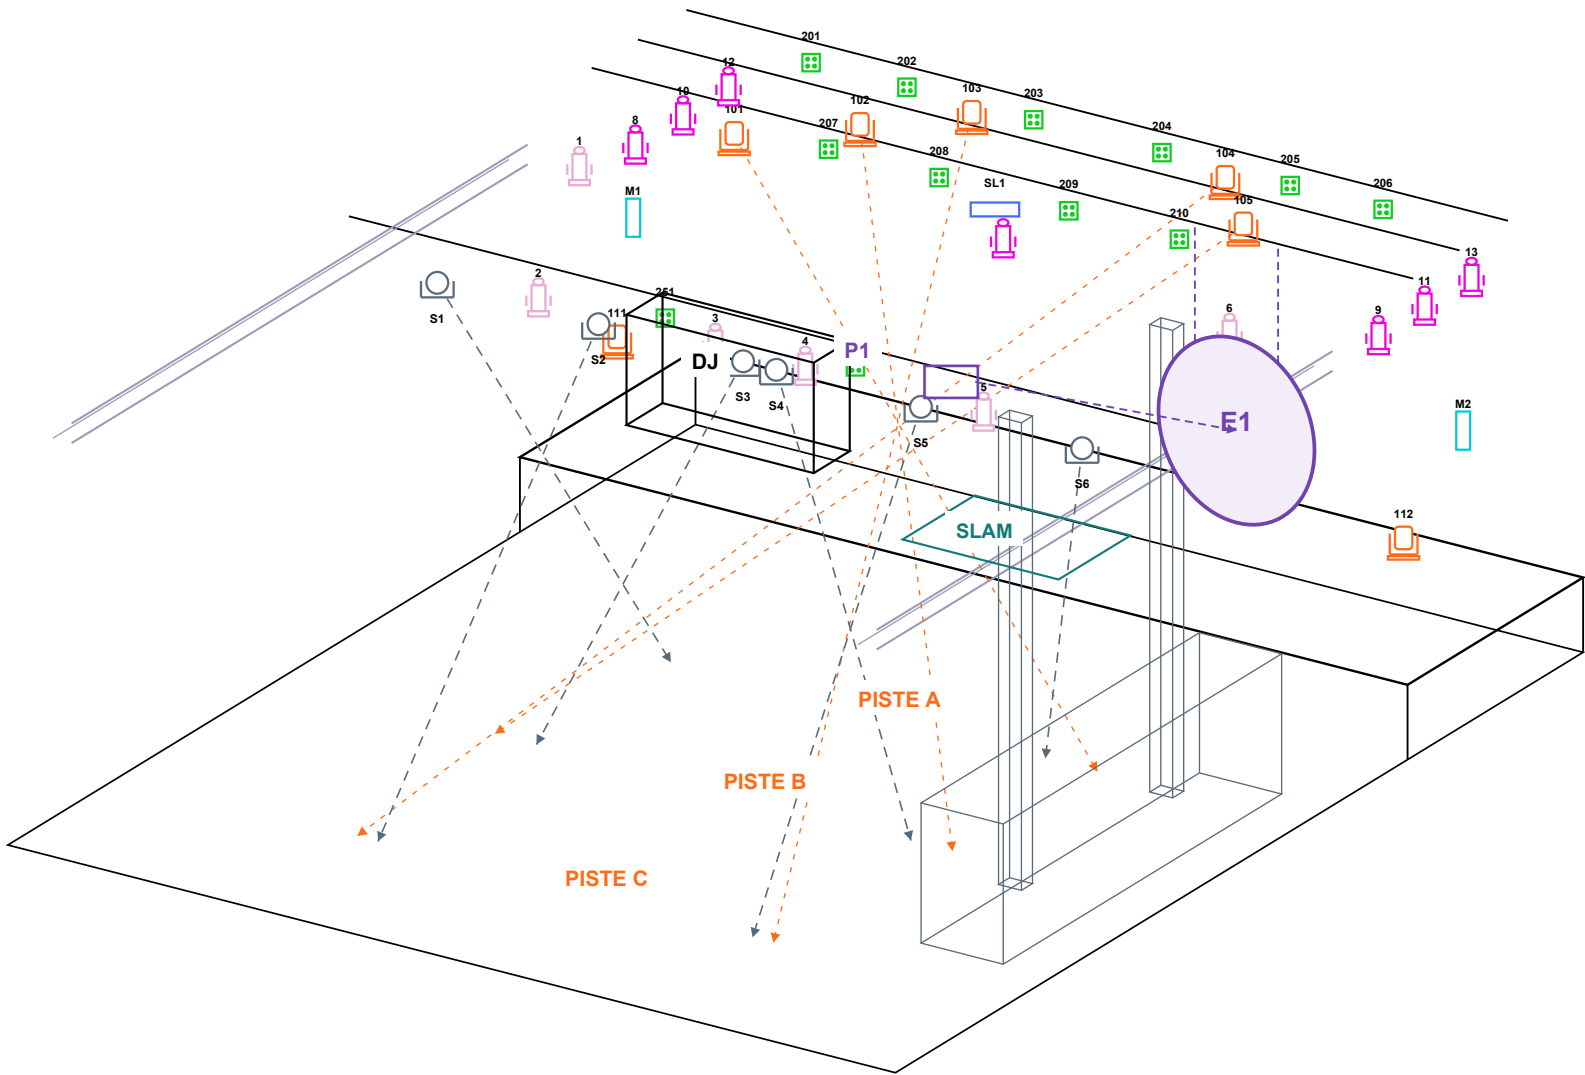

S1-S6 : 6 PAR proposés au-dessus de la piste. 106 : dépose proposée pour E1 ; autres points conservés.

COTES À REPORTER ET RÉGLAGES POUR LE DT

Élément	Cote / destination	Application
E1 - écran	x +2,25 ; y +0,807 ; Ø 1,50 m	Bord droit x +3,00 ; mur à 1,27 m. Bas proposé +1,30 m / sol salle.
P1 - vidéo	x +1,07 ; y -2,58 ; z +3,00 m	Hors comptoir modélisé. Repère lentille à 3,11 m. Optique, décentrement et support non validés.
DJ / slam	DJ : x -3,00 ; y +1,80. Slam : x 0 ; y +1,10.	Table 1,80 x 0,75 m ; mur gauche à 37 cm. Passage artiste derrière puis côté centre.
PAR S1-S6	y -4,25 ; x -3,10 / -1,55 / -0,16 / +0,16 / +1,55 / +3,10.	Hauteur de corps proposée +3,30 m. S1/S6 : A ; S3/S4 : B ; S2/S5 : C.

Sources : dossier Audio-LX du Ministère (dimensions, inventaire, support et installation vidéo) ; plan LX communiqué par Rémi ; spécifications Panasonic PT-RZ770. Les cotes du nouveau setup sont des propositions de conception, pas un relevé de l'existant.

ÉQUIPEMENTS TECHNIQUES LX - FICHE SALLE

Appareil	Qté	Donnée principale
Colorado 1 Tri Tour	12	LED RGB / ARC1
Intimidator Spot 375Z	8	5 suspendus + 2 bas ; 106 déposé
Source Four 25-50°	6	750 W / TL3
Source Four 36°	8	575 W / 7 dessinés
DMG SL1 Mix	1	200 W
DMG Mini Mix	2	100 W
PAR 56 WFL	6	500 W / S1-S6 proposés

Commande : GrandMA3 Command Wing Compact sur PC.
Gradateurs : 4 Lite-Putter DX-1210.
Distribution DMX : 1 Chauvet Data Stream 4.
Brouillard : Antari F-1W, usage à convenir.
Complément : conserver l'éclairage général de salle pour accueil et circulation.

VIDÉOPROJECTION - DONNÉES DOCUMENTÉES

Panasonic PT-RZ770
Laser DLP ; 7 000 lumens nominaux.
Résolution native : 1920 x 1200, 16:10.
HDMI disponible ; câble annoncé par Rémi.

Installation décrite par la salle :
Support Chief VCMU ; ultra short throw ; à 5 pi (1,52 m) de l'écran existant 16:9 de 150 pouces.

Écran de ce projet : cercle Ø 1,50 m. Prévoir un masque circulaire. Gabarit V13 : 2,432 x 1,52 m avant masque, image visible Ø 1,48 m, bord noir intérieur de 1 cm. Réserve native pour réglage du masque.

À relever : référence de lentille et repère exact des 5 pi. Le modèle est connu ; le ratio de l'optique installée n'est pas fourni.

DONNÉES COMMUNES - V13 - ESSAI SPATIAL, PAS UN PLAN DE MONTAGE VALIDÉ		
Le PDF et la maquette lisent le même fichier implantation.json : positions E1/P1/DJ, dimensions principales, trajet artiste, bar, poteaux et 41 appareils actifs, 106 déposé proposé. Le repère de géométrie est identique dans les deux livrables. Cette concordance ne remplace pas un relevé architectural.		
Élément	Repères communs en mètres	Niveau de validation
Scène / parterre	8,5344 x 3,6576 ; parterre 8,5344 x 10,668	Dimensions nominales du dossier de salle
Écran E1	x 2.25 ; y 0.81 ; z 2.05 ; diamètre 1.50	Proposé : suspension et visibilité à valider
Projecteur P1	x 1.07 ; y -2.58 ; z 3.00	Enveloppe indicative ; lentille et support inconnus
DJ	x -3.00 ; y 1.80 ; table 1,80 x 0,75	Proposé ; dégagement mur 0,367 m
Bar / poteaux	Mêmes volumes indicatifs dans les deux vues	Aucun relevé coté disponible ; collisions réelles non garanties
Lumières	35 existants actifs + 6 PAR proposés = 41	Positions reprises graphiquement ; accroches réelles à conserver

CALCUL DE COUVERTURE - IDENTIFIER LA LENTILLE AVANT DE FIXER LE REcul
Cercle de 1,50 m : gabarit 16:10 de 2,432 x 1,52 m : image visible masquée Ø 1,48 m sur écran Ø 1,50 m, bord noir intérieur de 1 cm. Réserve native pour réglage, sans halo extérieur. Diagonale = sqrt(2,432² + 1,52²) / 0,0254 = 112.911 pouces. Le cercle n’est pas la diagonale du rectangle.
ET-DLE085 : Lmin = D x 0,0174 - 0,0471 = 1.918 m ; Lmax = D x 0,0216 - 0,0442 = 2.395 m. ET-DLE170 standard : Lmin = D x 0,0379 - 0,0746 = 4.205 m ; Lmax = D x 0,0529 - 0,0725 = 5.900 m.
Essai V13 : distance perpendiculaire du repère lentille indicatif à E1 = 2,58 - 0,28 + 0,807 = 3,11 m. Hors plage ET-DLE085 et hors plage standard pour ce gabarit. Optique à revalider. Décentrement latéral 1,18 m et vertical 0,94 m à contrôler avec la lentille et son repère réel. Depuis V12 : E1 reculé de 0,807 m sur la première barre et abaissé de 0,50 m. P1 conservé. Lyre 106 déposée dans cette proposition pour dégager l'accroche. Bordure noire de 1 cm conservée.
La salle ne nomme pas sa lentille. Elle décrit une installation ultra-courte à 5 pieds d’un écran 150 pouces. Cela ne confirme ni ET-DLE085 ni ET-DLE170. Les rayons V13 montrent le gabarit à obtenir, pas le trajet optique réel. Bar et poteaux approximatifs. Gabarit complet à environ 1,13 m du bar en plan ; boîtier à 1,685 m du comptoir et 1,56 m du poteau. Contrôle géométrique de maquette, sans validation des cotes réelles. Ne pas monter à partir de ces seuls tracés.
Source de calcul : Panasonic PT-RZ770 Spec File, page 15, tableau 16:10 (mars 2020). Contrôle sur place requis : lentille, recul et décentrement, refroidissement, structure porteuse, cotes du bar et visibilité de l’écran.