


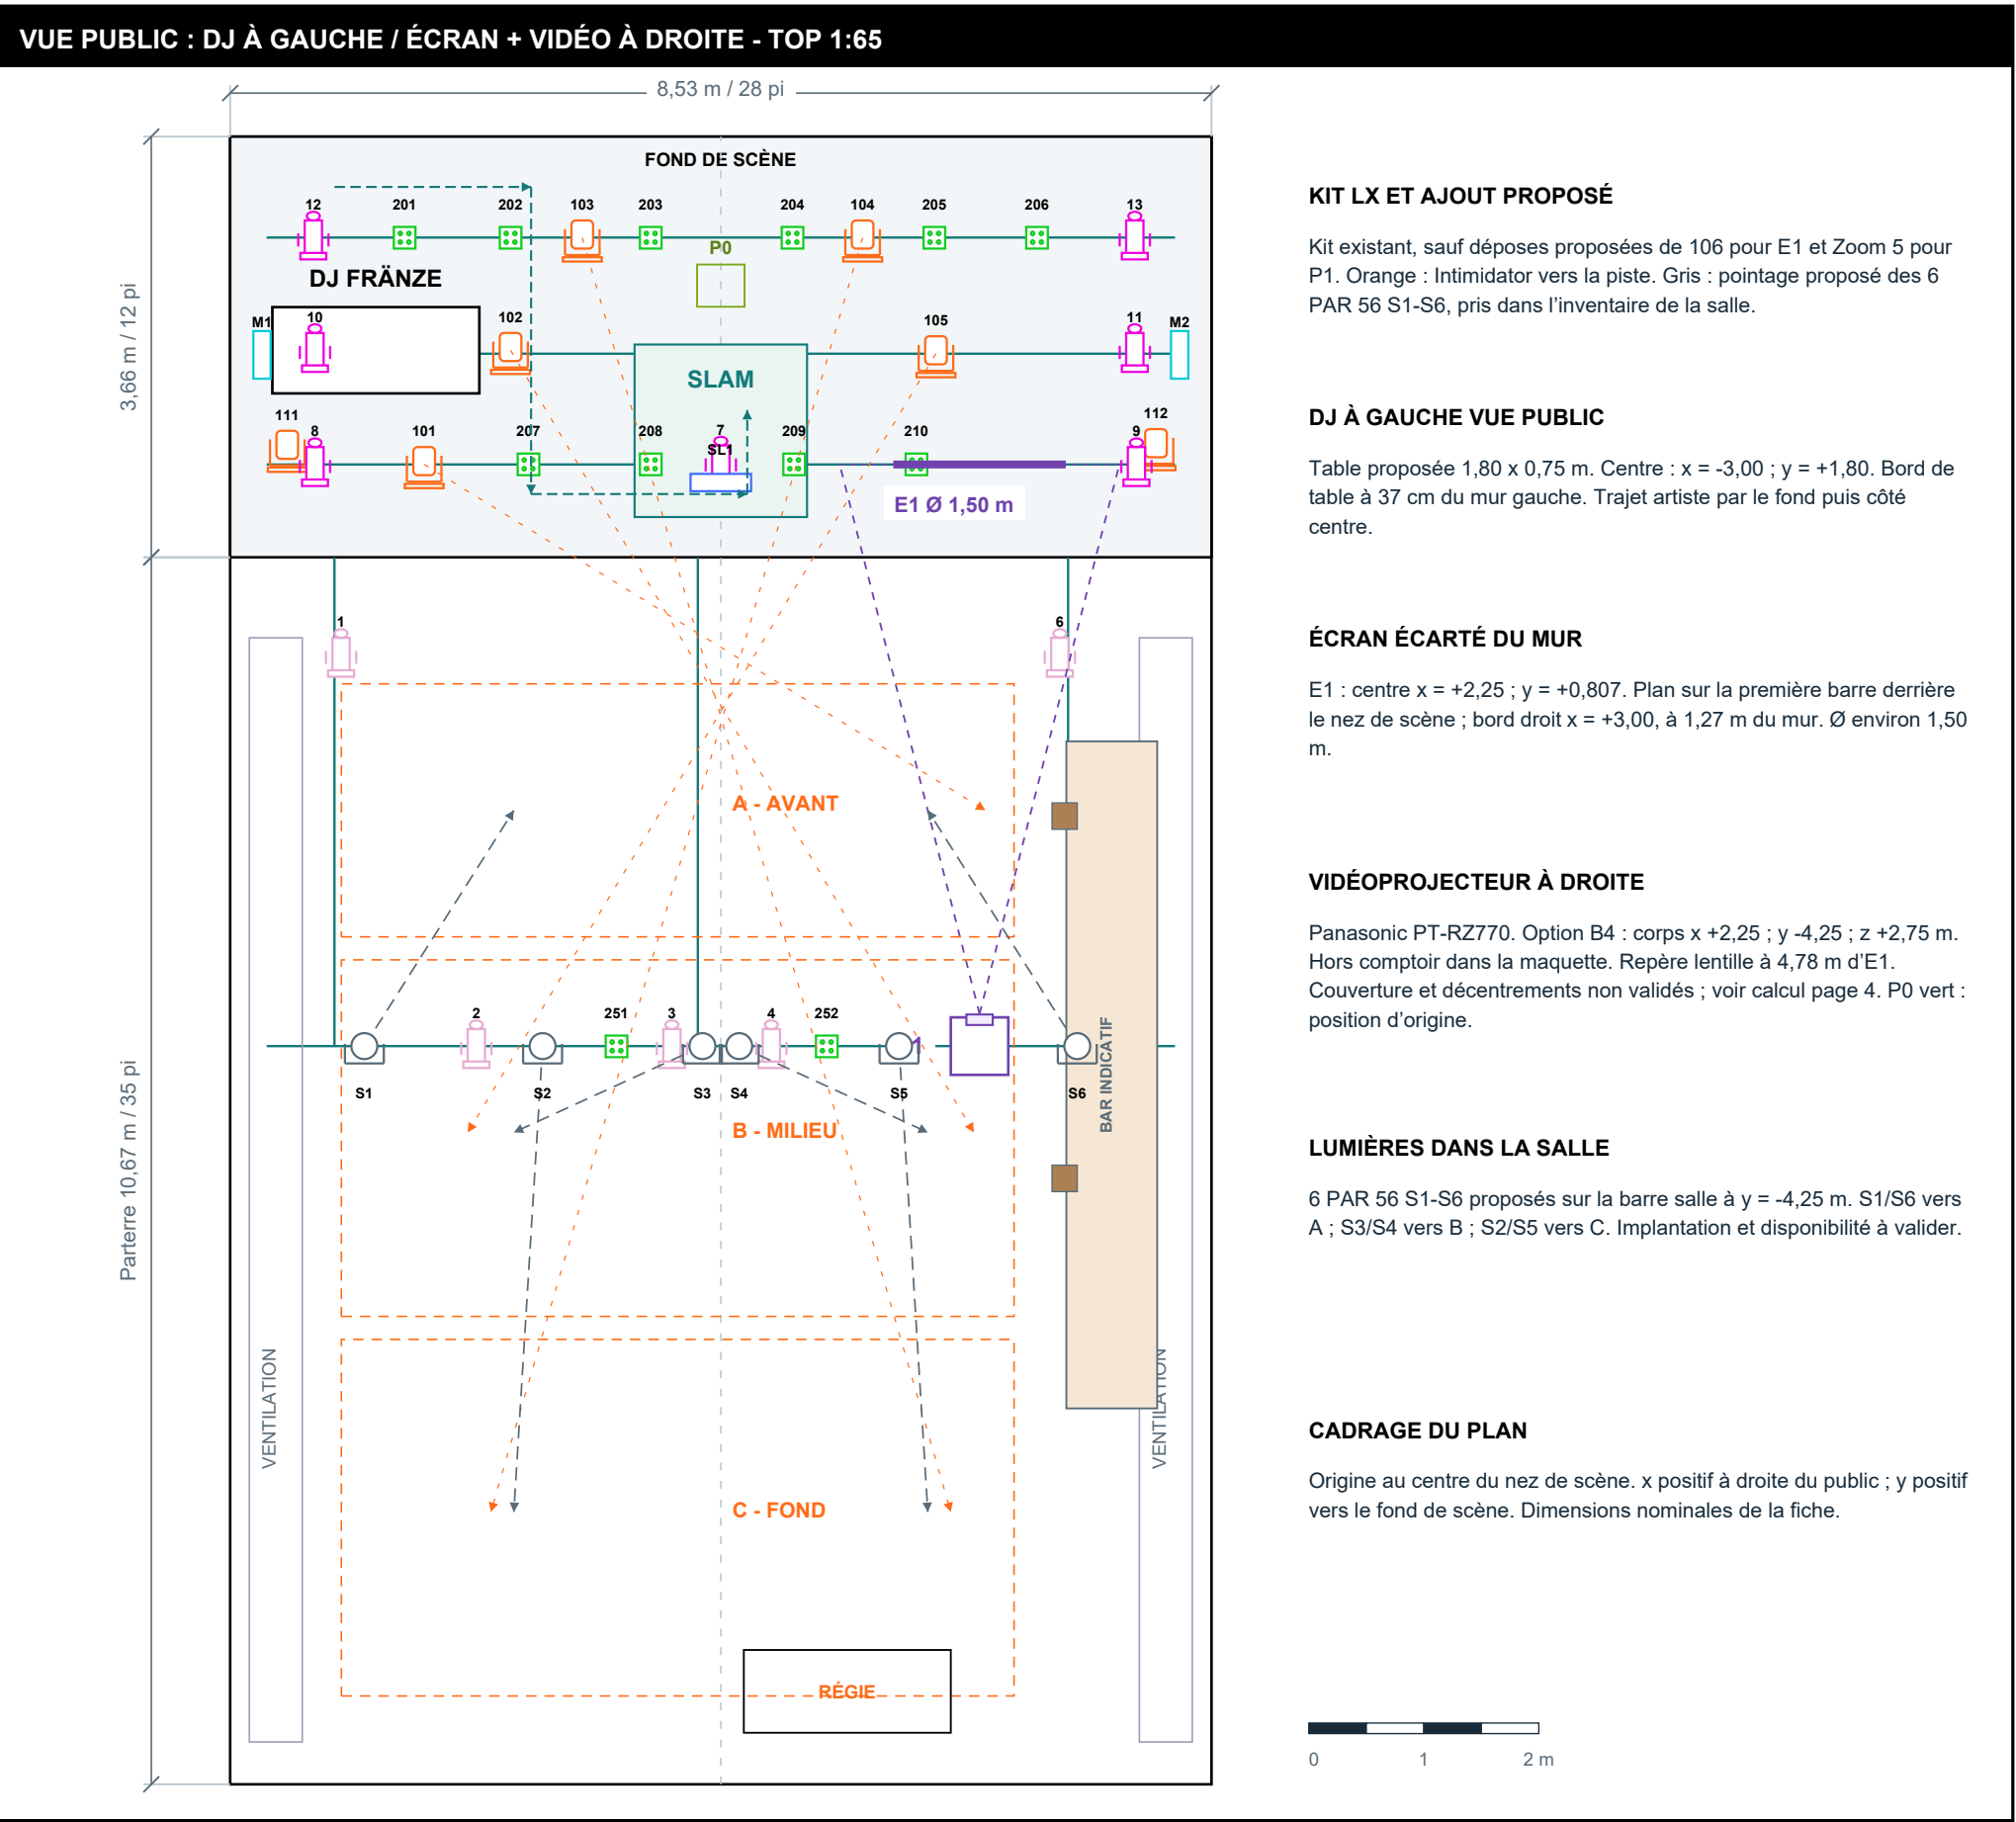

LÉGENDE - APPAREILS DU MINISTÈRE

Symbole	Appareil	Qté	DMX
	ETC Source Four 36°	8*	1
	ETC Source Four 25/50 Zoom	6	1
	Colorado 1 Tour-Tri	12	ARC1 / 3
	Intimidator Spot 375Z	8	15
	DMG SL1 Mix 200 W	1	4**
	DMG Mini Mix 100 W	2	4**
	PAR 56 WFL 500 W	6*	1

* Source Four 36° : 8 inventoriés, 7 dessinés.

PAR 56 : S1-S6 = emplacements proposés, à valider.

** Modes repris du plan LX ; conserver le patch.

IMPLANTATION DEMANDÉE - REPÈRES

E1 : écran suspendu Ø 1,50 m à l'avant droit, sur la première barre, à 0,807 m derrière le nez de scène. Bord droit à 1,27 m du mur droit. Bas proposé +1,30 m, haut +2,80 m / sol salle.

P1 : option B4 x +2,25 ; y -4,25 ; z +2,75 m. Enveloppe indicative de 0,50 x 0,50 m, à 0,505 m du bord du comptoir modélisé. Lentille indicative à 4,78 m de l'écran. Lentille réelle, décentrement et accroche non validés.


Piste : 6 PAR 56 proposés dans la salle pour une base fixe graduable, complétée par les 7 Intimidator actifs (106 déposé proposé). Les PAR ne sont pas attestés libres ou déjà installés à ces positions.

CARTOUCHE ET BASE DU PLAN

DT : Rémi LeGresley - Le Ministère

Base : dossier Audio-LX fourni + plan LX 2023 envoyé par Rémi.


Statut : implantation et pointages proposés. Emplacements LX repris graphiquement ; 106 et Zoom 5 déposés proposés. Accroches E1/P1 à valider.

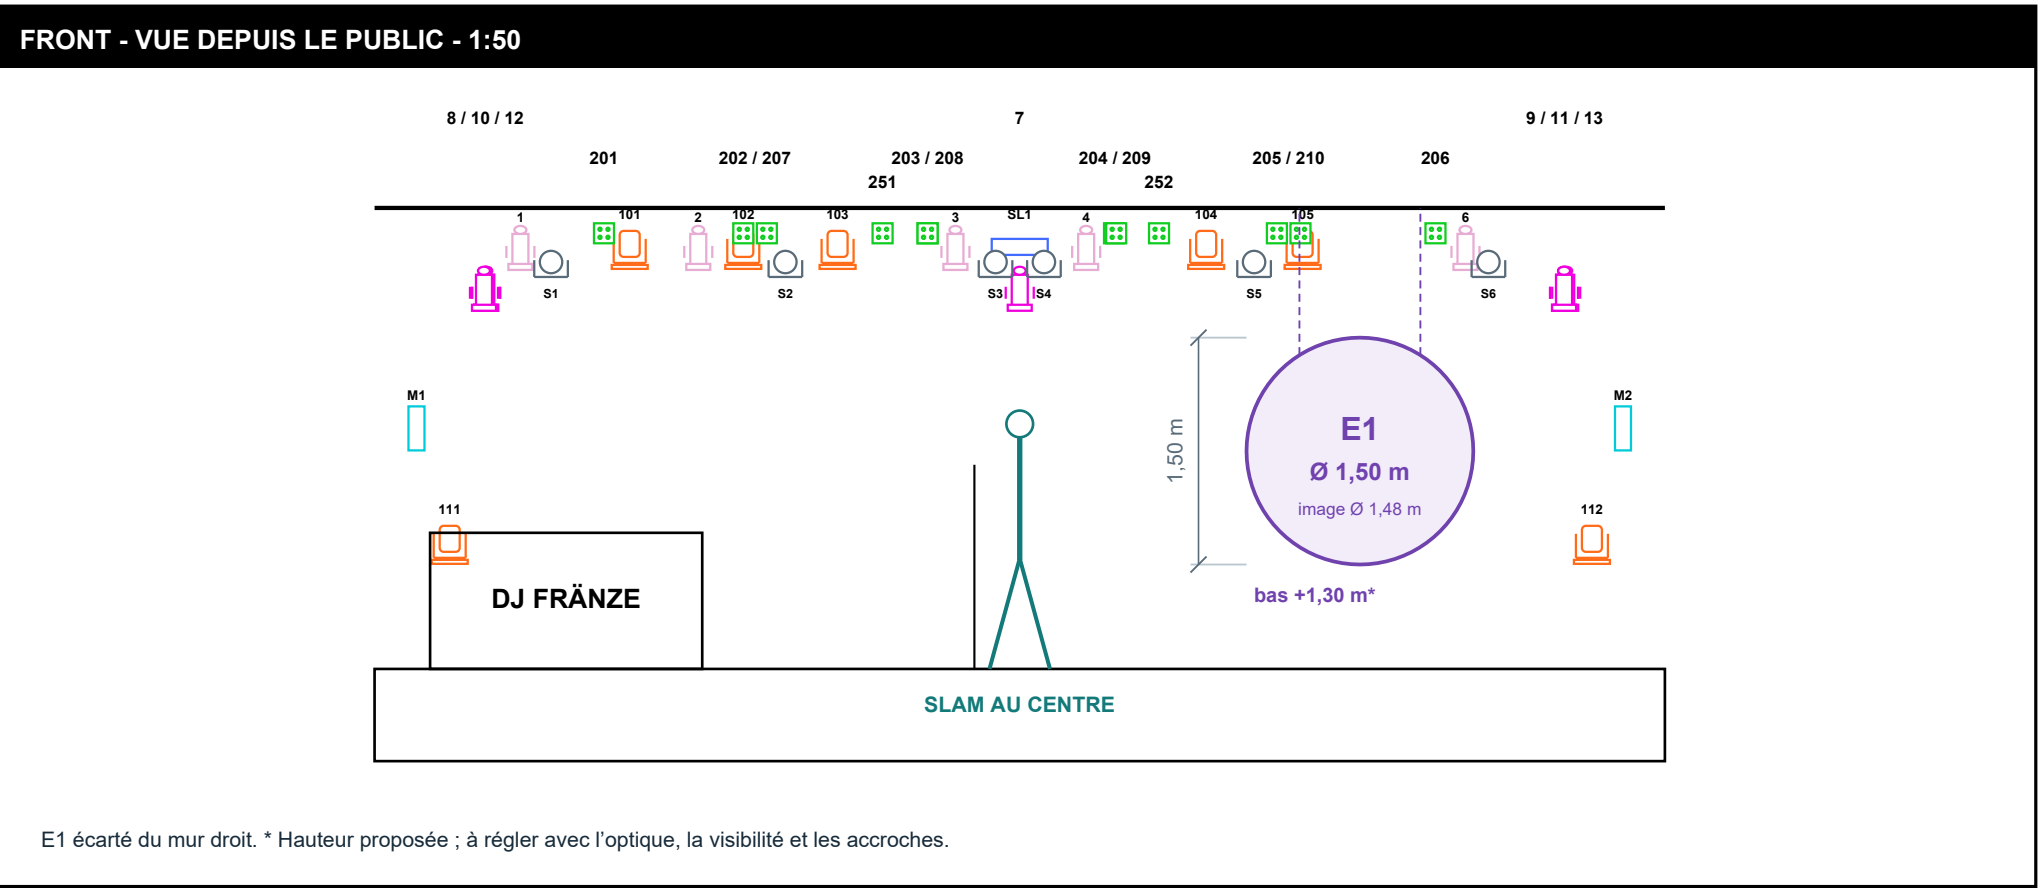

LÉGENDE - APPAREILS DU MINISTÈRE


Symbole	Appareil	Qté	DMX
	ETC Source Four 36°	8*	1
	ETC Source Four 25/50 Zoom	6	1
	Colorado 1 Tour-Tri	12	ARC1 / 3
	Intimidator Spot 375Z	8	15
	DMG SL1 Mix 200 W	1	4**
	DMG Mini Mix 100 W	2	4**
	PAR 56 WFL 500 W	6*	1

* Source Four 36° : 8 inventoriés, 7 dessinés.
PAR 56 : S1-S6 = emplacements proposés, à valider.
** Modes repris du plan LX ; conserver le patch.

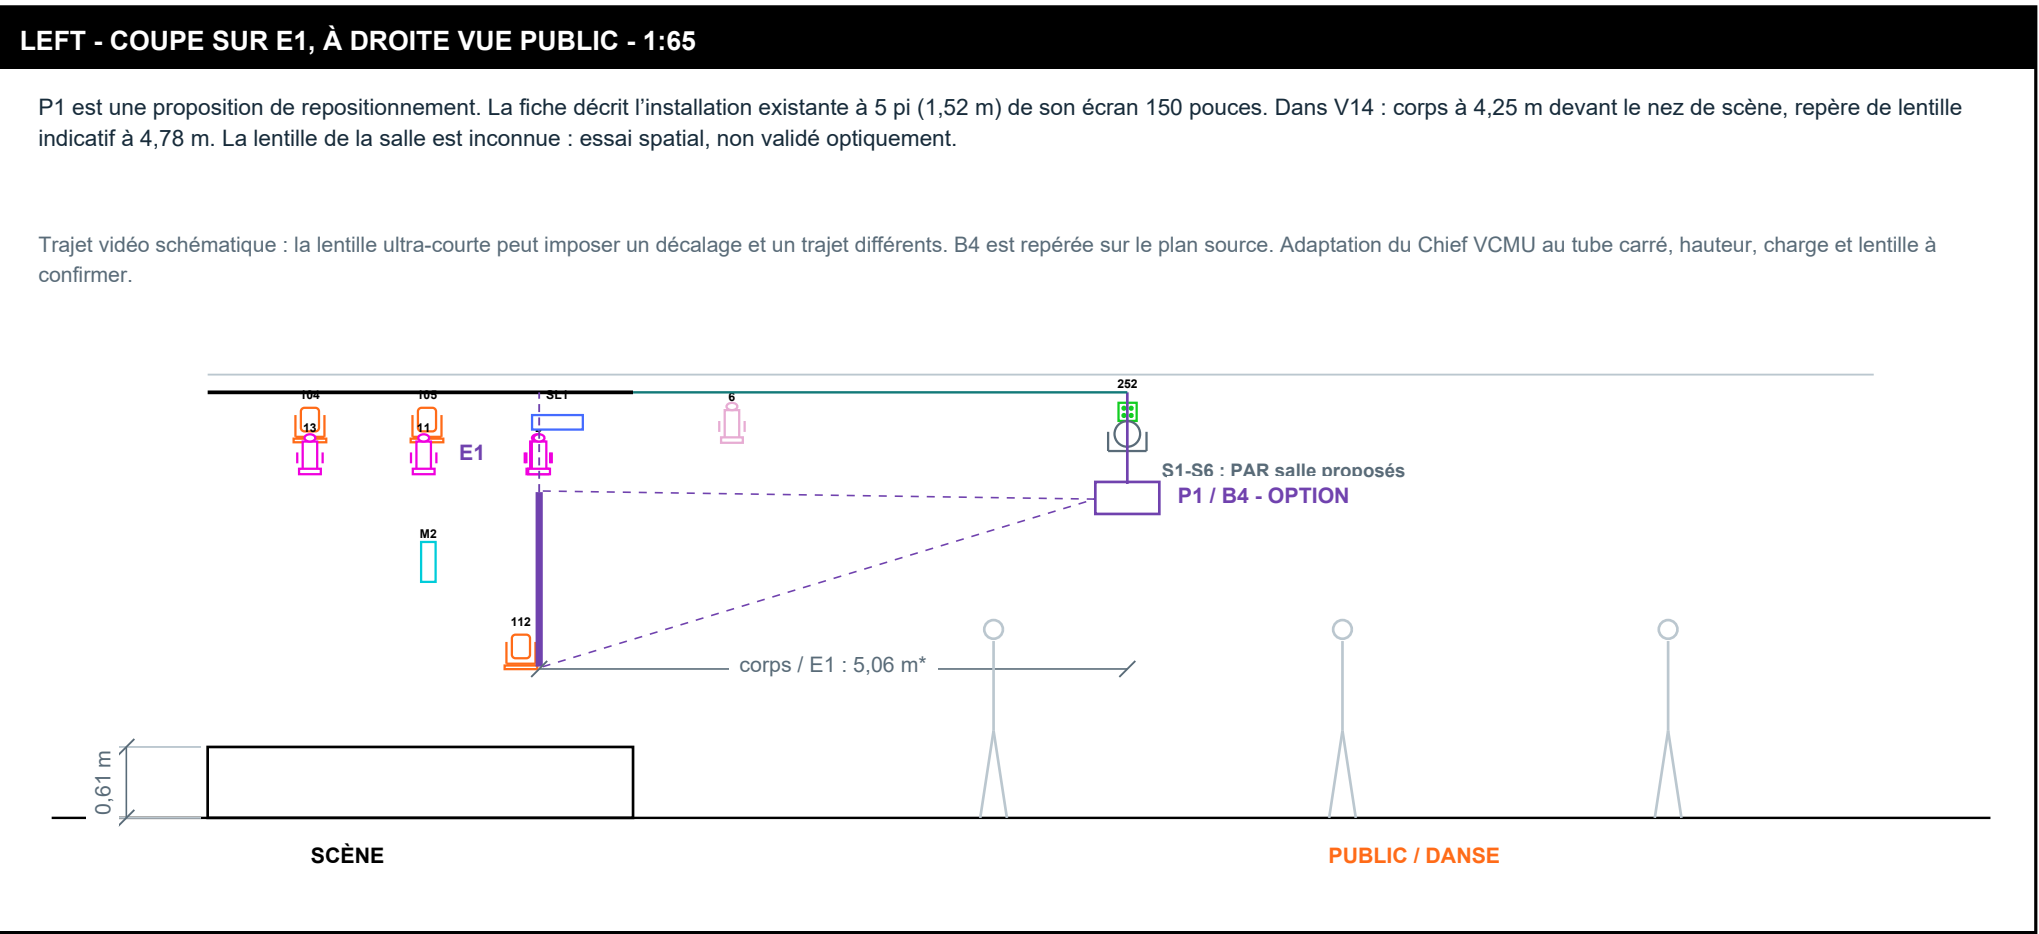

- NOTES TECHNIQUES DE MONTAGE
- Kit existant. Conserver les positions et le patch, sauf déposes proposées de 106 pour E1 et du Zoom 5 pour P1. Les PAR S1-S6 sont une proposition complémentaire avec du matériel inventorié, non une implantation existante confirmée.
 - Écran E1. Ø environ 1,50 m, suspendu à l'avant droit, écarté du mur vue public. Plan de l'écran sur la première barre (y = +0,807) ; bord droit à 1,27 m du mur. Suspension et sécurité secondaire à définir par le DT.
 - Lumières dans la salle. Proposer S1-S6 sur la barre transversale existante, à 4,25 m du nez de scène. Vérifier place disponible, charge, accroches, gradateurs et disponibilité des PAR. Puissance totale : 6 x 500 W = 3 kW.
 - Projection. PT-RZ770 et Chief VCMU documentés. Lentille installée non nommée : ne pas appliquer le ratio du zoom standard à l'installation ultra-courte. P1 hors du bar modélisé. Repère lentille à 4,78 m de l'écran, option sur B4 compatible en recul avec ET-DLE170 ; disponibilité et décentrement à vérifier. Lentille de la salle inconnue.
 - Public dansant. PAR : base fixe graduable. Intimidator : effets complémentaires, pan/tilt limités autour d'E1. Régler l'éblouissement et la couverture au fond.
 - Accroches. Aucun appareil sur les rails à rideaux. Points approuvés par la salle uniquement. Le 8e Source Four 36° reste non localisé.

ISOMÉTRIE DE REPÉRAGE - SANS ÉCHELLE - IMPLANTATION PROPOSÉE

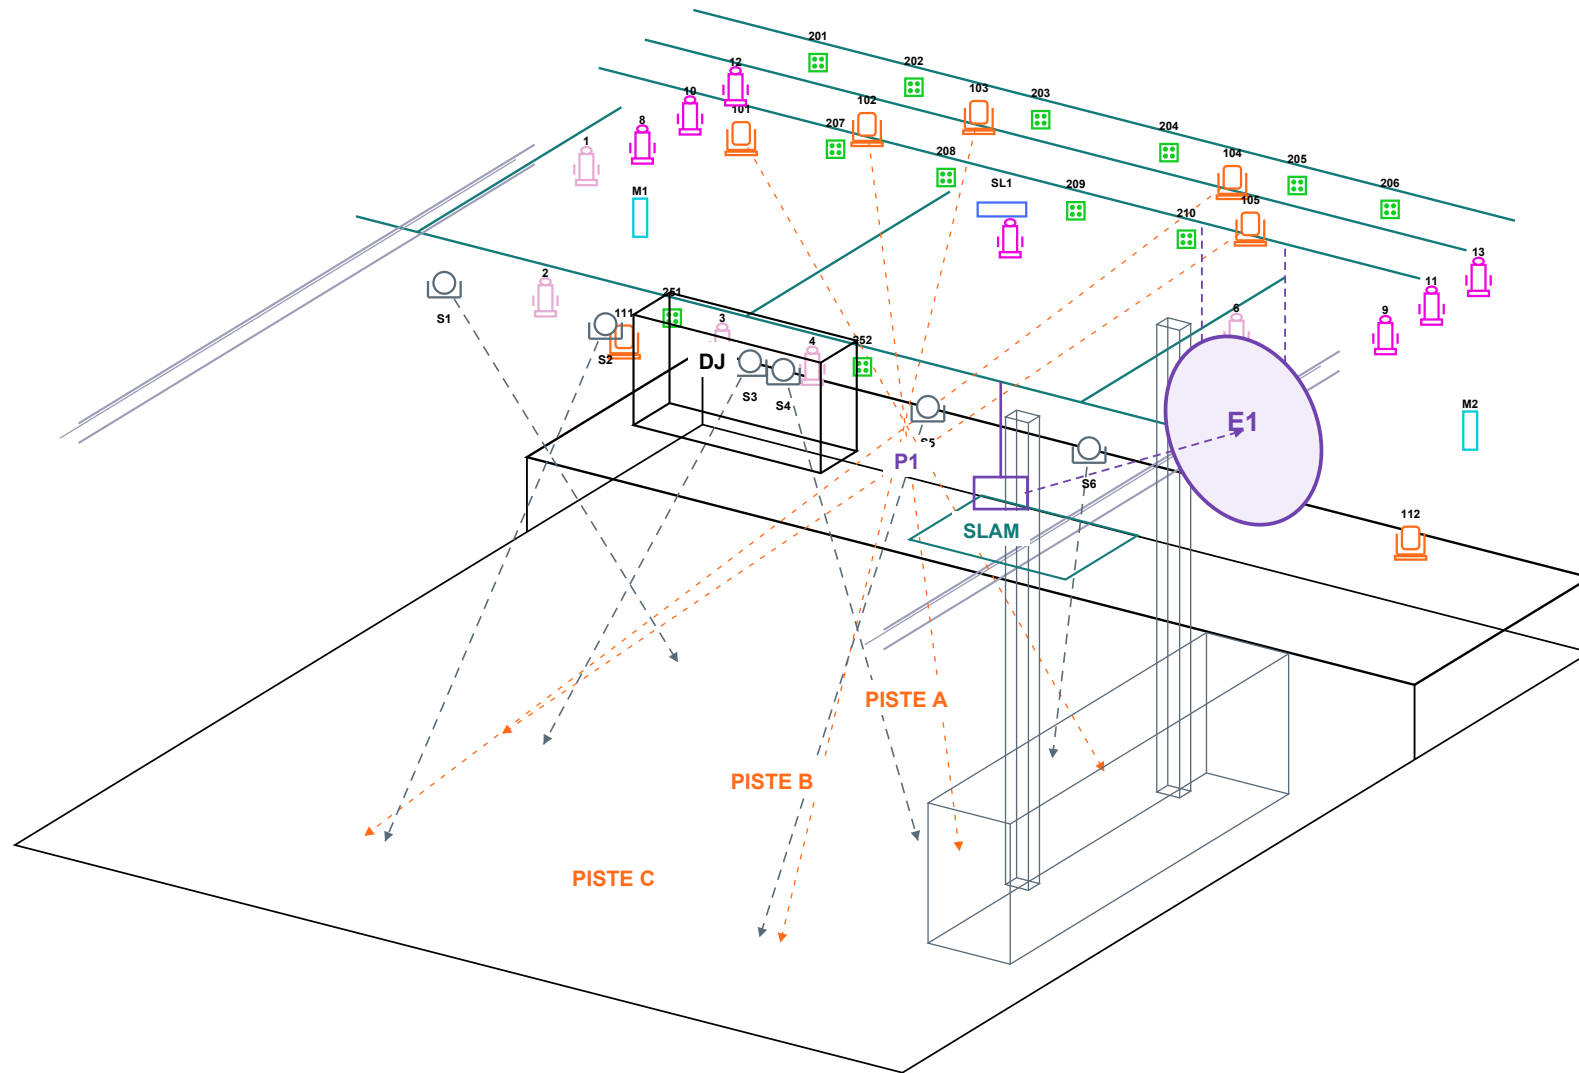

S1-S6 : 6 PAR proposés au-dessus de la piste. 106 et Zoom 5 : déposes proposées pour E1/P1 ; autres points conservés.

COTES À REPORTER ET RÉGLAGES POUR LE DT

Élément	Cote / destination	Application
E1 - écran	x +2,25 ; y +0,807 ; Ø 1,50 m	Bord droit x +3,00 ; mur à 1,27 m. Bas proposé +1,30 m / sol salle.
P1 - vidéo	x +2,25 ; y -4,25 ; z +2,75 m	Hors comptoir modélisé. Repère lentille à 4,78 m. Optique, décentrement et support non validés.
DJ / slam	DJ : x -3,00 ; y +1,80. Slam : x 0 ; y +1,10.	Table 1,80 x 0,75 m ; mur gauche à 37 cm. Passage artiste derrière puis côté centre.
PAR S1-S6	y -4,25 ; x -3,10 / -1,55 / -0,16 / +0,16 / +1,55 / +3,10.	Hauteur de corps proposée +3,30 m. S1/S6 : A ; S3/S4 : B ; S2/S5 : C.

Sources : dossier Audio-LX du Ministère (dimensions, inventaire, support et installation vidéo) ; plan LX communiqué par Rémi ; spécifications Panasonic PT-RZ770. Les cotes du nouveau setup sont des propositions de conception, pas un relevé de l'existant.

ÉQUIPEMENTS TECHNIQUES LX - FICHE SALLE

Appareil	Qté	Donnée principale
Colorado 1 Tri Tour	12	LED RGB / ARC1
Intimidator Spot 375Z	8	5 suspendus + 2 bas ; 106 déposé
Source Four 25-50°	6	5 actifs ; Zoom 5 déposé proposé
Source Four 36°	8	575 W / 7 dessinés
DMG SL1 Mix	1	200 W
DMG Mini Mix	2	100 W
PAR 56 WFL	6	500 W / S1-S6 proposés

Commande : GrandMA3 Command Wing Compact sur PC.
Gradateurs : 4 Lite-Putter DX-1210.
Distribution DMX : 1 Chauvet Data Stream 4.
Brouillard : Antari F-1W, usage à convenir.
Complément : conserver l'éclairage général de salle pour accueil et circulation.

VIDÉOPROJECTION - DONNÉES DOCUMENTÉES

Panasonic PT-RZ770
Laser DLP ; 7 000 lumens nominaux.
Résolution native : 1920 x 1200, 16:10.
HDMI disponible ; câble annoncé par Rémi.

Installation décrite par la salle :
Support Chief VCMU ; ultra short throw ; à 5 pi (1,52 m) de l'écran existant 16:9 de 150
pouces.

Écran de ce projet : cercle Ø 1,50 m. Prévoir un masque circulaire. Gabarit V14 : 2,432 x 1,52 m avant masque, image visible Ø 1,48 m, bord noir intérieur de 1 cm. Réserve native pour réglage du masque.

À relever : référence de lentille et repère exact des 5 pi. Le modèle est connu ; le ratio de l'optique installée n'est pas fourni.

DONNÉES COMMUNES - V14 - ESSAI SPATIAL, PAS UN PLAN DE MONTAGE VALIDÉ		
Le PDF et la maquette lisent le même fichier implantation.json : positions E1/P1/DJ, dimensions principales, trajet artiste, bar, poteaux et 40 appareils actifs ; 106 et Zoom 5 déposés proposés. Le repère de géométrie est identique dans les deux livrables. Cette concordance ne remplace pas un relevé architectural.		
Élément	Repères communs en mètres	Niveau de validation
Scène / parterre	8,5344 x 3,6576 ; parterre 8,5344 x 10,668	Dimensions nominales du dossier de salle
Écran E1	x 2.25 ; y 0.81 ; z 2.05 ; diamètre 1.50	Proposé : suspension et visibilité à valider
Projecteur P1	x 2.25 ; y -4.25 ; z 2.75	Option B4 ; lentille installée et adaptation support non validées
DJ	x -3.00 ; y 1.80 ; table 1,80 x 0,75	Proposé ; dégagement mur 0,367 m
Bar / poteaux	Mêmes volumes indicatifs dans les deux vues	Aucun relevé coté disponible ; collisions réelles non garanties
Lumières	34 existants actifs + 6 PAR proposés = 40	Positions reprises graphiquement ; accroches réelles à conserver

CALCUL DE COUVERTURE - IDENTIFIER LA LENTILLE AVANT DE FIXER LE REcul
Image demandée : cercle Ø 1,50 m ; image visible Ø 1,48 m, bord noir de 1 cm. Gabarit natif 16:10 = 2,432 x 1,52 m, diagonale 112.911 pouces. Le gabarit doit être masqué hors du cercle.
Option B4 : corps P1 x +2,25 ; y -4,25 ; z +2,75 m. Écran x +2,25 ; y +0,807 ; z +2,05 m. Lentille indicative avancée de 0,28 m : L = 4,25 - 0,28 + 0,807 = 4,777 m. Alignement horizontal : 0,00 m ; écart vertical : 2,75 - 0,01 - 2,05 = 0,69 m.
Zoom standard / ET-DLE170 : plage de recul 4.205 à 5.900 m, d'après les formules constructeur. 4,777 m est dans la plage. Décentrement vertical et référence réelle de mesure à contrôler. ET-DLE085 : plage 1.918 à 2.395 m ; ne convient pas à ce recul et à ce gabarit.
Conclusion conditionnelle : la position B4 est une option avec une optique appropriée, pas une installation confirmée avec la lentille actuelle. La salle décrit un montage ultra-court sans identifier sa lentille. Référence et disponibilité de l'optique indispensables avant de retenir B4.
Accroche : barre transversale reprise graphiquement ; cotes non relevées. Chief VCMU inventorié, mais adaptation, charge et longueur de suspension non documentées. Zoom 5 réservé à la dépose pour P1 ; 106 pour E1. Le dessin ne certifie ni leur déplacement ni la capacité de la structure. Corps à 0,505 m du comptoir indicatif ; visibilité, ventilation et obstacles réels à vérifier.
Source : Panasonic PT-RZ770 Spec File, pages 15–16 ; plan LX et fiche Audio-LX du Ministère. Les rayons sont un gabarit cible, pas une simulation de la lentille installée.

GRILLE SEULE - SECTIONS VIDES VISIBLES - COTES GRAPHIQUES APPROXIMATIVES

The diagram illustrates the stage layout with various sections and points. At the top, a dashed yellow box labeled 'FOND DE SCÈNE' contains three horizontal teal lines representing sections B3, B2, and B1 from top to bottom. A purple line segment labeled 'E1 / B1' is positioned on the B1 line. Below this, a horizontal teal line represents the 'NEZ DE SCÈNE / ORIGINE y = 0'. Three vertical teal lines, labeled L-G, L-C, and L-D from left to right, extend downwards from the 'NEZ DE SCÈNE' line. At the bottom, a horizontal teal line represents section B4. A purple square labeled 'P1 / B4' is located on the L-C line, with a dashed purple line connecting it to the 'E1 / B1' point above. A vertical dimension line on the right indicates a height of 'env. 4,25 m' from the B4 line to the 'NEZ DE SCÈNE' line.

Vert : tubes repérés. Jaune : rails à rideaux, accroche interdite.

Une section sans appareil n'est pas un point de charge validé.

POINTS PROPOSÉS ET LIMITES DU REPÉRAGE

B1–B3 : traverses de scène.
y ≈ +0,807 / +1,77 / +2,78 m depuis le bord avant.

B4 : traverse salle.
y ≈ -4,25 m. P1 proposé à x +2,25 m, dans l'axe d'E1. Environ 2,02 m du mur droit à l'axe, selon la largeur nominale.

L-G / L-C / L-D : tracés longitudinaux.
x ≈ -3,36 / -0,20 / +3,02 m ; de la scène vers B4. Repérage graphique : continuité, extrémités et nature de chaque tronçon à confirmer.

Section documentée : tubes carrés 2 x 2 pouces (50,8 mm). Aucun rail à rideaux, conduit de ventilation ou élément décoratif n'est retenu comme point d'accroche.

Priorités projection :
106 : dépose proposée pour la suspension E1 sur B1.
Zoom 5 : dépose proposée pour le support P1 sur B4.
Les deux restent à l'inventaire, sans nouvel emplacement attribué.

Avant montage : DT à consulter pour identification de la lentille, contrôle du support Chief VCMU, fixation adaptée au tube carré, capacité de charge, suspension secondaire, refroidissement et trajet optique réel.

Fidélité du modèle : mêmes segments et coordonnées dans le PDF et le 3D. Le dossier ne donne ni un relevé complet de tous les points cachés ni leurs charges admissibles. Ce repérage ne remplace pas la visite technique.