



01 IMPLANTATION SCÉNIQUE ET PISTE DE DANSE

Orientation de référence : depuis le public, écran à gauche et DJ à droite. Toutes les cotes sont en mètres.

A VUE DE DESSUS - 1:75

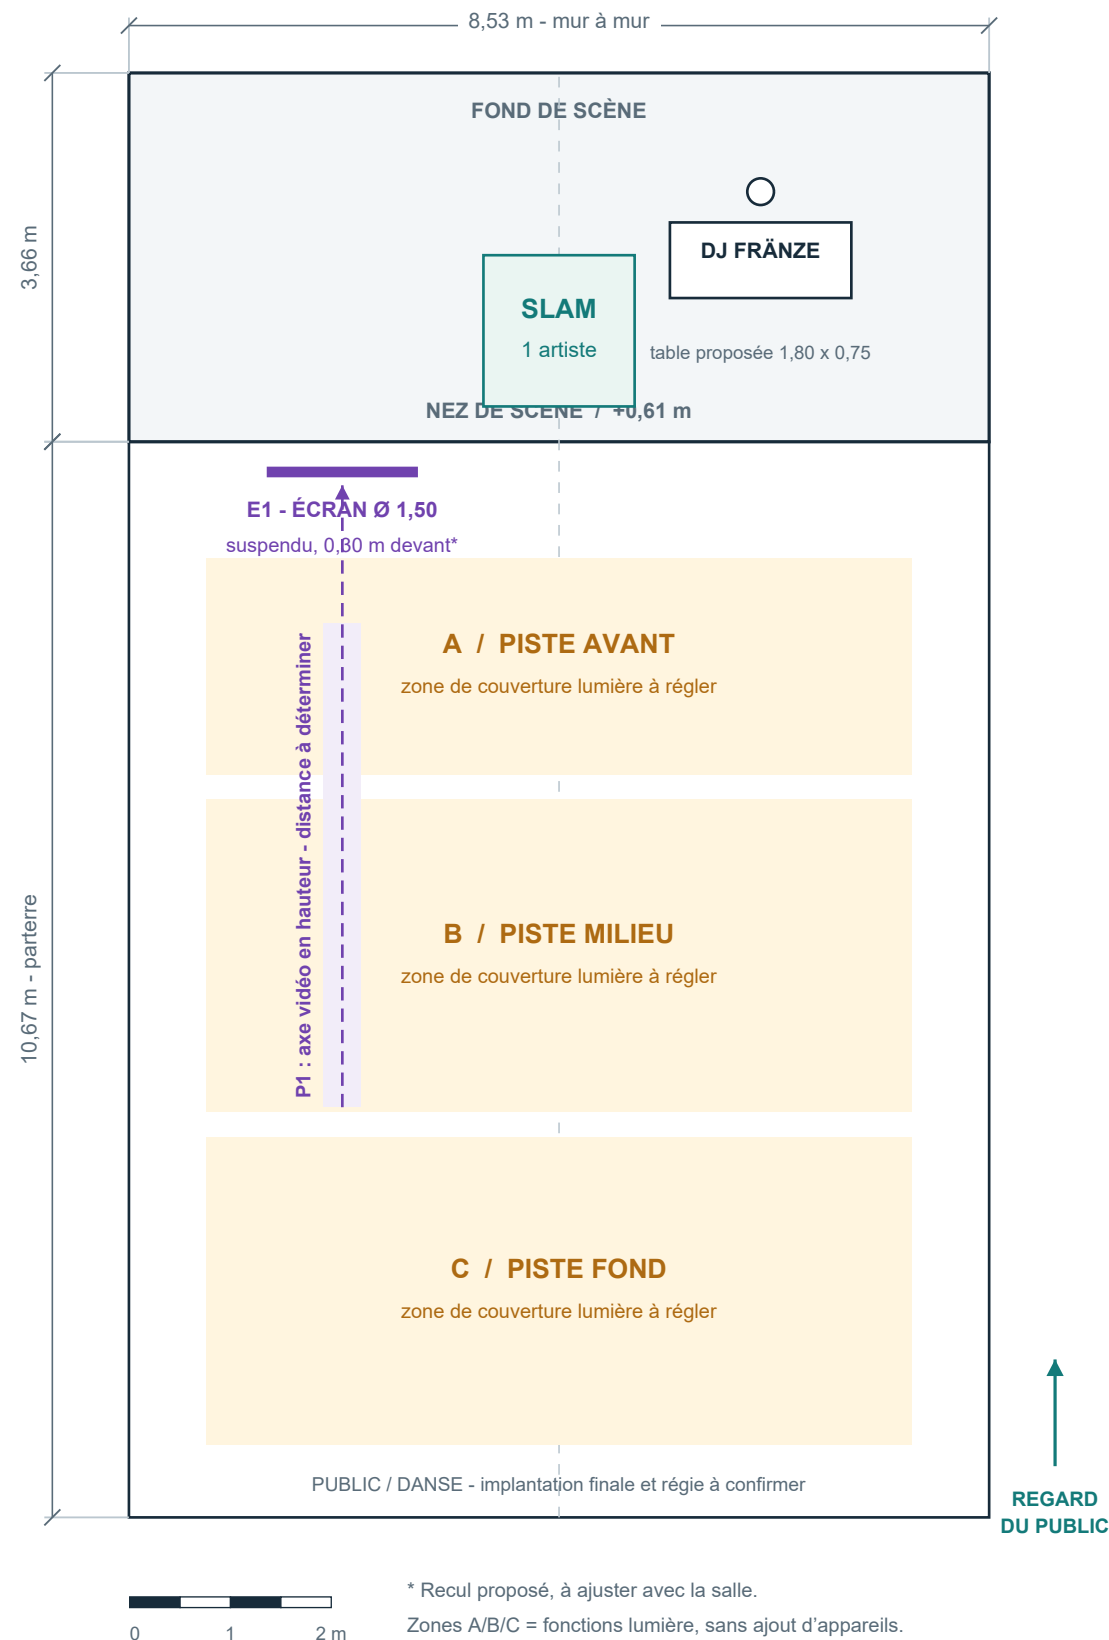

B VUE DE FACE DEPUIS LE PUBLIC - 1:50

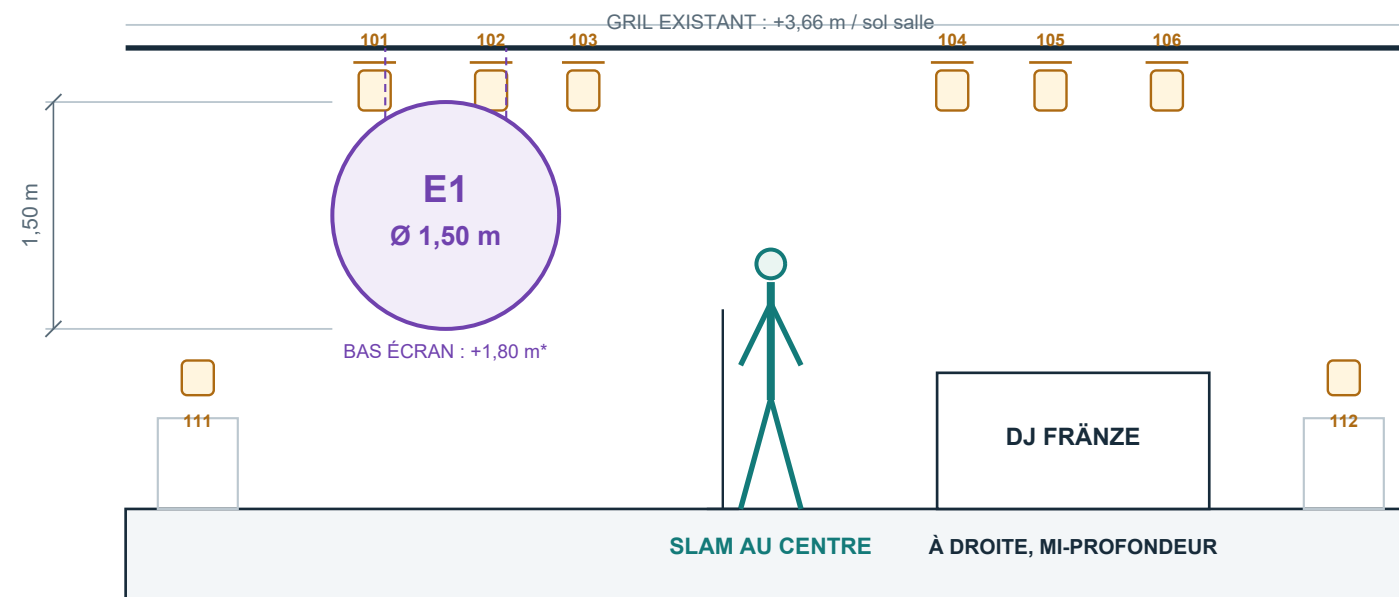

* Hauteur d'écran proposée. Accroches et visibilité à valider.

Symboles orange : Intimidator existants. Implantation complète : annexe, feuille 3.



C COTES D'IMPLANTATION PROPOSÉES

Élément	Position / dimensions	Statut
Écran E1	Centre x = -2,15 ; y = -0,30. Ø 1,50 ; bas z = 1,80 ; haut z = 3,30.	Côté et suspension demandés. Cotes exactes à valider.
Table DJ	Centre x = +2,00 ; y = +1,80. Emprise proposée : 1,80 x 0,75.	À droite, à mi-profondeur. Mesurer la table réelle.
Zone slam	Centre x = 0 ; y = +1,10. Zone proposée : 1,50 x 1,50.	Centre dégagé pour 1 artiste.
Vidéoprojecteur P1	Axe gauche aligné avec E1. Prévoir 0,30 à 0,50 m de réserve de recul.	Distance de base et support à confirmer. Réserve soumise à la plage optique.


Repère : origine x = 0 au centre du nez de scène ; x positif vers la droite du public ; y positif vers le fond de scène ; z depuis le sol de la salle. Les côtés gauche/droite de ce document sont toujours ceux du public.

Lecture : traits noirs = salle existante ; violet = projection proposée ; vert = slam ; ambre = éclairage de la piste. Imprimer à 100 % sur A3 pour conserver les échelles.

02 PROJECTION ET ÉCLAIRAGE DU PUBLIC

Conception avec le kit fixe du Ministère. Aucun appareil supplémentaire ni déplacement du kit n’est présumé.

D COUPE SUR L’AXE DE L’ÉCRAN GAUCHE - 1:50

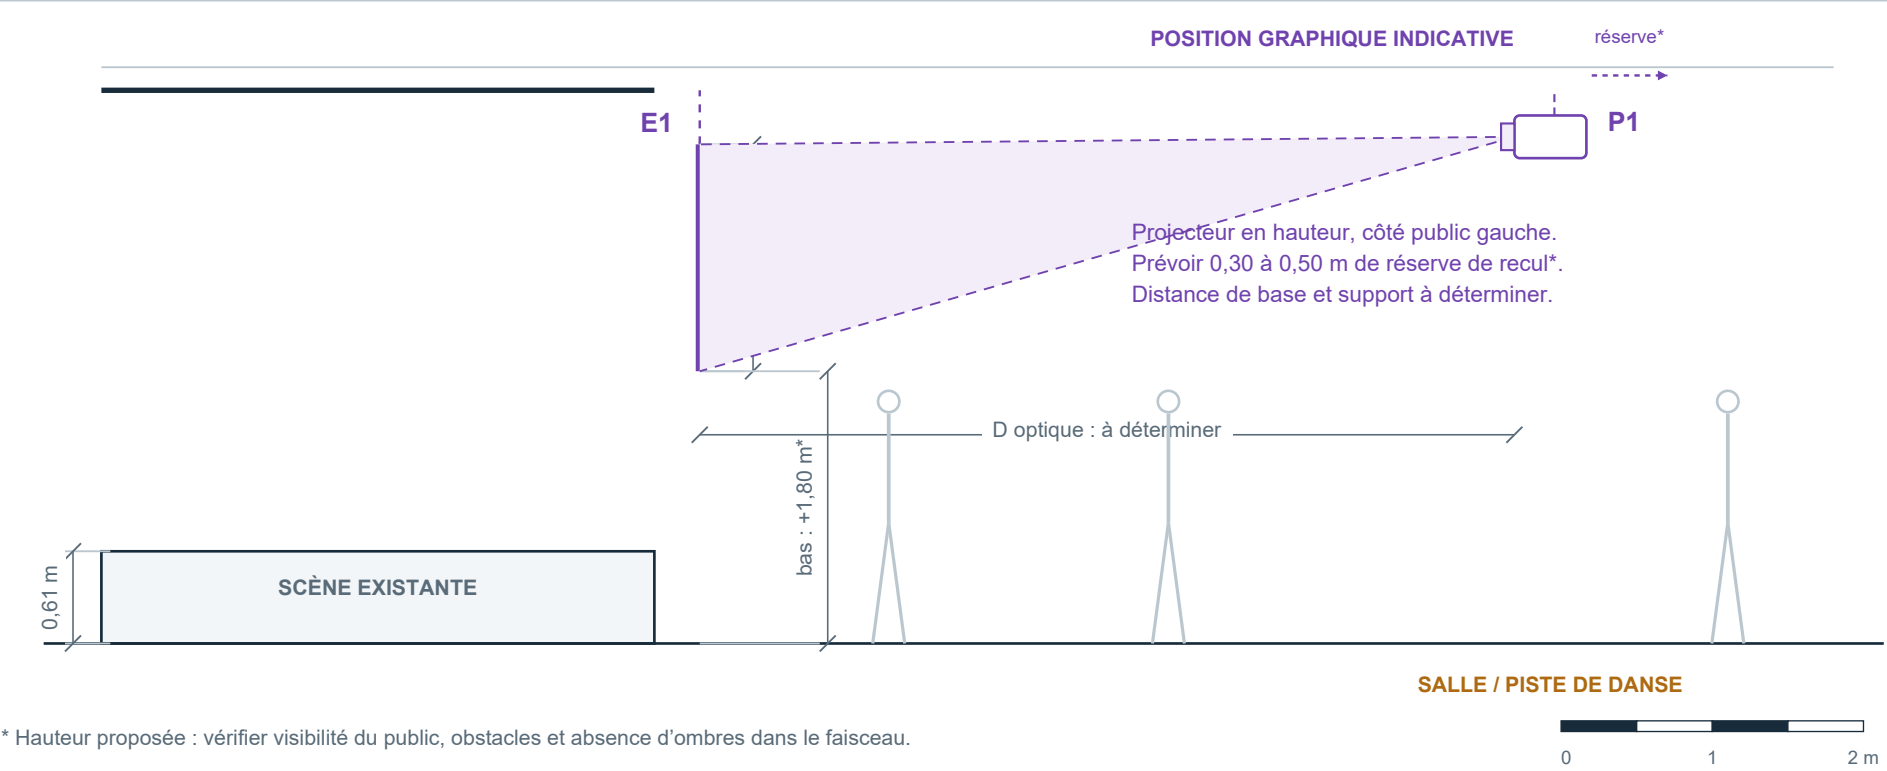

* Hauteur proposée : vérifier visibilité du public, obstacles et absence d’ombres dans le faisceau.

F PLAN DE FONCTIONS LUMIÈRE - SCÈNE ET PISTE

Groupe / matériel existant	Fonction proposée	Réglage / limite
Source Four / Colorado / DMG	Visage de l'artiste au centre ; table DJ à droite ; ambiance scénique.	Choisir les circuits au focus avec Rémi. Éviter tout débordement sur E1.
Intimidator 101 à 106 6 appareils suspendus	Éclairage dynamique de la piste. Répartir entre A avant, B milieu et C fond.	Affectation appareil-zone après essais. Faisceaux ouverts / zoom adapté ; amplitude limitée autour d'E1.
Intimidator 111 et 112 2 appareils bas existants	Complément d’effets pour la piste si les angles sont exploitables.	Vérifier l’éblouissement aux premiers rangs. Les exclure des effets public si les angles ne conviennent pas.
Éclairage général de salle	Accueil, entracte, sortie et circulation.	Circuits existants à identifier avec la salle. Ne pas les confondre avec les effets de spectacle.

Les huit Intimidator restent à leurs emplacements existants. Les zones A/B/C indiquent la couverture recherchée, pas de nouvelles accroches. La portée au fond du parterre reste à tester. Les effets mobiles ne garantissent pas un éclairage uniforme de toute la piste.

États proposés : slam = visage stable + piste discrète ; slam dansant = visage stable + mouvements doux dans la salle ; interlude/DJ = piste plus présente. Niveaux et vitesse à régler avec l’éclairagiste.

E VALIDATION DE LA PROJECTION

1. Identifier le matériel réellement utilisé

Le courriel de Rémi confirme une solution de projection et un câble HDMI. Il ne précise ni lentille ni position exploitable pour ce cercle.

2. Distance et petite réserve de recul

Calculer la distance selon la lentille ; prévoir 0,30 à 0,50 m d’ajustement vers l’arrière, si l’optique et l’accroche le permettent. Cette réserve ne valide pas un déplacement du support existant.

3. Préparer le masque circulaire

Un cercle de 1,50 m exige une image dont la hauteur utile couvre 1,50 m. À titre de calcul : largeur 2,67 m en 16:9 ou 2,40 m en 16:10 ; format réel à confirmer.

4. Tester avec l’éclairage de la piste

Régler focus, géométrie et masque. Vérifier la lumière résiduelle autour du cercle, les ombres du public et les positions des Intimidator qui touchent l’écran.

G BASE DOCUMENTAIRE ET INVENTAIRE

Plan joint par Rémi, Ministere23_Front.pdf :
8 Intimidator Spot 375Z ; 7 Source Four 36° ; 6 Source Four 25/50 Zoom ; 12 Colorado 1 Tour-Tri ; 1 DMG SL1 ; 2 DMG Mini Mix. Plan original reproduit en feuille 3.

Rémi, message daté du 6 mars, transféré par Ivy le 12 août 2026 : kit fixe ; Intimidator utilisables vers la salle. Tout ajout demande location, personnel d’installation et vérification de compatibilité GrandMA3.

Ivy, 31 août : scénographie comprenant les lumières sur scène et dans le public. 3 septembre : ébauche souhaitée début octobre, délai possible jusqu’au 10 octobre.

Fiche publique du Ministère : scène 28 x 12 pi ; hauteur 2 pi ; gril 10 pi au-dessus de la scène ; parterre 28 x 35 pi. Cotes nominales à contrôler sur place.

Décisions Cindy, 7 octobre : cercle env. 1,50 m suspendu devant à gauche ; DJ à droite à mi-profondeur ; slam central ; public dansant éclairé ; petite marge de recul du vidéoprojecteur.